## RK-L1-01 TAMPAK DEPAN

1:10 · L1-SERVER · 42U

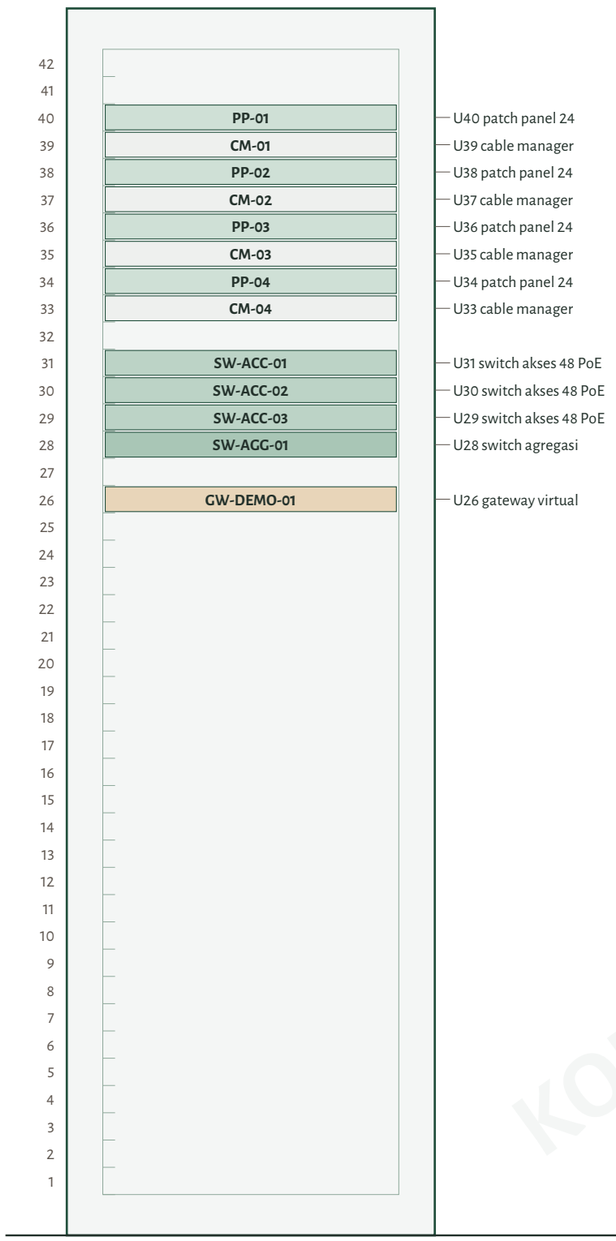


## RK-L1-02 TAMPAK DEPAN

1:10 · L1-SERVER · 42U

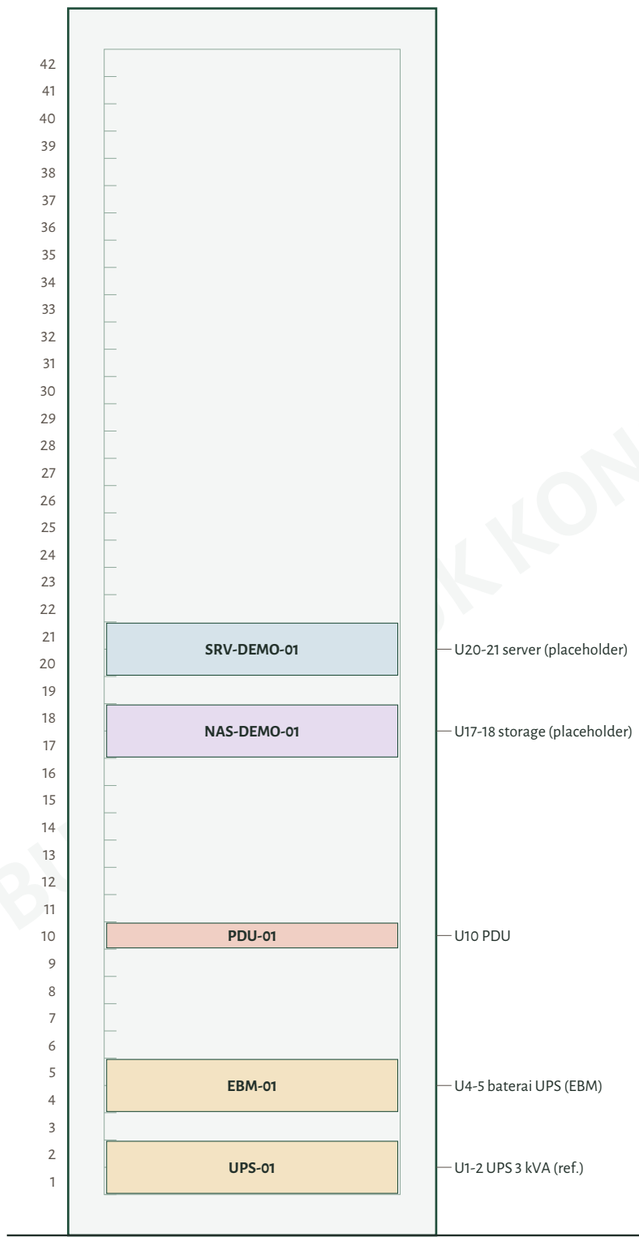


## CLEARANCE RACK 1:100 (AS-ICT-06)

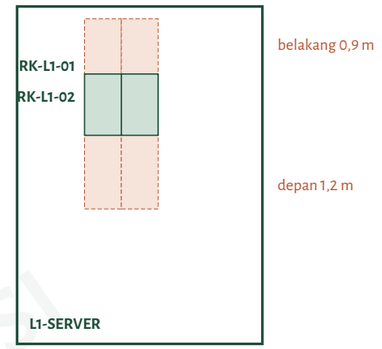


## ISI RACK (world.json racks[].contents)

| Rack | U | Tg | Perangkat | Tipe | Port |
|---|---|---|---|---|---|
| RK-L1-01 | U40 | 1 | PP-01 | patch panel 24 | 24 |
| RK-L1-01 | U39 | 1 | CM-01 | cable manager | - |
| RK-L1-01 | U38 | 1 | PP-02 | patch panel 24 | 24 |
| RK-L1-01 | U37 | 1 | CM-02 | cable manager | - |
| RK-L1-01 | U36 | 1 | PP-03 | patch panel 24 | 24 |
| RK-L1-01 | U35 | 1 | CM-03 | cable manager | - |
| RK-L1-01 | U34 | 1 | PP-04 | patch panel 24 | 24 |
| RK-L1-01 | U33 | 1 | CM-04 | cable manager | - |
| RK-L1-01 | U31 | 1 | SW-ACC-01 | switch akses 48 PoE | 48 |
| RK-L1-01 | U30 | 1 | SW-ACC-02 | switch akses 48 PoE | 48 |
| RK-L1-01 | U29 | 1 | SW-ACC-03 | switch akses 48 PoE | 48 |
| RK-L1-01 | U28 | 1 | SW-AGG-01 | switch agregasi | 24 |
| RK-L1-01 | U26 | 1 | GW-DEMO-01 | gateway virtual | 8 |
| RK-L1-02 | U20 | 2 | SRV-DEMO-01 | server (placeholder) | 2 |
| RK-L1-02 | U17 | 2 | NAS-DEMO-01 | storage (placeholder) | 2 |
| RK-L1-02 | U10 | 1 | PDU-01 | PDU | - |
| RK-L1-02 | U4 | 2 | EBM-01 | baterai UPS (EBM) | - |
| RK-L1-02 | U1 | 2 | UPS-01 | UPS 3 kVA (ref.) | - |

- Skala tampak rack 1:10; 1U = 44,45 mm, nomor U dihitung dari bawah. Tg = tinggi dalam U.
- Switch, UPS 3 kVA + 1 EBM = model referensi konsep (AS-ICT-07, AS-ICT-09), bukan keputusan beli; PDU belum dipilih; tanpa harga.
- Clearance depan 1,2 m / belakang 0,9 m adalah target konsep dari catalog (AS-ICT-06), wajib diverifikasi ke standar yang dipilih.

**STATUS KONSEP** — Bukan untuk konstruksi

**kantor-rpg** Proyek kantor-rpg · gedung KRPG-01

### Elevasi rack

Skala 1:10 @ A3 lanskap
Revisi P03 · 2026-10-01
Render 2026-10-05 05:43:54 UTC
Halaman 1/1
Digambar Claude Code cloud (generator)
Diperiksa Max (supervisor) belum review
Sumber world.json sha256 9361e1355d660520

Nomor lembar

**ICT-201**

Rev P03 · 1/1

Huruf: KantorRPG Sans, turunan Alegreya Sans karya Juan Pablo del Peral (SIL OFL 1.1, paket Debian fonts-alegreya-sans), subset tertanam.

KONSEP - BUKAN UNTUK KONSTRUKSI