


TOPOLOGI JARINGAN (VIRTUAL)

RANCANGAN VIRTUAL, BUKAN TOPOLOGI PRODUKSI

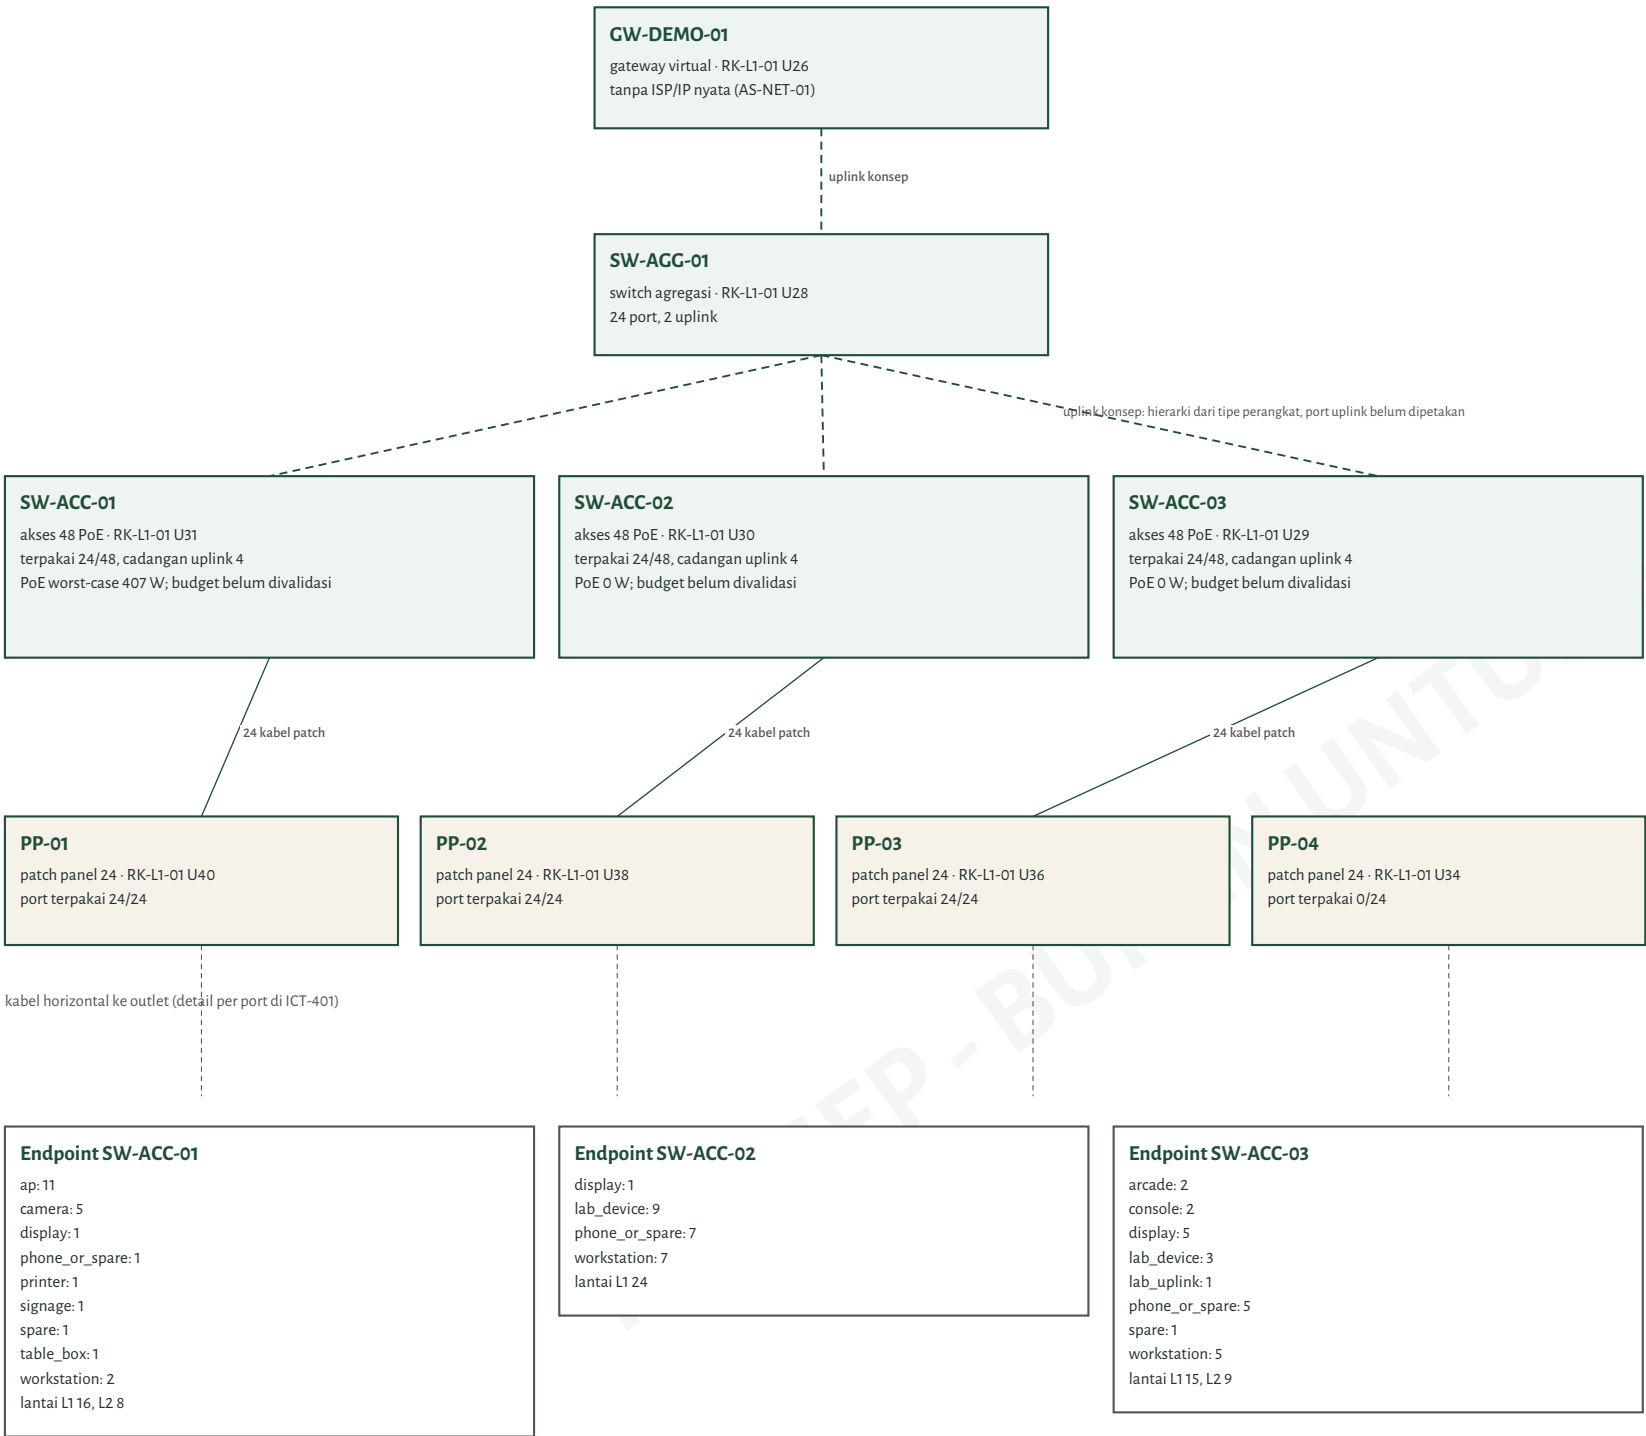

DOMAIN (ID abstrak, AS-NET-01)

| Domain     | Label  | Port | Catatan                    |
|------------|--------|------|----------------------------|
| NET-OFFICE | office | 48   | abstrak                    |
| NET-DEMO   | demo   | 10   | abstrak                    |
| NET-GUEST  | guest  | 0    | abstrak, SSID tamu konsep  |
| NET-LAB    | lab    | 14   | abstrak, terisolasi konsep |
| NET-SERVER | server | 0    | abstrak                    |

JUMLAH DARI DATA

|              |                                                                |
|--------------|----------------------------------------------------------------|
| Outlet       | 45 outlet, 72 port                                             |
| Patch panel  | 4 x 24 = 96 port, terpakai 72                                  |
| Access point | 11 placeholder (AS-ICT-01): L1 5, L2 6                         |
| Kamera       | 5 opsional konsep: L1 3, L2 2                                  |
| Kabel        | 72 kabel, total 2074,8 m (AS-ICT-02)                           |
| PoE          | worst-case 407 W dari kelas IEEE (AS-ICT-04); belum divalidasi |

RACK

|          |   |
|----------|---|
| RK-L1-01 | L1-SERVER, 42U: PP-01 U40, CM-01 U39, PP-02 U38, CM-02 U37, PP-03 U36, CM-03 U35, PP-04 U34, CM-04 U33, SW-ACC-01 U31, SW-ACC-02 U30, SW-ACC-03 U29, SW-AGG-01 U28, GW-DEMO-01 U26 |
| RK-L1-02 | L1-SERVER, 42U: SRV-DEMO-01 U20, NAS-DEMO-01 U17, PDU-01 U10, UPS-01 U1   |

SRV-DEMO-01 dan NAS-DEMO-01 belum punya port map; koneksinya tidak digambar.

STATUS KONSEP

Bukan untuk konstruksi

kantor-rpg Proyek kantor-rpg - gedung KRPG-01

Topologi jaringan (virtual)

|          |                                    |           |                               |
|----------|------------------------------------|-----------|-------------------------------|
| Skala    | NTS @ A3 lanskap                   | Revisi    | P02 - 2026-10-01              |
| Render   | 2026-10-01 12:12:53 UTC            | Halaman   | halaman 1/1                   |
| Digambar | Claude Code cloud (generator)      | Diperiksa | Max (supervisor) belum review |
| Sumber   | world.json sha256 ac39b320919d6410 |           |                               |

Nomor lembar

ICT-001

Rev P02 - 1/1

OUTLET, AP DAN KAMERA LANTAI 1

Skala 1:100 @ A2

Label outlet: ID (jumlah port), Tray di +3,2 m (AS-ICT-02), AP placeholder tanpa klaim radius Wi-Fi (AS-ICT-01).



Rancangan virtual, bukan topologi produksi

Lantai L1: Lantai 1 - Kerja & Kunjungan

Sumber: world.json ict + design/derived/ict-portmap.json

LEGENDA

△ Outlet data (segitiga), label ID (port)

□ Kamera opsional + arah konsep (bukan FOV terukur)

■ Riser vertikal ke lantai lain

○ Access point placeholder (AS-ICT-01)

— Tray kabel +3,2 m

■ Rack 42U (target)

OUTLET L1 (30 outlet, 55 port)

| ID        | Ruang | Port | Domain | Melayani  | ID        | Ruang | Port | Domain | Melayani  |
|-----------|-------|------|--------|-----------|-----------|-------|------|--------|-----------|
| TO-L1-001 | LOBBY | 2    | OFFICE | FX-L1-001 | TO-L1-016 | LAB   | 4    | LAB    | FX-L1-077 |
| TO-L1-002 | LOBBY | 1    | DEMO   | FX-L1-009 | TO-L1-017 | LAB   | 2    | LAB    | FX-L1-079 |
| TO-L1-003 | MEET  | 2    | OFFICE | FX-L1-011 | TO-L1-018 | CEO   | 2    | OFFICE | FX-L1-082 |
| TO-L1-004 | MEET  | 1    | OFFICE | FX-L1-022 | TO-L1-019 | HUGO  | 2    | OFFICE | FX-L1-089 |
| TO-L1-005 | IMPL  | 2    | OFFICE | FX-L1-053 | TO-L1-020 | HUGO  | 2    | OFFICE | FX-L1-091 |
| TO-L1-006 | IMPL  | 2    | OFFICE | FX-L1-055 | TO-L1-021 | KEVIN | 2    | OFFICE | FX-L1-096 |
| TO-L1-007 | IMPL  | 2    | OFFICE | FX-L1-057 | TO-L1-022 | BRUNO | 2    | OFFICE | FX-L1-101 |
| TO-L1-008 | IMPL  | 2    | OFFICE | FX-L1-059 | TO-L1-023 | LOBBY | 1    | OFFICE | AP-L1-01  |
| TO-L1-009 | IMPL  | 2    | OFFICE | FX-L1-061 | TO-L1-024 | IMPL  | 1    | OFFICE | AP-L1-02  |
| TO-L1-010 | IMPL  | 2    | OFFICE | FX-L1-063 | TO-L1-025 | CORR  | 1    | OFFICE | AP-L1-03  |
| TO-L1-011 | IMPL  | 1    | OFFICE | FX-L1-065 | TO-L1-026 | NCORR | 1    | OFFICE | AP-L1-04  |
| TO-L1-012 | NOVA  | 2    | OFFICE | FX-L1-069 | TO-L1-027 | NCORR | 1    | OFFICE | AP-L1-05  |
| TO-L1-013 | NOVA  | 2    | OFFICE | FX-L1-071 | TO-L1-028 | LOBBY | 1    | OFFICE | CAM-L1-01 |
| TO-L1-014 | LAB   | 4    | LAB    | FX-L1-075 | TO-L1-029 | CORR  | 1    | OFFICE | CAM-L1-02 |
| TO-L1-015 | LAB   | 4    | LAB    | FX-L1-076 | TO-L1-030 | BRUNO | 1    | OFFICE | CAM-L1-03 |

PERANGKAT L1 (AP 5, kamera 3)

| ID        | Ruang | Outlet    | Tinggi | PoE | Status                                     |
|-----------|-------|-----------|--------|-----|--------------------------------------------|
| AP-L1-01  | LOBBY | TO-L1-023 | 3,0 m  | 4   | placeholder (AS-ICT-01)                    |
| AP-L1-02  | IMPL  | TO-L1-024 | 3,0 m  | 4   | placeholder (AS-ICT-01)                    |
| AP-L1-03  | CORR  | TO-L1-025 | 3,0 m  | 4   | placeholder (AS-ICT-01)                    |
| AP-L1-04  | NCORR | TO-L1-026 | 3,0 m  | 4   | placeholder (AS-ICT-01)                    |
| AP-L1-05  | NCORR | TO-L1-027 | 3,0 m  | 4   | placeholder (AS-ICT-01)                    |
| CAM-L1-01 | LOBBY | TO-L1-028 | 2,8 m  | 3   | opsional konsep, privacy mask perlu kajian |
| CAM-L1-02 | CORR  | TO-L1-029 | 2,8 m  | 3   | opsional konsep, privacy mask perlu kajian |
| CAM-L1-03 | BRUNO | TO-L1-030 | 2,8 m  | 3   | opsional konsep, privacy mask perlu kajian |

ASUMSI

- AS-ICT-01** Jumlah AP adalah placeholder; belum ada model site/material dan target coverage. Tidak ada radius Wi-Fi efektif yang diklaim.
- AS-ICT-02** Slack kabel: 3,0 m sisi rack + 0,3 m sisi outlet; tray pada 3,2 m di atas lantai jadi; outlet meja 0,3 m; outlet plafon 3,0 m. Asumsi proyek, bukan standar.
- AS-ICT-03** Batas panjang permanent link 90 m dipakai sebagai target konsep (praktik umum kabel tembaga terstruktur), wajib diverifikasi ke standar yang dipilih.
- AS-NET-01** Domain jaringan office/demo/guest/lab/server adalah ID abstrak; bukan subnet, VLAN atau perangkat produksi.

STATUS KONSEP

Bukan untuk konstruksi

**kantor-rpg** Proyek kantor-rpg - gedung KRPG-01  
**Outlet, AP dan kamera Lantai 1**

Skala 1:100 @ A2 lanskap  
Render 2026-10-01 12:12:53 UTC  
Digambar Claude Code cloud (generator)  
Sumber world.json sha256 ac39b320919d6410

Revisi P02 - 2026-10-01  
Halaman halaman 1/1  
Diperiksa Max (supervisor) belum review

Nomor lembar

ICT-101

Rev P02 - 1/1

OUTLET, AP DAN KAMERA LANTAI 2

Skala 1:100 @ A2

Label outlet: ID (jumlah port). Tray di +3,2 m (AS-ICT-02). AP placeholder tanpa klaim radius Wi-Fi (AS-ICT-01).



Rancangan virtual, bukan topologi produksi

Lantai L2: Lantai 2 - Rekreasi  
Sumber: world.json ict + design/derived/ict-portmap.json

LEGENDA

- Outlet data (segitiga), label ID (port)
- Access point placeholder (AS-ICT-01)
- Kamera opsional + arah konsep (bukan FOV terukur)
- Tray kabel +3,2 m
- Riservertikal ke lantai lain
- Rack 42U (target)

OUTLET L2 (15 outlet, 17 port)

| ID        | Ruang    | Port | Domain | Melayani  | ID        | Ruang | Port | Domain | Melayani  |
|-----------|----------|------|--------|-----------|-----------|-------|------|--------|-----------|
| TO-L2-001 | DINE     | 1    | DEMO   | FX-L2-034 | TO-L2-009 | DINE  | 1    | OFFICE | AP-L2-02  |
| TO-L2-002 | GAME     | 2    | DEMO   | FX-L2-058 | TO-L2-010 | GAME  | 1    | OFFICE | AP-L2-03  |
| TO-L2-003 | GAME     | 2    | DEMO   | FX-L2-061 | TO-L2-011 | CORR  | 1    | OFFICE | AP-L2-04  |
| TO-L2-004 | GAME     | 1    | DEMO   | FX-L2-064 | TO-L2-012 | NCORR | 1    | OFFICE | AP-L2-05  |
| TO-L2-005 | GAME     | 1    | DEMO   | FX-L2-065 | TO-L2-013 | GYM   | 1    | OFFICE | AP-L2-06  |
| TO-L2-006 | BILLIARD | 1    | DEMO   | FX-L2-079 | TO-L2-014 | CORR  | 1    | OFFICE | CAM-L2-01 |
| TO-L2-007 | GYM      | 1    | DEMO   | FX-L2-087 | TO-L2-015 | NCORR | 1    | OFFICE | CAM-L2-02 |
| TO-L2-008 | LOUNGE   | 1    | OFFICE | AP-L2-01  |           |       |      |        |           |

PERANGKAT L2 (AP 6, kamera 2)

| ID        | Ruang  | Outlet    | Tinggi | PoE | Status                                     |
|-----------|--------|-----------|--------|-----|--------------------------------------------|
| AP-L2-01  | LOUNGE | TO-L2-008 | 3,0 m  | 4   | placeholder (AS-ICT-01)                    |
| AP-L2-02  | DINE   | TO-L2-009 | 3,0 m  | 4   | placeholder (AS-ICT-01)                    |
| AP-L2-03  | GAME   | TO-L2-010 | 3,0 m  | 4   | placeholder (AS-ICT-01)                    |
| AP-L2-04  | CORR   | TO-L2-011 | 3,0 m  | 4   | placeholder (AS-ICT-01)                    |
| AP-L2-05  | NCORR  | TO-L2-012 | 3,0 m  | 4   | placeholder (AS-ICT-01)                    |
| AP-L2-06  | GYM    | TO-L2-013 | 3,0 m  | 4   | placeholder (AS-ICT-01)                    |
| CAM-L2-01 | CORR   | TO-L2-014 | 2,8 m  | 3   | opsional konsep, privacy mask perlu kajian |
| CAM-L2-02 | NCORR  | TO-L2-015 | 2,8 m  | 3   | opsional konsep, privacy mask perlu kajian |

ASUMSI

- AS-ICT-01** Jumlah AP adalah placeholder; belum ada model site/material dan target coverage. Tidak ada radius Wi-Fi efektif yang diklaim.
- AS-ICT-02** Slack kabel: 3,0 m sisi rack + 0,3 m sisi outlet; tray pada 3,2 m di atas lantai jadi; outlet meja 0,3 m; outlet plafon 3,0 m. Asumsi proyek, bukan standar.
- AS-ICT-03** Batas panjang permanent link 90 m dipakai sebagai target konsep (praktik umum kabel tembaga terstruktur), wajib diverifikasi ke standar yang dipilih.
- AS-NET-01** Domain jaringan office/demo/guest/lab/server adalah ID abstrak; bukan subnet, VLAN atau perangkat produksi.

STATUS KONSEP

Bukan untuk konstruksi

kantor-rpg  
Outlet, AP dan kamera Lantai 2


|          |                                    |           |                               |
|----------|------------------------------------|-----------|-------------------------------|
| Skala    | 1:100 @ A2 lanskap                 | Revisi    | P02 - 2026-10-01              |
| Render   | 2026-10-01 12:12:53 UTC            | Halaman   | halaman 1/1                   |
| Digambar | Claude Code cloud (generator)      | Diperiksa | Max (supervisor) belum review |
| Sumber   | world.json sha256 ac39b320919d6410 |           |                               |

Nomor lembar


ICT-102

Rev P02 - 1/1


RK-L1-01 TAMPAK DEPAN 1:20 · L1-SERVER · 42U

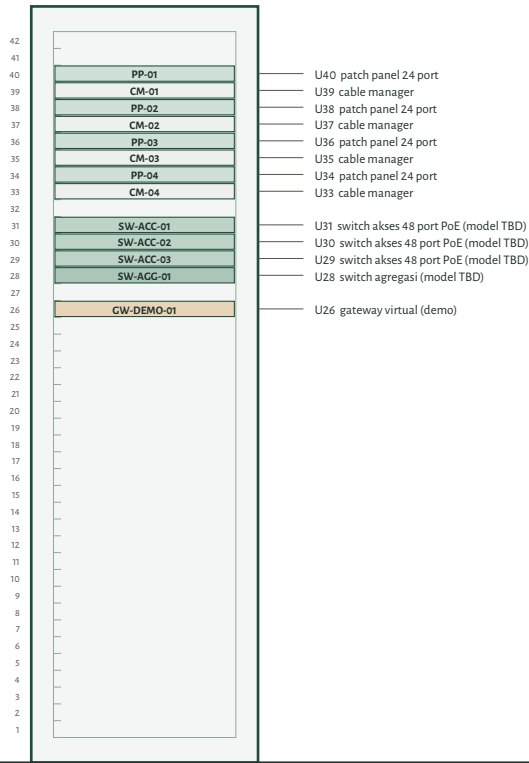

RK-L1-02 TAMPAK DEPAN 1:20 · L1-SERVER · 42U

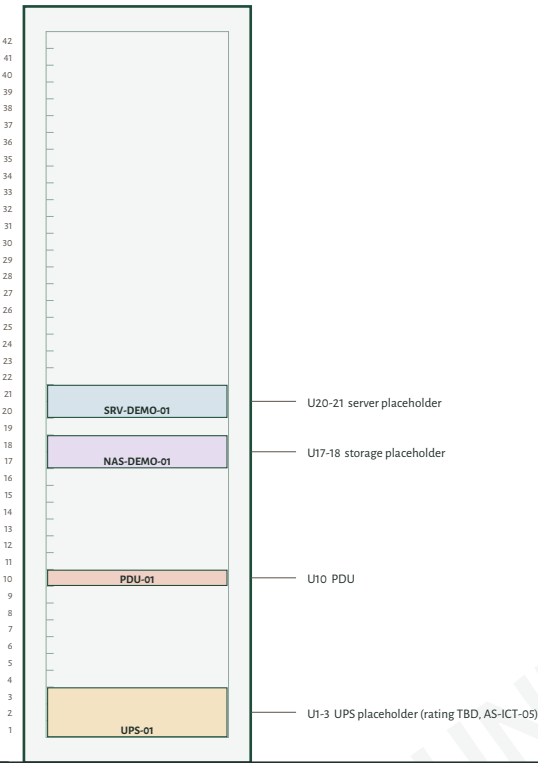

CLEARANCE RACK 1:100 (AS-ICT-06)

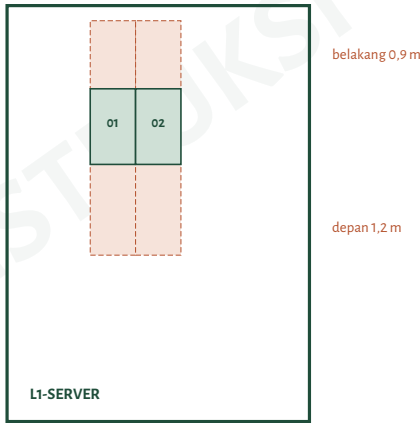

ISI RACK (world.json racks[].contents)

| Rack     | U   | Tinggi | Perangkat   | Tipe                                    | Port |
|----------|-----|--------|-------------|-----------------------------------------|------|
| RK-L1-01 | U40 | 1      | PP-01       | patch panel 24 port                     | 24   |
| RK-L1-01 | U39 | 1      | CM-01       | cable manager                           | -    |
| RK-L1-01 | U38 | 1      | PP-02       | patch panel 24 port                     | 24   |
| RK-L1-01 | U37 | 1      | CM-02       | cable manager                           | -    |
| RK-L1-01 | U36 | 1      | PP-03       | patch panel 24 port                     | 24   |
| RK-L1-01 | U35 | 1      | CM-03       | cable manager                           | -    |
| RK-L1-01 | U34 | 1      | PP-04       | patch panel 24 port                     | 24   |
| RK-L1-01 | U33 | 1      | CM-04       | cable manager                           | -    |
| RK-L1-01 | U31 | 1      | SW-ACC-01   | switch akses 48 port PoE (model TBD)    | 48   |
| RK-L1-01 | U30 | 1      | SW-ACC-02   | switch akses 48 port PoE (model TBD)    | 48   |
| RK-L1-01 | U29 | 1      | SW-ACC-03   | switch akses 48 port PoE (model TBD)    | 48   |
| RK-L1-01 | U28 | 1      | SW-AGG-01   | switch agregasi (model TBD)             | 24   |
| RK-L1-01 | U26 | 1      | GW-DEMO-01  | gateway virtual (demo)                  | 8    |
| RK-L1-02 | U20 | 2      | SRV-DEMO-01 | server placeholder                      | 2    |
| RK-L1-02 | U17 | 2      | NAS-DEMO-01 | storage placeholder                     | 2    |
| RK-L1-02 | U10 | 1      | PDU-01      | PDU                                     | -    |
| RK-L1-02 | U1  | 3      | UPS-01      | UPS placeholder (rating TBD, AS-ICT-05) | -    |

- Skala tampak rack 1:20; 1U = 44,45 mm, nomor U dihitung dari bawah.
- Model switch, PDU dan UPS belum dipilih (AS-ICT-04, AS-ICT-05); tidak ada harga.
- Clearance depan 1,2 m / belakang 0,9 m adalah target konsep dari catalog (AS-ICT-06), wajib diverifikasi ke standar yang dipilih.

STATUS KONSEP

Bukan untuk konstruksi

kantor-rpg Proyek kantor-rpg · gedung KRPG-01

Elevasi rack


|          |                                    |           |                               |
|----------|------------------------------------|-----------|-------------------------------|
| Skala    | 1:20 @ A3 lanskap                  | Revisi    | PO2 · 2026-10-01              |
| Render   | 2026-10-01 12:12:53 UTC            | Halaman   | halaman 1/1                   |
| Digambar | Claude Code cloud (generator)      | Diperiksa | Max (supervisor) belum review |
| Sumber   | world.json sha256 ac39b320919d6410 |           |                               |

Nomor lembar


ICT-201

Rev PO2 · 1/1

JALUR KABEL L1 1:200 - tray +3,2 m

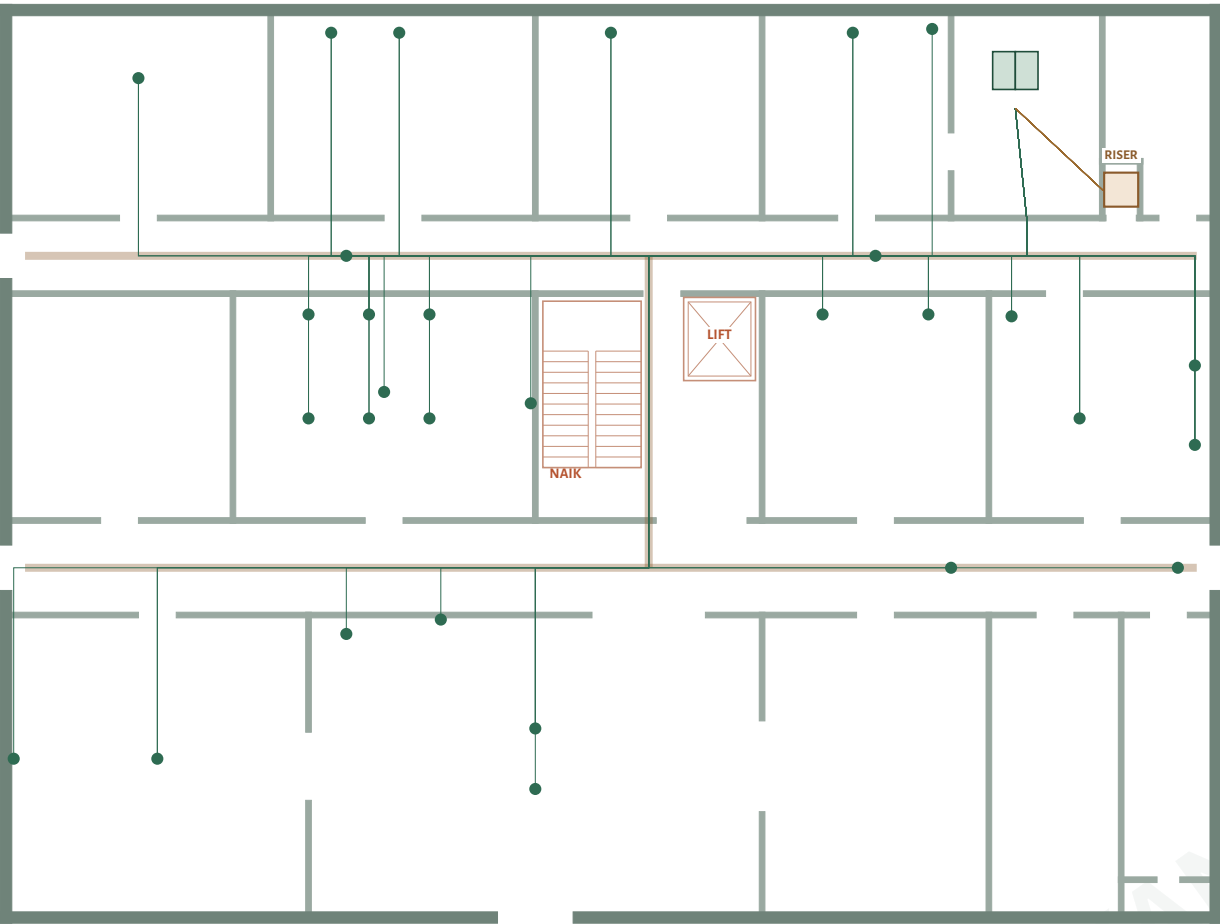

JALUR KABEL L2 1:200 - tray +3,2 m

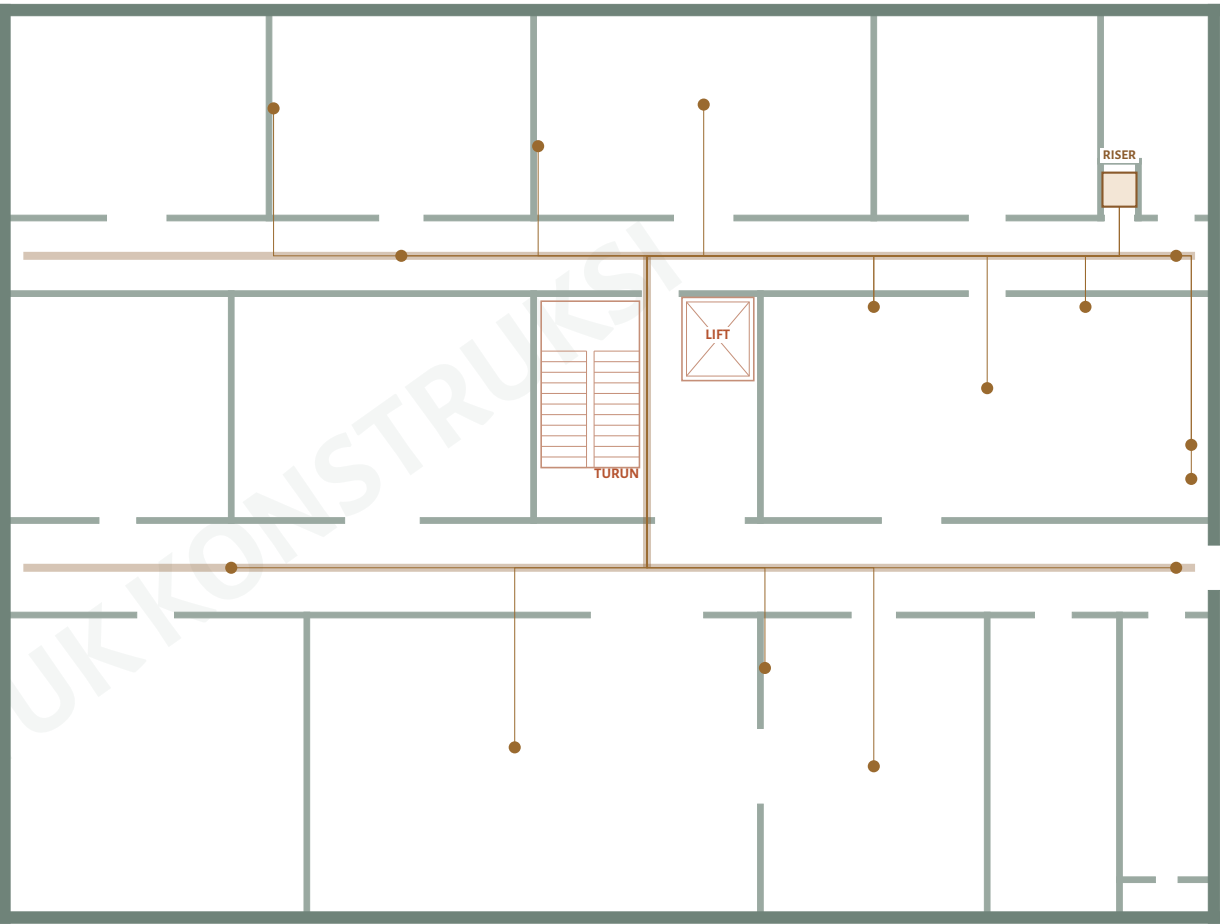


RINGKASAN PANJANG KABEL (ict-portmap.json)

| Lantai | Kabel | Total m | Min m | Maks m | Rata m |
|--------|-------|---------|-------|--------|--------|
| L1     | 55    | 1537,1  | 12,7  | 50,6   | 27,9   |
| L2     | 17    | 537,7   | 15,6  | 48,9   | 31,6   |
| Total  | 72    | 2074,8  | 12,7  | 50,6   | 28,8   |

Cek: jumlah baris 2074,8 m vs total port map 2074,8 m: COCOK. Semua kabel di bawah target 90 m (AS-ICT-03).

SKEMA RISER

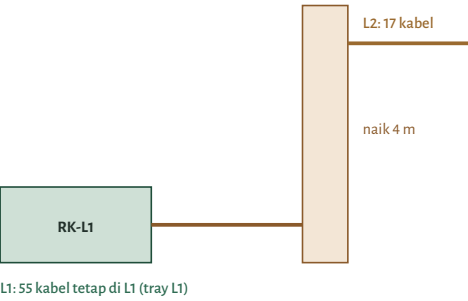

- Garis hijau = kabel endpoint L1, coklat = kabel endpoint L2 (bagian di L1 ikut warna lantai tujuan).
- Panjang = route tray + naik rack 1,2 m + riser 4,0 m (L2) + drop + slack 3,3 m (AS-ICT-02).



STATUS KONSEP

Bukan untuk konstruksi

kantor-rpg Proyek kantor-rpg - gedung KRPG-01  
Pathway dan riser

Skala 1:200 @ A3 lanskap  
Render 2026-10-01 12:12:53 UTC  
Digambar Claude Code cloud (generator)  
Sumber world.json sha256 ac39b320919d6410

Revisi P02 - 2026-10-01  
Halaman halaman 1/1  
Diperiksa Max (supervisor) belum review

Nomor lembar

ICT-301

Rev P02 · 1/1

PORT SCHEDULE

rancangan virtual, bukan topologi produksi · sumber design/derived/ict-portmap.json (world P02)

| Kabel         | Port outlet | Ruang     | PP/port  | Switch/port  | Domain     | PoE | m    | Label sisi rack        | Label sisi outlet      | Endpoint                 |
|---------------|-------------|-----------|----------|--------------|------------|-----|------|------------------------|------------------------|--------------------------|
| C-TO-L1-023-A | TO-L1-023-A | L1-LOBBY  | PP-01/01 | SW-ACC-01/01 | NET-OFFICE | 4   | 35,8 | PP-01-01 > TO-L1-023-A | TO-L1-023-A > PP-01-01 | ap AP-L1-01              |
| C-TO-L1-024-A | TO-L1-024-A | L1-IMPL   | PP-01/02 | SW-ACC-01/02 | NET-OFFICE | 4   | 29,3 | PP-01-02 > TO-L1-024-A | TO-L1-024-A > PP-01-02 | ap AP-L1-02              |
| C-TO-L1-025-A | TO-L1-025-A | L1-CORR   | PP-01/03 | SW-ACC-01/03 | NET-OFFICE | 4   | 34,9 | PP-01-03 > TO-L1-025-A | TO-L1-025-A > PP-01-03 | ap AP-L1-03              |
| C-TO-L1-026-A | TO-L1-026-A | L1-NCORR  | PP-01/04 | SW-ACC-01/04 | NET-OFFICE | 4   | 26,7 | PP-01-04 > TO-L1-026-A | TO-L1-026-A > PP-01-04 | ap AP-L1-04              |
| C-TO-L1-027-A | TO-L1-027-A | L1-NCORR  | PP-01/05 | SW-ACC-01/05 | NET-OFFICE | 4   | 12,7 | PP-01-05 > TO-L1-027-A | TO-L1-027-A > PP-01-05 | ap AP-L1-05              |
| C-TO-L1-028-A | TO-L1-028-A | L1-LOBBY  | PP-01/06 | SW-ACC-01/06 | NET-OFFICE | 3   | 36,7 | PP-01-06 > TO-L1-028-A | TO-L1-028-A > PP-01-06 | camera CAM-L1-01         |
| C-TO-L1-029-A | TO-L1-029-A | L1-CORR   | PP-01/07 | SW-ACC-01/07 | NET-OFFICE | 3   | 40,9 | PP-01-07 > TO-L1-029-A | TO-L1-029-A > PP-01-07 | camera CAM-L1-02         |
| C-TO-L1-030-A | TO-L1-030-A | L1-BRUNO  | PP-01/08 | SW-ACC-01/08 | NET-OFFICE | 3   | 17,2 | PP-01-08 > TO-L1-030-A | TO-L1-030-A > PP-01-08 | camera CAM-L1-03         |
| C-TO-L2-008-A | TO-L2-008-A | L2-LOUNGE | PP-01/09 | SW-ACC-01/09 | NET-OFFICE | 4   | 43,1 | PP-01-09 > TO-L2-008-A | TO-L2-008-A > PP-01-09 | ap AP-L2-01              |
| C-TO-L2-009-A | TO-L2-009-A | L2-DINE   | PP-01/10 | SW-ACC-01/10 | NET-OFFICE | 4   | 46,1 | PP-01-10 > TO-L2-009-A | TO-L2-009-A > PP-01-10 | ap AP-L2-02              |
| C-TO-L2-010-A | TO-L2-010-A | L2-GAME   | PP-01/11 | SW-ACC-01/11 | NET-OFFICE | 4   | 21,1 | PP-01-11 > TO-L2-010-A | TO-L2-010-A > PP-01-11 | ap AP-L2-03              |
| C-TO-L2-011-A | TO-L2-011-A | L2-CORR   | PP-01/12 | SW-ACC-01/12 | NET-OFFICE | 4   | 45,9 | PP-01-12 > TO-L2-011-A | TO-L2-011-A > PP-01-12 | ap AP-L2-04              |
| C-TO-L2-012-A | TO-L2-012-A | L2-NCORR  | PP-01/13 | SW-ACC-01/13 | NET-OFFICE | 4   | 33,1 | PP-01-13 > TO-L2-012-A | TO-L2-012-A > PP-01-13 | ap AP-L2-05              |
| C-TO-L2-013-A | TO-L2-013-A | L2-GYM    | PP-01/14 | SW-ACC-01/14 | NET-OFFICE | 4   | 29,1 | PP-01-14 > TO-L2-013-A | TO-L2-013-A > PP-01-14 | ap AP-L2-06              |
| C-TO-L2-014-A | TO-L2-014-A | L2-CORR   | PP-01/15 | SW-ACC-01/15 | NET-OFFICE | 3   | 48,9 | PP-01-15 > TO-L2-014-A | TO-L2-014-A > PP-01-15 | camera CAM-L2-01         |
| C-TO-L2-015-A | TO-L2-015-A | L2-NCORR  | PP-01/16 | SW-ACC-01/16 | NET-OFFICE | 3   | 15,6 | PP-01-16 > TO-L2-015-A | TO-L2-015-A > PP-01-16 | camera CAM-L2-02         |
| C-TO-L1-001-A | TO-L1-001-A | L1-LOBBY  | PP-01/17 | SW-ACC-01/17 | NET-OFFICE | -   | 36,9 | PP-01-17 > TO-L1-001-A | TO-L1-001-A > PP-01-17 | workstation FX-L1-001    |
| C-TO-L1-001-B | TO-L1-001-B | L1-LOBBY  | PP-01/18 | SW-ACC-01/18 | NET-OFFICE | -   | 36,9 | PP-01-18 > TO-L1-001-B | TO-L1-001-B > PP-01-18 | printer FX-L1-001        |
| C-TO-L1-002-A | TO-L1-002-A | L1-LOBBY  | PP-01/19 | SW-ACC-01/19 | NET-DEMO   | -   | 35,6 | PP-01-19 > TO-L1-002-A | TO-L1-002-A > PP-01-19 | signage FX-L1-009        |
| C-TO-L1-003-A | TO-L1-003-A | L1-MEET   | PP-01/20 | SW-ACC-01/20 | NET-OFFICE | -   | 47,7 | PP-01-20 > TO-L1-003-A | TO-L1-003-A > PP-01-20 | table_box FX-L1-011      |
| C-TO-L1-003-B | TO-L1-003-B | L1-MEET   | PP-01/21 | SW-ACC-01/21 | NET-OFFICE | -   | 47,7 | PP-01-21 > TO-L1-003-B | TO-L1-003-B > PP-01-21 | spare FX-L1-011          |
| C-TO-L1-004-A | TO-L1-004-A | L1-MEET   | PP-01/22 | SW-ACC-01/22 | NET-OFFICE | -   | 50,6 | PP-01-22 > TO-L1-004-A | TO-L1-004-A > PP-01-22 | display FX-L1-022        |
| C-TO-L1-005-A | TO-L1-005-A | L1-IMPL   | PP-01/23 | SW-ACC-01/23 | NET-OFFICE | -   | 34,7 | PP-01-23 > TO-L1-005-A | TO-L1-005-A > PP-01-23 | workstation FX-L1-053    |
| C-TO-L1-005-B | TO-L1-005-B | L1-IMPL   | PP-01/24 | SW-ACC-01/24 | NET-OFFICE | -   | 34,7 | PP-01-24 > TO-L1-005-B | TO-L1-005-B > PP-01-24 | phone_or_spare FX-L1-053 |
| C-TO-L1-006-A | TO-L1-006-A | L1-IMPL   | PP-02/01 | SW-ACC-02/01 | NET-OFFICE | -   | 31,9 | PP-02-01 > TO-L1-006-A | TO-L1-006-A > PP-02-01 | workstation FX-L1-055    |
| C-TO-L1-006-B | TO-L1-006-B | L1-IMPL   | PP-02/02 | SW-ACC-02/02 | NET-OFFICE | -   | 31,9 | PP-02-02 > TO-L1-006-B | TO-L1-006-B > PP-02-02 | phone_or_spare FX-L1-055 |
| C-TO-L1-007-A | TO-L1-007-A | L1-IMPL   | PP-02/03 | SW-ACC-02/03 | NET-OFFICE | -   | 33,1 | PP-02-03 > TO-L1-007-A | TO-L1-007-A > PP-02-03 | workstation FX-L1-057    |
| C-TO-L1-007-B | TO-L1-007-B | L1-IMPL   | PP-02/04 | SW-ACC-02/04 | NET-OFFICE | -   | 33,1 | PP-02-04 > TO-L1-007-B | TO-L1-007-B > PP-02-04 | phone_or_spare FX-L1-057 |
| C-TO-L1-008-A | TO-L1-008-A | L1-IMPL   | PP-02/05 | SW-ACC-02/05 | NET-OFFICE | -   | 30,3 | PP-02-05 > TO-L1-008-A | TO-L1-008-A > PP-02-05 | workstation FX-L1-059    |
| C-TO-L1-008-B | TO-L1-008-B | L1-IMPL   | PP-02/06 | SW-ACC-02/06 | NET-OFFICE | -   | 30,3 | PP-02-06 > TO-L1-008-B | TO-L1-008-B > PP-02-06 | phone_or_spare FX-L1-059 |
| C-TO-L1-009-A | TO-L1-009-A | L1-IMPL   | PP-02/07 | SW-ACC-02/07 | NET-OFFICE | -   | 31,5 | PP-02-07 > TO-L1-009-A | TO-L1-009-A > PP-02-07 | workstation FX-L1-061    |
| C-TO-L1-009-B | TO-L1-009-B | L1-IMPL   | PP-02/08 | SW-ACC-02/08 | NET-OFFICE | -   | 31,5 | PP-02-08 > TO-L1-009-B | TO-L1-009-B > PP-02-08 | phone_or_spare FX-L1-061 |
| C-TO-L1-010-A | TO-L1-010-A | L1-IMPL   | PP-02/09 | SW-ACC-02/09 | NET-OFFICE | -   | 28,7 | PP-02-09 > TO-L1-010-A | TO-L1-010-A > PP-02-09 | workstation FX-L1-063    |
| C-TO-L1-010-B | TO-L1-010-B | L1-IMPL   | PP-02/10 | SW-ACC-02/10 | NET-OFFICE | -   | 28,7 | PP-02-10 > TO-L1-010-B | TO-L1-010-B > PP-02-10 | phone_or_spare FX-L1-063 |
| C-TO-L1-011-A | TO-L1-011-A | L1-IMPL   | PP-02/11 | SW-ACC-02/11 | NET-OFFICE | -   | 27,5 | PP-02-11 > TO-L1-011-A | TO-L1-011-A > PP-02-11 | display FX-L1-065        |
| C-TO-L1-012-A | TO-L1-012-A | L1-NOVA   | PP-02/12 | SW-ACC-02/12 | NET-OFFICE | -   | 18,3 | PP-02-12 > TO-L1-012-A | TO-L1-012-A > PP-02-12 | workstation FX-L1-069    |
| C-TO-L1-012-B | TO-L1-012-B | L1-NOVA   | PP-02/13 | SW-ACC-02/13 | NET-OFFICE | -   | 18,3 | PP-02-13 > TO-L1-012-B | TO-L1-012-B > PP-02-13 | phone_or_spare FX-L1-069 |
| C-TO-L1-013-A | TO-L1-013-A | L1-NOVA   | PP-02/14 | SW-ACC-02/14 | NET-OFFICE | -   | 15,5 | PP-02-14 > TO-L1-013-A | TO-L1-013-A > PP-02-14 | workstation FX-L1-071    |
| C-TO-L1-013-B | TO-L1-013-B | L1-NOVA   | PP-02/15 | SW-ACC-02/15 | NET-OFFICE | -   | 15,5 | PP-02-15 > TO-L1-013-B | TO-L1-013-B > PP-02-15 | phone_or_spare FX-L1-071 |
| C-TO-L1-014-A | TO-L1-014-A | L1-LAB    | PP-02/16 | SW-ACC-02/16 | NET-LAB    | -   | 20,8 | PP-02-16 > TO-L1-014-A | TO-L1-014-A > PP-02-16 | lab_device FX-L1-075     |
| C-TO-L1-014-B | TO-L1-014-B | L1-LAB    | PP-02/17 | SW-ACC-02/17 | NET-LAB    | -   | 20,8 | PP-02-17 > TO-L1-014-B | TO-L1-014-B > PP-02-17 | lab_device FX-L1-075     |
| C-TO-L1-014-C | TO-L1-014-C | L1-LAB    | PP-02/18 | SW-ACC-02/18 | NET-LAB    | -   | 20,8 | PP-02-18 > TO-L1-014-C | TO-L1-014-C > PP-02-18 | lab_device FX-L1-075     |
| C-TO-L1-014-D | TO-L1-014-D | L1-LAB    | PP-02/19 | SW-ACC-02/19 | NET-LAB    | -   | 20,8 | PP-02-19 > TO-L1-014-D | TO-L1-014-D > PP-02-19 | lab_device FX-L1-075     |
| C-TO-L1-015-A | TO-L1-015-A | L1-LAB    | PP-02/20 | SW-ACC-02/20 | NET-LAB    | -   | 18,7 | PP-02-20 > TO-L1-015-A | TO-L1-015-A > PP-02-20 | lab_device FX-L1-076     |
| C-TO-L1-015-B | TO-L1-015-B | L1-LAB    | PP-02/21 | SW-ACC-02/21 | NET-LAB    | -   | 18,7 | PP-02-21 > TO-L1-015-B | TO-L1-015-B > PP-02-21 | lab_device FX-L1-076     |
| C-TO-L1-015-C | TO-L1-015-C | L1-LAB    | PP-02/22 | SW-ACC-02/22 | NET-LAB    | -   | 18,7 | PP-02-22 > TO-L1-015-C | TO-L1-015-C > PP-02-22 | lab_device FX-L1-076     |
| C-TO-L1-015-D | TO-L1-015-D | L1-LAB    | PP-02/23 | SW-ACC-02/23 | NET-LAB    | -   | 18,7 | PP-02-23 > TO-L1-015-D | TO-L1-015-D > PP-02-23 | lab_device FX-L1-076     |
| C-TO-L1-016-A | TO-L1-016-A | L1-LAB    | PP-02/24 | SW-ACC-02/24 | NET-LAB    | -   | 17,1 | PP-02-24 > TO-L1-016-A | TO-L1-016-A > PP-02-24 | lab_device FX-L1-077     |
| C-TO-L1-016-B | TO-L1-016-B | L1-LAB    | PP-03/01 | SW-ACC-03/01 | NET-LAB    | -   | 17,1 | PP-03-01 > TO-L1-016-B | TO-L1-016-B > PP-03-01 | lab_device FX-L1-077     |
| C-TO-L1-016-C | TO-L1-016-C | L1-LAB    | PP-03/02 | SW-ACC-03/02 | NET-LAB    | -   | 17,1 | PP-03-02 > TO-L1-016-C | TO-L1-016-C > PP-03-02 | lab_device FX-L1-077     |

Label dua ujung: sisi rack 'PP-nn-pp > port outlet', sisi outlet sebaliknya. Panjang mengikuti AS-ICT-02; batas 90 m AS-ICT-03.

STATUS KONSEP

Bukan untuk konstruksi

kantor-rpg    Proyek kantor-rpg · gedung KRPG-01

Port dan device schedule

|          |                                    |           |                               |
|----------|------------------------------------|-----------|-------------------------------|
| Skala    | NTS @ A3 lanskap                   | Revisi    | P02 · 2026-10-01              |
| Render   | 2026-10-01 12:12:53 UTC            | Halaman   | halaman 1/3                   |
| Digambar | Claude Code cloud (generator)      | Diperiksa | Max (supervisor) belum review |
| Sumber   | world.json sha256 ac39b320919d6410 |           |                               |

Nomor lembar

ICT-401

Rev P02 · 1/3

PORT SCHEDULE

rancangan virtual, bukan topologi produksi · sumber design/derived/ict-portmap.json (world P02)

| Kabel         | Port outlet | Ruang       | PP/port  | Switch/port  | Domain     | PoE | m      | Label sisi rack        | Label sisi outlet      | Endpoint                 |
|---------------|-------------|-------------|----------|--------------|------------|-----|--------|------------------------|------------------------|--------------------------|
| C-TO-L1-016-D | TO-L1-016-D | L1-LAB      | PP-03/03 | SW-ACC-03/03 | NET-LAB    | -   | 17,1   | PP-03-03 > TO-L1-016-D | TO-L1-016-D > PP-03-03 | lab_device FX-L1-077     |
| C-TO-L1-017-A | TO-L1-017-A | L1-LAB      | PP-03/04 | SW-ACC-03/04 | NET-LAB    | -   | 13,4   | PP-03-04 > TO-L1-017-A | TO-L1-017-A > PP-03-04 | lab_uplink FX-L1-079     |
| C-TO-L1-017-B | TO-L1-017-B | L1-LAB      | PP-03/05 | SW-ACC-03/05 | NET-LAB    | -   | 13,4   | PP-03-05 > TO-L1-017-B | TO-L1-017-B > PP-03-05 | spare FX-L1-079          |
| C-TO-L1-018-A | TO-L1-018-A | L1-CEO      | PP-03/06 | SW-ACC-03/06 | NET-OFFICE | -   | 39,6   | PP-03-06 > TO-L1-018-A | TO-L1-018-A > PP-03-06 | workstation FX-L1-082    |
| C-TO-L1-018-B | TO-L1-018-B | L1-CEO      | PP-03/07 | SW-ACC-03/07 | NET-OFFICE | -   | 39,6   | PP-03-07 > TO-L1-018-B | TO-L1-018-B > PP-03-07 | phone_or_spare FX-L1-082 |
| C-TO-L1-019-A | TO-L1-019-A | L1-HUGO     | PP-03/08 | SW-ACC-03/08 | NET-OFFICE | -   | 35,7   | PP-03-08 > TO-L1-019-A | TO-L1-019-A > PP-03-08 | workstation FX-L1-089    |
| C-TO-L1-019-B | TO-L1-019-B | L1-HUGO     | PP-03/09 | SW-ACC-03/09 | NET-OFFICE | -   | 35,7   | PP-03-09 > TO-L1-019-B | TO-L1-019-B > PP-03-09 | phone_or_spare FX-L1-089 |
| C-TO-L1-020-A | TO-L1-020-A | L1-HUGO     | PP-03/10 | SW-ACC-03/10 | NET-OFFICE | -   | 33,9   | PP-03-10 > TO-L1-020-A | TO-L1-020-A > PP-03-10 | workstation FX-L1-091    |
| C-TO-L1-020-B | TO-L1-020-B | L1-HUGO     | PP-03/11 | SW-ACC-03/11 | NET-OFFICE | -   | 33,9   | PP-03-11 > TO-L1-020-B | TO-L1-020-B > PP-03-11 | phone_or_spare FX-L1-091 |
| C-TO-L1-021-A | TO-L1-021-A | L1-KEVIN    | PP-03/12 | SW-ACC-03/12 | NET-OFFICE | -   | 28,3   | PP-03-12 > TO-L1-021-A | TO-L1-021-A > PP-03-12 | workstation FX-L1-096    |
| C-TO-L1-021-B | TO-L1-021-B | L1-KEVIN    | PP-03/13 | SW-ACC-03/13 | NET-OFFICE | -   | 28,3   | PP-03-13 > TO-L1-021-B | TO-L1-021-B > PP-03-13 | phone_or_spare FX-L1-096 |
| C-TO-L1-022-A | TO-L1-022-A | L1-BRUNO    | PP-03/14 | SW-ACC-03/14 | NET-OFFICE | -   | 21,9   | PP-03-14 > TO-L1-022-A | TO-L1-022-A > PP-03-14 | workstation FX-L1-101    |
| C-TO-L1-022-B | TO-L1-022-B | L1-BRUNO    | PP-03/15 | SW-ACC-03/15 | NET-OFFICE | -   | 21,9   | PP-03-15 > TO-L1-022-B | TO-L1-022-B > PP-03-15 | phone_or_spare FX-L1-101 |
| C-TO-L2-001-A | TO-L2-001-A | L2-DINE     | PP-03/16 | SW-ACC-03/16 | NET-DEMO   | -   | 42,5   | PP-03-16 > TO-L2-001-A | TO-L2-001-A > PP-03-16 | display FX-L2-034        |
| C-TO-L2-002-A | TO-L2-002-A | L2-GAME     | PP-03/17 | SW-ACC-03/17 | NET-DEMO   | -   | 24,7   | PP-03-17 > TO-L2-002-A | TO-L2-002-A > PP-03-17 | console FX-L2-058        |
| C-TO-L2-002-B | TO-L2-002-B | L2-GAME     | PP-03/18 | SW-ACC-03/18 | NET-DEMO   | -   | 24,7   | PP-03-18 > TO-L2-002-B | TO-L2-002-B > PP-03-18 | display FX-L2-058        |
| C-TO-L2-003-A | TO-L2-003-A | L2-GAME     | PP-03/19 | SW-ACC-03/19 | NET-DEMO   | -   | 19,1   | PP-03-19 > TO-L2-003-A | TO-L2-003-A > PP-03-19 | console FX-L2-061        |
| C-TO-L2-003-B | TO-L2-003-B | L2-GAME     | PP-03/20 | SW-ACC-03/20 | NET-DEMO   | -   | 19,1   | PP-03-20 > TO-L2-003-B | TO-L2-003-B > PP-03-20 | display FX-L2-061        |
| C-TO-L2-004-A | TO-L2-004-A | L2-GAME     | PP-03/21 | SW-ACC-03/21 | NET-DEMO   | -   | 24,6   | PP-03-21 > TO-L2-004-A | TO-L2-004-A > PP-03-21 | arcade FX-L2-064         |
| C-TO-L2-005-A | TO-L2-005-A | L2-GAME     | PP-03/22 | SW-ACC-03/22 | NET-DEMO   | -   | 23,7   | PP-03-22 > TO-L2-005-A | TO-L2-005-A > PP-03-22 | arcade FX-L2-065         |
| C-TO-L2-006-A | TO-L2-006-A | L2-BILLIARD | PP-03/23 | SW-ACC-03/23 | NET-DEMO   | -   | 42,2   | PP-03-23 > TO-L2-006-A | TO-L2-006-A > PP-03-23 | display FX-L2-079        |
| C-TO-L2-007-A | TO-L2-007-A | L2-CYM      | PP-03/24 | SW-ACC-03/24 | NET-DEMO   | -   | 34,2   | PP-03-24 > TO-L2-007-A | TO-L2-007-A > PP-03-24 | display FX-L2-087        |
| Total         | 72 kabel    |             |          |              |            |     | 2074,8 | port map: 2074,8 m     | COCOK                  |                          |

Label dua ujung: sisi rack 'PP-nn-pp > port outlet', sisi outlet sebaliknya. Panjang mengikuti AS-ICT-02; batas 90 m AS-ICT-03.

STATUS KONSEP

Bukan untuk konstruksi

kantor-rpg Proyek kantor-rpg · gedung KRPG-01

Port dan device schedule

|          |                                    |           |                               |
|----------|------------------------------------|-----------|-------------------------------|
| Skala    | NTS @ A3 lanskap                   | Revisi    | P02 · 2026-10-01              |
| Render   | 2026-10-01 12:12:53 UTC            | Halaman   | halaman 2/3                   |
| Digambar | Claude Code cloud (generator)      | Diperiksa | Max (supervisor) belum review |
| Sumber   | world.json sha256 ac39b320919d6410 |           |                               |

Nomor lembar

ICT-401

Rev P02 · 2/3

BOM RINGKAS DAN POE

BOM (tanpa harga): jumlah turunan dari port map; tanpa harga (AS-ICT-05)

| Item                                                    | Satuan | Jumlah |
|---------------------------------------------------------|--------|--------|
| Kabel tembaga horizontal (kategori TBD)                 | m      | 2074,8 |
| Box kabel 305 m (pembulatan, belum termasuk waste)      | box    | 7      |
| Keystone jack sisi outlet                               | pcs    | 72     |
| Faceplate 1 port                                        | pcs    | 24     |
| Faceplate 2 port                                        | pcs    | 18     |
| Faceplate 4 port                                        | pcs    | 3      |
| Patch panel 24 port                                     | pcs    | 4      |
| Patch cord sisi rack (1 per port terpakai, asumsi)      | pcs    | 72     |
| Patch cord sisi perangkat (1 per port terpakai, asumsi) | pcs    | 72     |
| Access switch 48 port PoE (kelas, model TBD)            | pcs    | 3      |
| Access point (placeholder AS-ICT-01)                    | pcs    | 11     |
| Kamera konsep (opsional)                                | pcs    | 5      |
| Rack 42U (target)                                       | pcs    | 2      |
| UPS (rating TBD)                                        | pcs    | 1      |

Harga: tidak ada (tidak ada quote bertanggal; tidak diestimasi; AS-ICT-05).

POE PER SWITCH (BELUM DIVALIDASI)

| Switch    | Port  | Spare | Worst W | Budget W  | Status                                           |
|-----------|-------|-------|---------|-----------|--------------------------------------------------|
| SW-ACC-01 | 24/48 | 20    | 407     | belum ada | belum divalidasi: datasheet switch belum dipilih |
| SW-ACC-02 | 24/48 | 20    | 0       | belum ada | belum divalidasi: datasheet switch belum dipilih |
| SW-ACC-03 | 24/48 | 20    | 0       | belum ada | belum divalidasi: datasheet switch belum dipilih |

Total PoE worst-case 407 W dari nilai PSE kelas IEEE (AS-ICT-04): belum divalidasi karena datasheet switch belum dipilih.

TOTAL

|                        |                                                |
|------------------------|------------------------------------------------|
| Outlet / port          | 45 / 72                                        |
| Panjang kabel          | 2074,8 m (baris) vs 2074,8 m (port map): COCOK |
| Terpanjang / terpendek | 50,6 / 12,7 m                                  |
| Revisi data            | port map P02 / world P02: sama                 |

STATUS KONSEP

Bukan untuk konstruksi

kantor-rpg    Proyek kantor-rpg - gedung KRPG-01

Port dan device schedule

|          |                                    |           |                               |
|----------|------------------------------------|-----------|-------------------------------|
| Skala    | NTS @ A3 lanskap                   | Revisi    | P02 - 2026-10-01              |
| Render   | 2026-10-01 12:12:53 UTC            | Halaman   | halaman 3/3                   |
| Digambar | Claude Code cloud (generator)      | Diperiksa | Max (supervisor) belum review |
| Sumber   | world.json sha256 ac39b320919d6410 |           |                               |

Nomor lembar

ICT-401

Rev P02 · 3/3