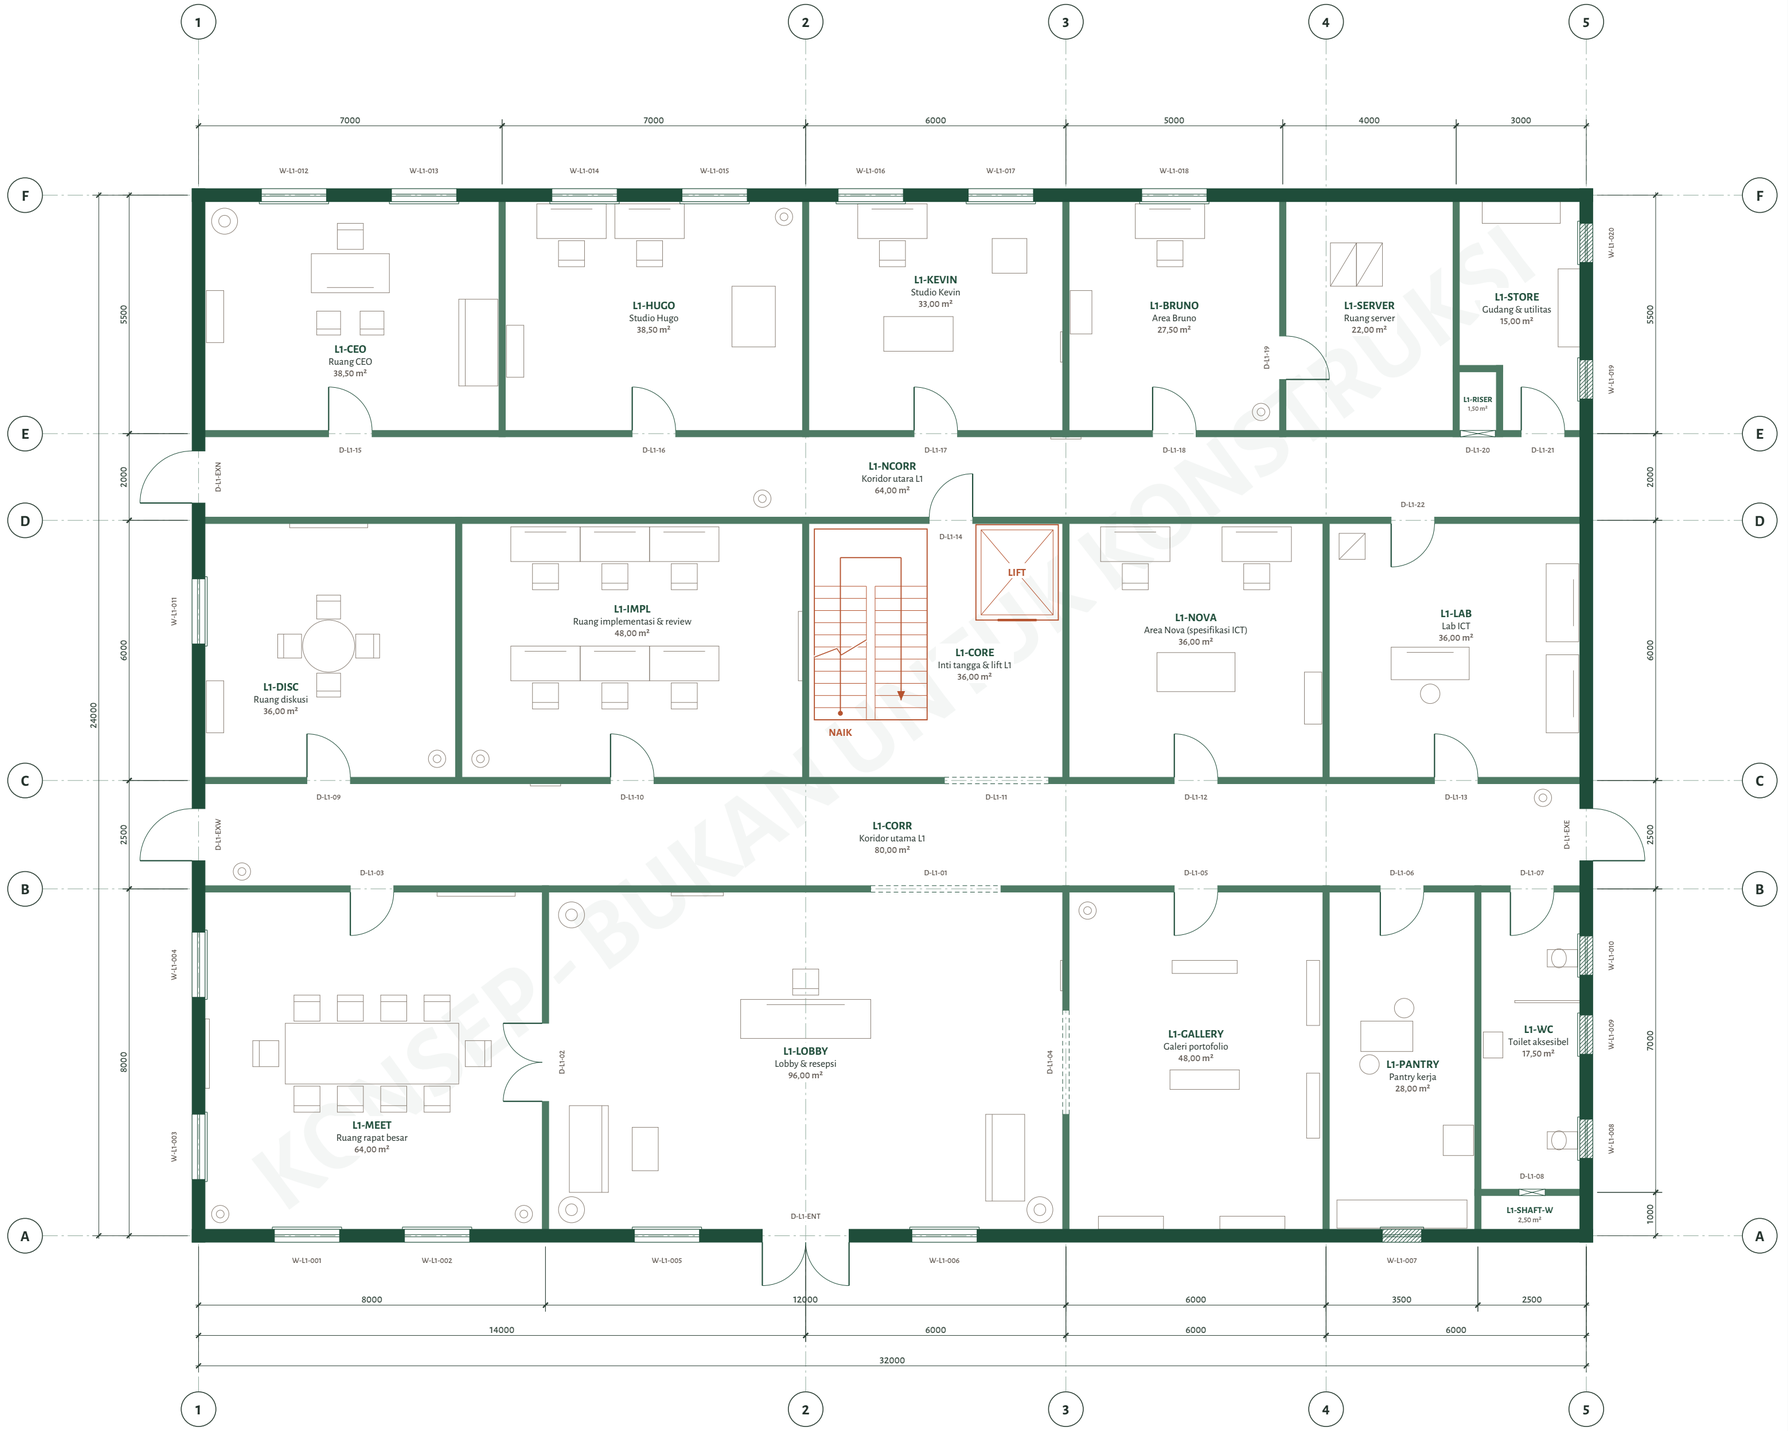


KONSEP - BUKAN UNTUK KONSTRUKSI

DENAH LANTAI 1

Skala 1:100 @ A2 · lantai L1 · ukuran dalam mm, as ke as dinding

0 1 2 5 10 m

Skala grafis benar pada cetak A2 100%: 10 m = 100 mm di kertas

U

Utara = sumbu Y+ dunia
Origin (0,0) sudut barat daya L1, X timur.
Grid acuan konsep dari tepi ruang (1..n, A..n), bukan grid struktur (AS-DIM-03).

LEGENDA

- Dinding luar 0,30 m (poche hijau tua)
- Dinding dalam 0,15 m
- Pintu tunggal + arah buka 90°
- Pintu ganda
- Bukaan tanpa daun (garis atas putus)
- Hatch akses shaft / riser
- Furniture dan fixture (catalog, AS-DIM-04)
- Tangga U / lift, panah dari lantai ini
- 1 Garis grid acuan konsep
- 8000 Dimensi mm, as ke as (AS-DIM-02)
- ID-RUANG 00,00 m² Tag ruang: ID, nama, luas as-drawn
- D-ID ID pintu (sisi tanpa ayunan)
- Jendela konsep kaca bening, ID di luar dinding
- Jendela kaca buram (arsir diagonal)

ASUMSI (lengkap di design/world.json dan docs/assumptions.md)

AS-DIM-01	Footprint 32 x 24 m dan tinggi antar lantai 4,0 m adalah proposal PRD, bukan lahan yang disahkan.
AS-DIM-02	Polygon ruang diukur di as dinding; luas = luas as-drawn, bukan luas bersih.
AS-DIM-03	Tebal dinding konsep luar 0,30 m, dalam 0,15 m; plafon 3,0 m; belum ada desain struktur.
AS-DIM-04	Ukuran furniture dari catalog adalah target konsep, bukan katalog vendor.
AS-DIM-05	Tangga U 24 riser x 0,1667 m, tread 0,28 m, lebar flight 1,2 m: target konsep, bukan tangga layak konstruksi.
AS-OCC-02	Kapasitas kursi dihitung dari fixture, bukan target okupansi yang diputuskan.

DAFTAR RUANG L1 (luas as-drawn dari polygon)

ID	Nama	Luas
L1-MEET	Ruang rapat besar	64,00 m²
L1-LOBBY	Lobby & resepsi	96,00 m²
L1-GALLERY	Galeri portofolio	48,00 m²
L1-PANTRY	Pantry kerja	28,00 m²
L1-SHAFT-W	Shaft basah	2,50 m²
L1-WC	Toilet aksesibel	17,50 m²
L1-CORR	Koridor utama L1	80,00 m²
L1-DISC	Ruang diskusi	36,00 m²
L1-IMPL	Ruang implementasi & review	48,00 m²
L1-CORE	Inti tangga & lift L1	36,00 m²
L1-NOVA	Area Nova (spesifikasi ICT)	36,00 m²
L1-LAB	Lab ICT	36,00 m²
L1-NCORR	Koridor utama L1	64,00 m²
L1-CEO	Ruang CEO	38,50 m²
L1-HUGO	Studio Hugo	38,50 m²
L1-KEVIN	Studio Kevin	33,00 m²
L1-BRUNO	Area Bruno	27,50 m²
L1-SERVER	Ruang server	22,00 m²
L1-RISER	Riser ICT	1,50 m²
L1-STORE	Gudang & utilitas	15,00 m²
Jumlah 20 ruang	= envelope 32 x 24 m (768,00 m²)	**768,00 m²**

CATATAN

- Sumber tunggal: design/world.json revisi P03; dinding diturunkan oleh tools/kantor/geometry.py (tepi polygon ruang dikurangi bukaan pintu).
- Arah buka dan sisi engsel pintu dibaca dari world.json (doors[].swing.into dan .hinge); generator menolak pintu tunggal/ganda tanpa data swing.
- Jendela konsep dari world.json windows: 20 di lantai ini, 6 kaca buram. Ambang dan kepala jendela ada di schedule pintu dan jendela A-103 halaman 2 dan di A-301.
- Lantai L1: elevasi ±0,00 m; 20 ruang, 26 pintu/bukaan, 108 fixture, 41 slot duduk (AS-OCC-02).
- DXF pasangan: cad/out/A-101.dxf (mm, 1:1). DWG native BLOCKED: tidak ada AutoCAD berlisensi di container; lihat cad/AUTOCAD-RUNBOOK.md.
- Pintu exit konsep di lantai ini: 4. Jalur keluar belum dinilai terhadap peraturan (AS-OCC-01).

KUNCI LANTAI

L2	elevasi +4,00 m	Lantai 2 - Rekreasi
L1	elevasi ±0,00 m	**Lantai 1 - Kerja & Kunjungan (lembar ini)**

RIWAYAT REVISI

Rev	Tanggal	Keterangan
P03	2026-10-01	Hardening: arah bukaan pintu dan jendela konsep di dataset; gym provisional (Q-03). Lembar dihasilkan dari world.json revisi ini.

kantor-rpg Proyek kantor-rpg · gedung KRPG-01

STATUS KONSEP — Bukan untuk konstruksi

Denah Lantai 1

L1: Lantai 1 - Kerja & Kunjungan

Skala	1:100 @ A2 lanskap
Revisi	P03 · 2026-10-01
Render	2026-10-01 15:47:39 UTC
Satuan	mm (dimensi), m² (luas)
Digambar	Claude Code cloud (generator)
Diperiksa	Max (supervisor) belum review
Sumber	world.json sha256 488597bb0552fbde
Generator	cad/generate.py v1

Nomor lembar

A-101

Rev P03

Huruf: KantorRPG Sans, turunan Alegreya Sans karya Juan Pablo del Peral (SIL OFL 1.1, paket Debian fonts-alegreya-sans), subset tertanam.