


TOPOLOGI JARINGAN (VIRTUAL)

RANCANGAN VIRTUAL, BUKAN TOPOLOGI PRODUKSI

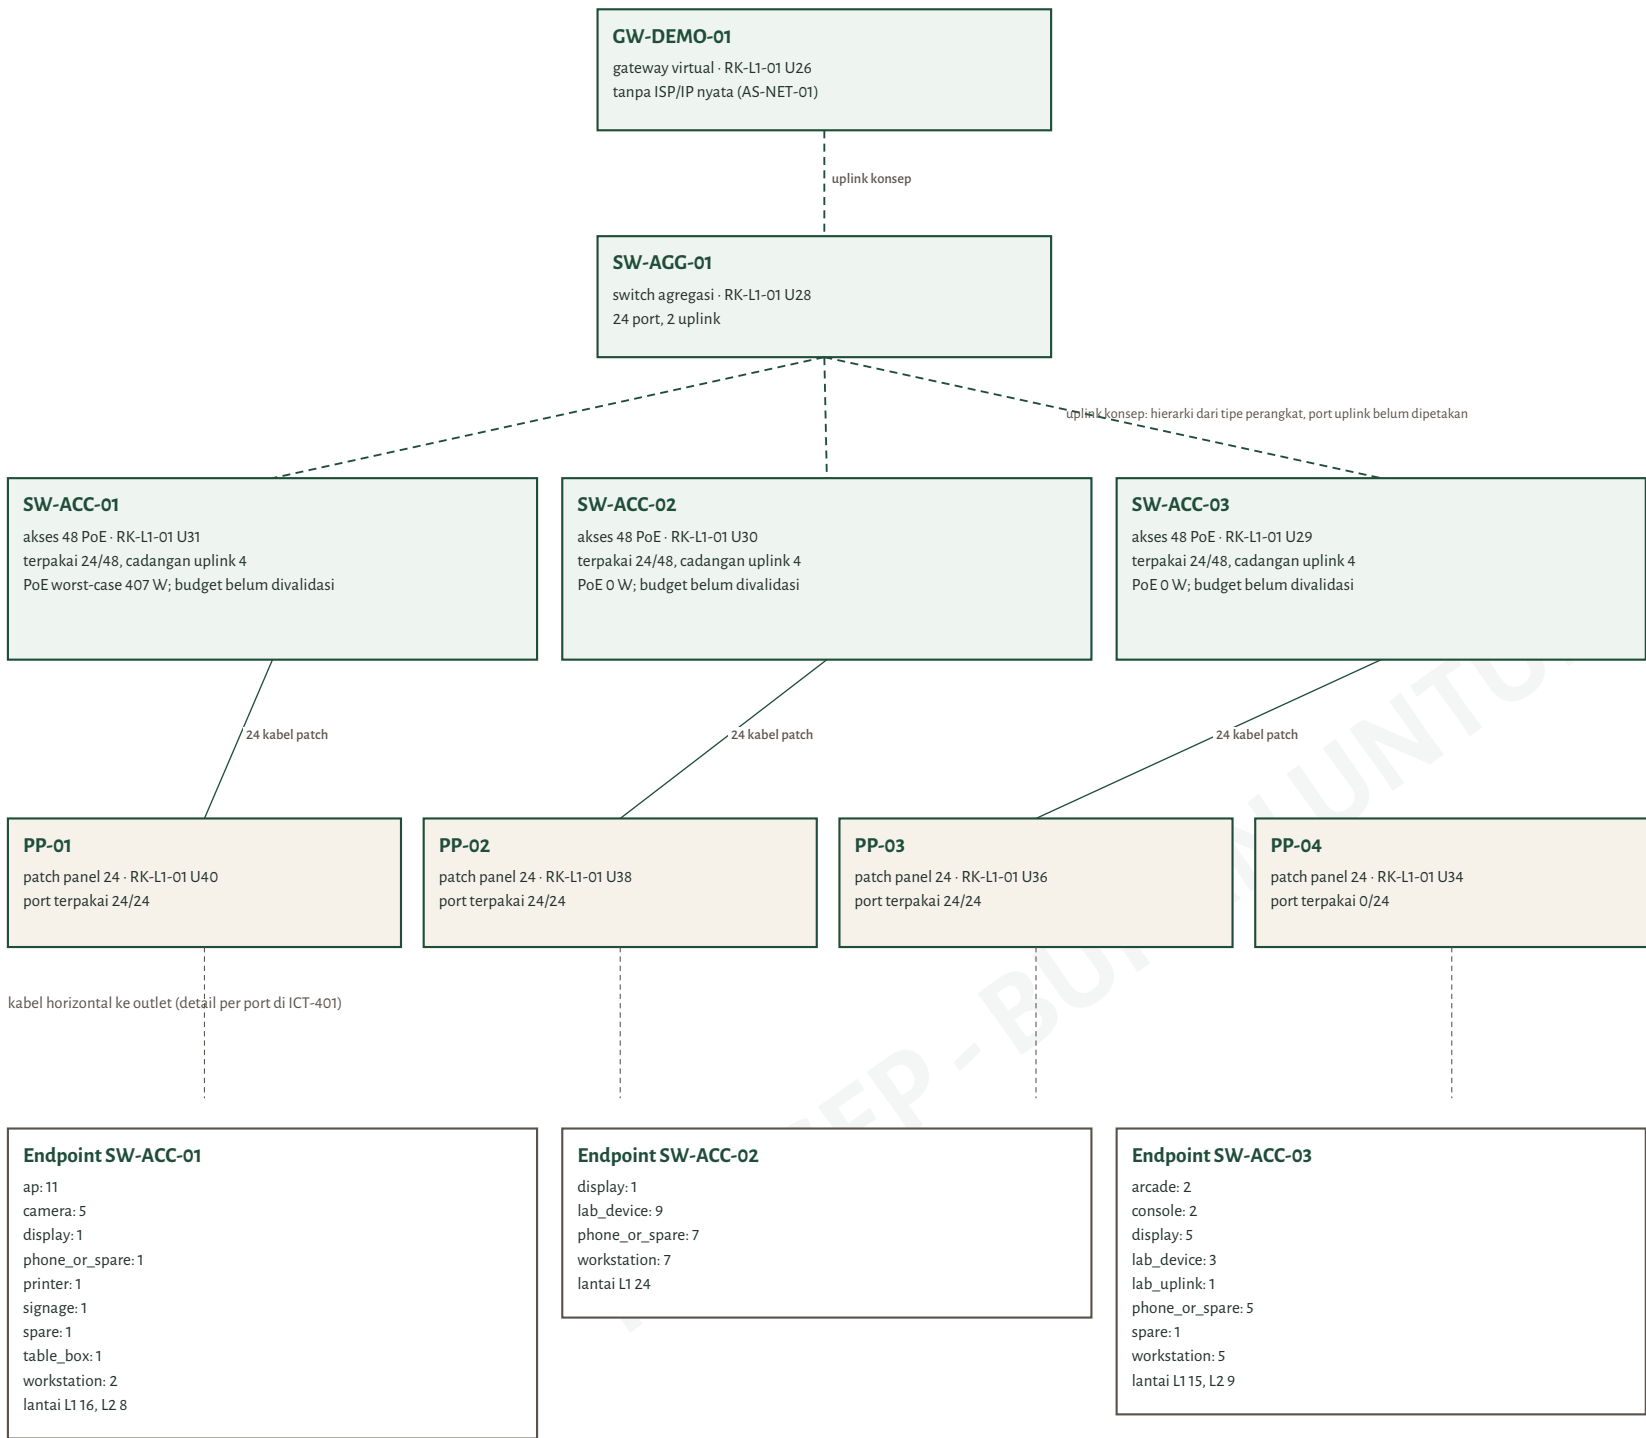

DOMAIN (ID abstrak, AS-NET-01)

Domain	Label	Port	Catatan
NET-OFFICE	office	48	abstrak
NET-DEMO	demo	10	abstrak
NET-GUEST	guest	0	abstrak, SSID tamu konsep
NET-LAB	lab	14	abstrak, terisolasi konsep
NET-SERVER	server	0	abstrak

JUMLAH DARI DATA

Outlet	45 outlet, 72 port
Patch panel	4 x 24 = 96 port, terpakai 72
Access point	11 placeholder (AS-ICT-01): L1 5, L2 6
Kamera	5 opsional konsep: L1 3, L2 2
Kabel	72 kabel, total 2074,8 m (AS-ICT-02)
PoE	worst-case 407 W dari kelas IEEE (AS-ICT-04); belum divalidasi

RACK

RK-L1-01	L1-SERVER, 42U: PP-01 U40, CM-01 U39, PP-02 U38, CM-02 U37, PP-03 U36, CM-03 U35, PP-04 U34, CM-04 U33, SW-ACC-01 U31, SW-ACC-02 U30, SW-ACC-03 U29, SW-AGG-01 U28, GW-DEMO-01 U26
RK-L1-02	L1-SERVER, 42U: SRV-DEMO-01 U20, NAS-DEMO-01 U17, PDU-01 U10, UPS-01 U1

SRV-DEMO-01 dan NAS-DEMO-01 belum punya port map; koneksinya tidak digambar.

STATUS KONSEP

Bukan untuk konstruksi

kantor-rpg Proyek kantor-rpg - gedung KRPG-01

Topologi jaringan (virtual)

Skala	NTS @ A3 lanskap	Revisi	P03 - 2026-10-01
Render	2026-10-01 15:47:39 UTC	Halaman	halaman 1/1
Digambar	Claude Code cloud (generator)	Diperiksa	Max (supervisor) belum review
Sumber	world.json sha256 488597bb0552fbde		

Nomor lembar

ICT-001

Rev P03 · 1/1

OUTLET, AP DAN KAMERA LANTAI 1

Skala 1:100 @ A2

Label outlet: ID (jumlah port), Tray di +3,2 m (AS-ICT-02), AP placeholder tanpa klaim radius Wi-Fi (AS-ICT-01).



Rancangan virtual, bukan topologi produksi

Lantai L1: Lantai 1 - Kerja & Kunjungan

Sumber: world.json ict + design/derived/ict-portmap.json

LEGENDA

- △ Outlet data (segitiga), label ID (port) ○ Access point placeholder (AS-ICT-01)
- Kamera opsional + arah konsep (bukan FOV terukur) — Tray kabel +3,2 m
- Riservertikal ke lantai lain ■ Rack 42U (target)

OUTLET L1 (30 outlet, 55 port)

ID	Ruang	Port	Domain	Melayani	ID	Ruang	Port	Domain	Melayani
TO-L1-001	LOBBY	2	OFFICE	FX-L1-001	TO-L1-016	LAB	4	LAB	FX-L1-077
TO-L1-002	LOBBY	1	DEMO	FX-L1-009	TO-L1-017	LAB	2	LAB	FX-L1-079
TO-L1-003	MEET	2	OFFICE	FX-L1-011	TO-L1-018	CEO	2	OFFICE	FX-L1-082
TO-L1-004	MEET	1	OFFICE	FX-L1-022	TO-L1-019	HUGO	2	OFFICE	FX-L1-089
TO-L1-005	IMPL	2	OFFICE	FX-L1-053	TO-L1-020	HUGO	2	OFFICE	FX-L1-091
TO-L1-006	IMPL	2	OFFICE	FX-L1-055	TO-L1-021	KEVIN	2	OFFICE	FX-L1-096
TO-L1-007	IMPL	2	OFFICE	FX-L1-057	TO-L1-022	BRUNO	2	OFFICE	FX-L1-101
TO-L1-008	IMPL	2	OFFICE	FX-L1-059	TO-L1-023	LOBBY	1	OFFICE	AP-L1-01
TO-L1-009	IMPL	2	OFFICE	FX-L1-061	TO-L1-024	IMPL	1	OFFICE	AP-L1-02
TO-L1-010	IMPL	2	OFFICE	FX-L1-063	TO-L1-025	CORR	1	OFFICE	AP-L1-03
TO-L1-011	IMPL	1	OFFICE	FX-L1-065	TO-L1-026	NCORR	1	OFFICE	AP-L1-04
TO-L1-012	NOVA	2	OFFICE	FX-L1-069	TO-L1-027	NCORR	1	OFFICE	AP-L1-05
TO-L1-013	NOVA	2	OFFICE	FX-L1-071	TO-L1-028	LOBBY	1	OFFICE	CAM-L1-01
TO-L1-014	LAB	4	LAB	FX-L1-075	TO-L1-029	CORR	1	OFFICE	CAM-L1-02
TO-L1-015	LAB	4	LAB	FX-L1-076	TO-L1-030	BRUNO	1	OFFICE	CAM-L1-03

PERANGKAT L1 (AP 5, kamera 3)

ID	Ruang	Outlet	Tinggi	PoE	Status
AP-L1-01	LOBBY	TO-L1-023	3,0 m	4	placeholder (AS-ICT-01)
AP-L1-02	IMPL	TO-L1-024	3,0 m	4	placeholder (AS-ICT-01)
AP-L1-03	CORR	TO-L1-025	3,0 m	4	placeholder (AS-ICT-01)
AP-L1-04	NCORR	TO-L1-026	3,0 m	4	placeholder (AS-ICT-01)
AP-L1-05	NCORR	TO-L1-027	3,0 m	4	placeholder (AS-ICT-01)
CAM-L1-01	LOBBY	TO-L1-028	2,8 m	3	opsional konsep, privacy mask perlu kajian
CAM-L1-02	CORR	TO-L1-029	2,8 m	3	opsional konsep, privacy mask perlu kajian
CAM-L1-03	BRUNO	TO-L1-030	2,8 m	3	opsional konsep, privacy mask perlu kajian

ASUMSI

- AS-ICT-01** Jumlah AP adalah placeholder; belum ada model site/material dan target coverage. Tidak ada radius Wi-Fi efektif yang diklaim.
- AS-ICT-02** Slack kabel: 3,0 m sisi rack + 0,3 m sisi outlet; tray pada 3,2 m di atas lantai jadi; outlet meja 0,3 m; outlet plafon 3,0 m. Asumsi proyek, bukan standar.
- AS-ICT-03** Batas panjang permanent link 90 m dipakai sebagai target konsep (praktik umum kabel tembaga terstruktur), wajib diverifikasi ke standar yang dipilih.
- AS-NET-01** Domain jaringan office/demo/guest/lab/server adalah ID abstrak; bukan subnet, VLAN atau perangkat produksi.

STATUS KONSEP

Bukan untuk konstruksi

kantor-rpg
Outlet, AP dan kamera Lantai 1

Skala	1:100 @ A2 lanskap	Revisi	P03 - 2026-10-01
Render	2026-10-01 15:47:39 UTC	Halaman	halaman 1/1
Digambar	Claude Code cloud (generator)	Diperiksa	Max (supervisor) belum review
Sumber	world.json sha256 488597bb0552fbde		

Nomor lembar

ICT-101

Rev P03 - 1/1

OUTLET, AP DAN KAMERA LANTAI 2

Skala 1:100 @ A2

Label outlet: ID (jumlah port), Tray di +3,2 m (AS-ICT-02), AP placeholder tanpa klaim radius Wi-Fi (AS-ICT-01).



Rancangan virtual, bukan topologi produksi

Lantai L2: Lantai 2 - Rekreasi

Sumber: world.json ict + design/derived/ict-portmap.json

LEGENDA

- △ Outlet data (segitiga), label ID (port)

□ Kamera opsional + arah konsep (bukan FOV terukur)

■ Riservertikal ke lantai lain
- Access point placeholder (AS-ICT-01)

— Tray kabel +3,2 m

■ Rack 42U (target)

OUTLET L2 (15 outlet, 17 port)

ID	Ruang	Port	Domain	Melayani	ID	Ruang	Port	Domain	Melayani
TO-L2-001	DINE	1	DEMO	FX-L2-034	TO-L2-009	DINE	1	OFFICE	AP-L2-02
TO-L2-002	GAME	2	DEMO	FX-L2-058	TO-L2-010	GAME	1	OFFICE	AP-L2-03
TO-L2-003	GAME	2	DEMO	FX-L2-061	TO-L2-011	CORR	1	OFFICE	AP-L2-04
TO-L2-004	GAME	1	DEMO	FX-L2-064	TO-L2-012	NCORR	1	OFFICE	AP-L2-05
TO-L2-005	GAME	1	DEMO	FX-L2-065	TO-L2-013	GYM	1	OFFICE	AP-L2-06
TO-L2-006	BILLIARD	1	DEMO	FX-L2-079	TO-L2-014	CORR	1	OFFICE	CAM-L2-01
TO-L2-007	GYM	1	DEMO	FX-L2-087	TO-L2-015	NCORR	1	OFFICE	CAM-L2-02
TO-L2-008	LOUNGE	1	OFFICE	AP-L2-01					

PERANGKAT L2 (AP 6, kamera 2)

ID	Ruang	Outlet	Tinggi	PoE	Status
AP-L2-01	LOUNGE	TO-L2-008	3,0 m	4	placeholder (AS-ICT-01)
AP-L2-02	DINE	TO-L2-009	3,0 m	4	placeholder (AS-ICT-01)
AP-L2-03	GAME	TO-L2-010	3,0 m	4	placeholder (AS-ICT-01)
AP-L2-04	CORR	TO-L2-011	3,0 m	4	placeholder (AS-ICT-01)
AP-L2-05	NCORR	TO-L2-012	3,0 m	4	placeholder (AS-ICT-01)
AP-L2-06	GYM	TO-L2-013	3,0 m	4	placeholder (AS-ICT-01)
CAM-L2-01	CORR	TO-L2-014	2,8 m	3	opsional konsep, privacy mask perlu kajian
CAM-L2-02	NCORR	TO-L2-015	2,8 m	3	opsional konsep, privacy mask perlu kajian

ASUMSI

- AS-ICT-01** Jumlah AP adalah placeholder; belum ada model site/material dan target coverage. Tidak ada radius Wi-Fi efektif yang diklaim.
- AS-ICT-02** Slack kabel: 3,0 m sisi rack + 0,3 m sisi outlet; tray pada 3,2 m di atas lantai jadi; outlet meja 0,3 m; outlet plafon 3,0 m. Asumsi proyek, bukan standar.
- AS-ICT-03** Batas panjang permanent link 90 m dipakai sebagai target konsep (praktik umum kabel tembaga terstruktur), wajib diverifikasi ke standar yang dipilih.
- AS-NET-01** Domain jaringan office/demo/guest/lab/server adalah ID abstrak; bukan subnet, VLAN atau perangkat produksi.

STATUS KONSEP

Bukan untuk konstruksi

kantor-rpg
Outlet, AP dan kamera Lantai 2


Skala	1:100 @ A2 lanskap	Revisi	P03 - 2026-10-01
Render	2026-10-01 15:47:39 UTC	Halaman	halaman 1/1
Digambar	Claude Code cloud (generator)	Diperiksa	Max (supervisor) belum review
Sumber	world.json sha256 488597bb0552fbde		

Nomor lembar


ICT-102

Rev P03 - 1/1


RK-L1-01 TAMPAK DEPAN 1:20 · L1-SERVER · 42U

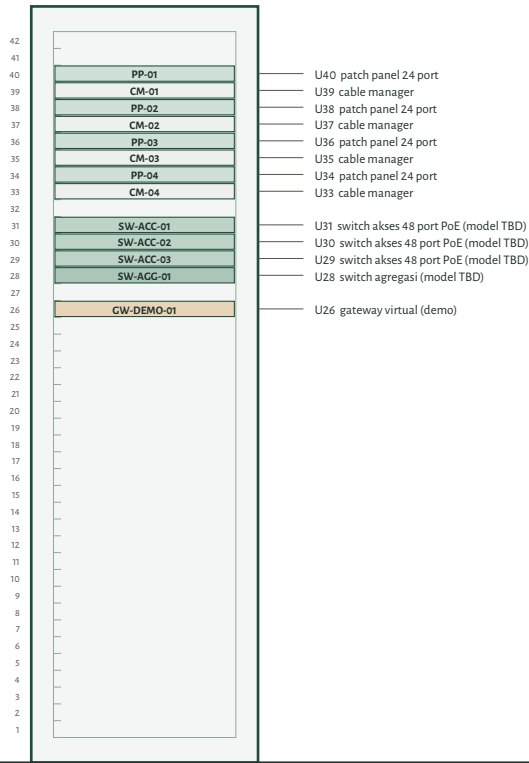

RK-L1-02 TAMPAK DEPAN 1:20 · L1-SERVER · 42U

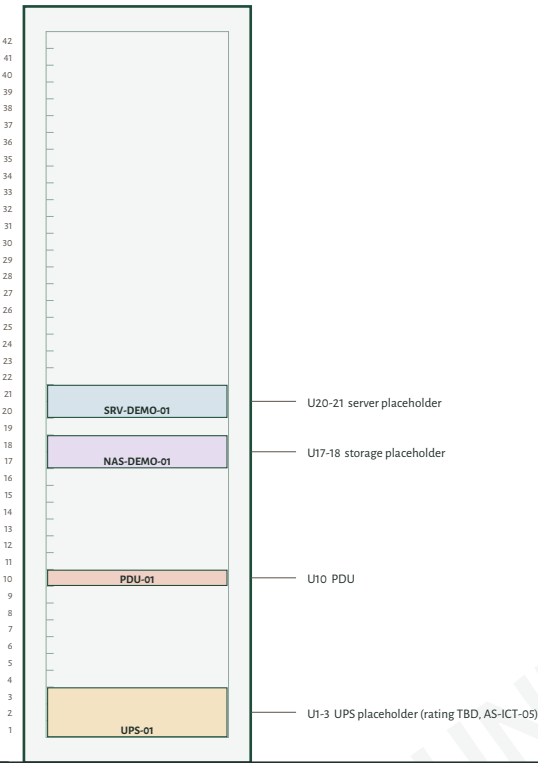

CLEARANCE RACK 1:100 (AS-ICT-06)

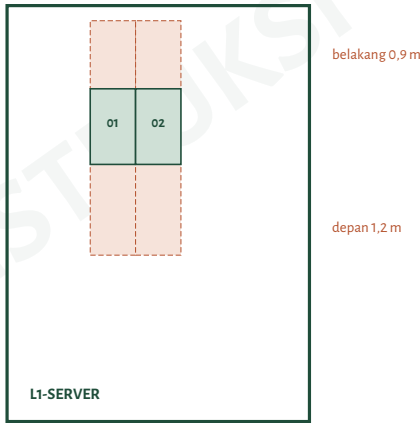

ISI RACK (world.json racks[].contents)

Rack	U	Tinggi	Perangkat	Tipe	Port
RK-L1-01	U40	1	PP-01	patch panel 24 port	24
RK-L1-01	U39	1	CM-01	cable manager	-
RK-L1-01	U38	1	PP-02	patch panel 24 port	24
RK-L1-01	U37	1	CM-02	cable manager	-
RK-L1-01	U36	1	PP-03	patch panel 24 port	24
RK-L1-01	U35	1	CM-03	cable manager	-
RK-L1-01	U34	1	PP-04	patch panel 24 port	24
RK-L1-01	U33	1	CM-04	cable manager	-
RK-L1-01	U31	1	SW-ACC-01	switch akses 48 port PoE (model TBD)	48
RK-L1-01	U30	1	SW-ACC-02	switch akses 48 port PoE (model TBD)	48
RK-L1-01	U29	1	SW-ACC-03	switch akses 48 port PoE (model TBD)	48
RK-L1-01	U28	1	SW-AGG-01	switch agregasi (model TBD)	24
RK-L1-01	U26	1	GW-DEMO-01	gateway virtual (demo)	8
RK-L1-02	U20	2	SRV-DEMO-01	server placeholder	2
RK-L1-02	U17	2	NAS-DEMO-01	storage placeholder	2
RK-L1-02	U10	1	PDU-01	PDU	-
RK-L1-02	U1	3	UPS-01	UPS placeholder (rating TBD, AS-ICT-05)	-

- Skala tampak rack 1:20; 1U = 44,45 mm, nomor U dihitung dari bawah.
- Model switch, PDU dan UPS belum dipilih (AS-ICT-04, AS-ICT-05); tidak ada harga.
- Clearance depan 1,2 m / belakang 0,9 m adalah target konsep dari catalog (AS-ICT-06), wajib diverifikasi ke standar yang dipilih.

STATUS KONSEP

Bukan untuk konstruksi

kantor-rpg Proyek kantor-rpg · gedung KRPG-01

Elevasi rack


Skala	1:20 @ A3 lanskap	Revisi	P03 · 2026-10-01
Render	2026-10-01 15:47:39 UTC	Halaman	halaman 1/1
Digambar	Claude Code cloud (generator)	Diperiksa	Max (supervisor) belum review
Sumber	world.json sha256 488597bb0552fbde		

Nomor lembar


ICT-201

Rev P03 · 1/1

JALUR KABEL L1 1:200 - tray +3,2 m

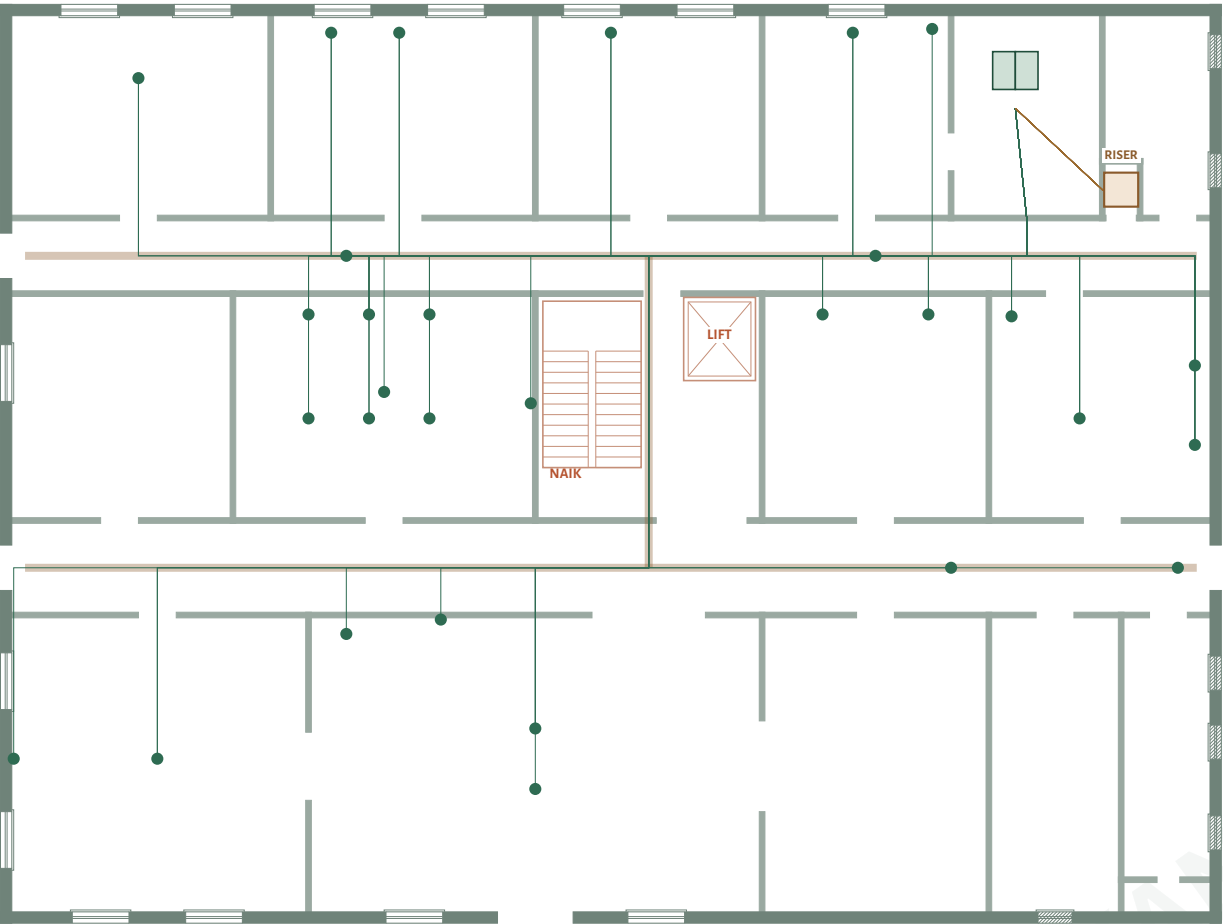

JALUR KABEL L2 1:200 - tray +3,2 m

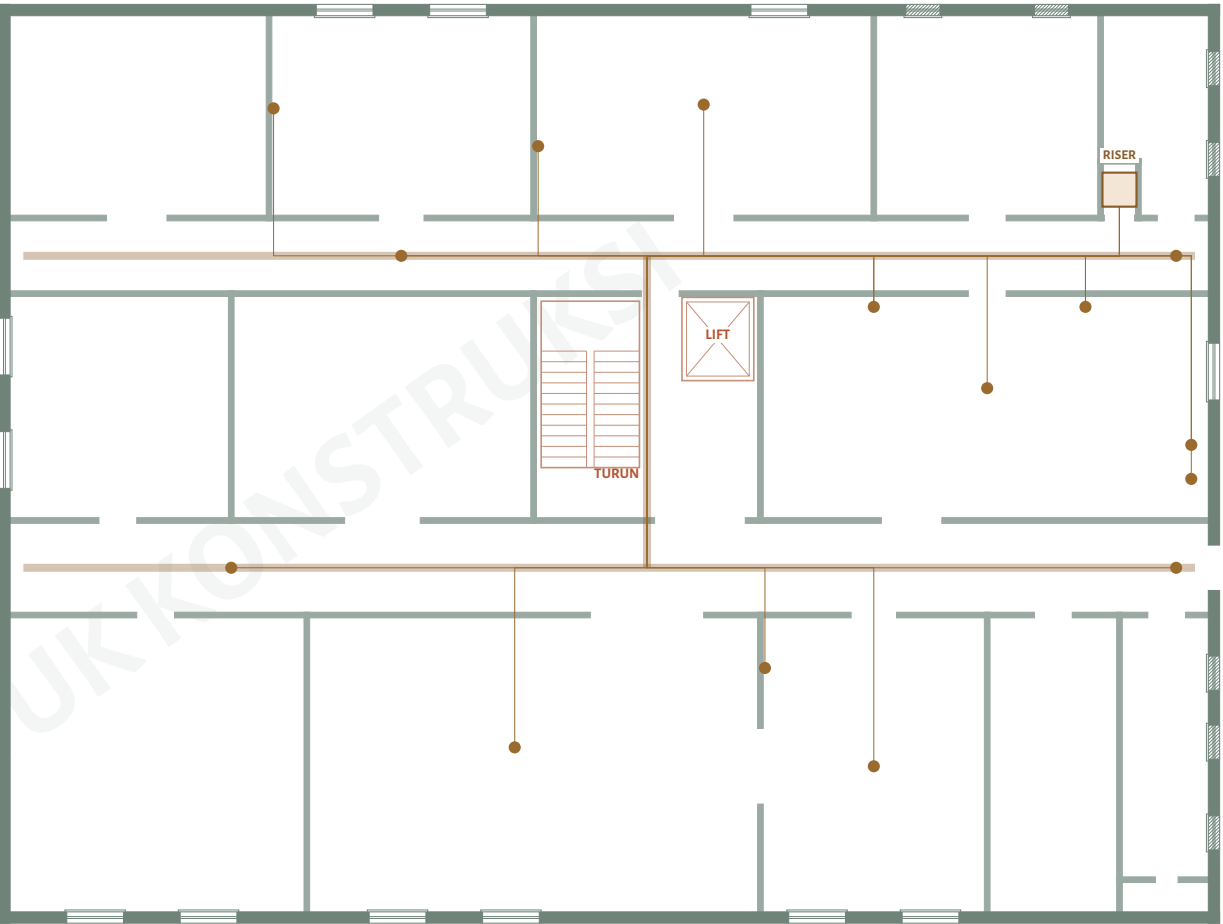


RINGKASAN PANJANG KABEL (ict-portmap.json)

Lantai	Kabel	Total m	Min m	Maks m	Rata m
L1	55	1537,1	12,7	50,6	27,9
L2	17	537,7	15,6	48,9	31,6
Total	72	2074,8	12,7	50,6	28,8

Cek: jumlah baris 2074,8 m vs total port map 2074,8 m: COCOK. Semua kabel di bawah target 90 m (AS-ICT-03).

SKEMA RISER

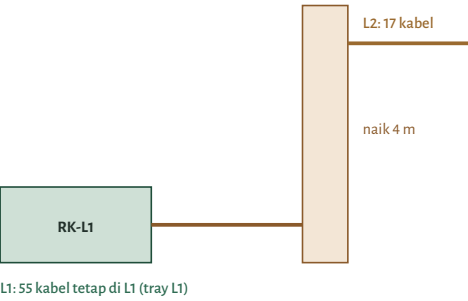

- Garis hijau = kabel endpoint L1, coklat = kabel endpoint L2 (bagian di L1 ikut warna lantai tujuan).
- Panjang = route tray + naik rack 1,2 m + riser 4,0 m (L2) + drop + slack 3,3 m (AS-ICT-02).



STATUS KONSEP

Bukan untuk konstruksi

kantor-rpg Proyek kantor-rpg - gedung KRPG-01
Pathway dan riser

Skala 1:200 @ A3 lanskap
Render 2026-10-01 15:47:39 UTC
Digambar Claude Code cloud (generator)
Sumber world.json sha256 488597bb0552fbde

Revisi P03 - 2026-10-01
Halaman halaman 1/1
Diperiksa Max (supervisor) belum review

Nomor lembar

ICT-301

Rev P03 · 1/1

PORT SCHEDULE

rancangan virtual, bukan topologi produksi · sumber design/derived/ict-portmap.json (world P03)

Kabel	Port outlet	Ruang	PP/port	Switch/port	Domain	PoE	m	Label sisi rack	Label sisi outlet	Endpoint
C-TO-L1-023-A	TO-L1-023-A	L1-LOBBY	PP-01/01	SW-ACC-01/01	NET-OFFICE	4	35,8	PP-01-01 > TO-L1-023-A	TO-L1-023-A > PP-01-01	ap AP-L1-01
C-TO-L1-024-A	TO-L1-024-A	L1-IMPL	PP-01/02	SW-ACC-01/02	NET-OFFICE	4	29,3	PP-01-02 > TO-L1-024-A	TO-L1-024-A > PP-01-02	ap AP-L1-02
C-TO-L1-025-A	TO-L1-025-A	L1-CORR	PP-01/03	SW-ACC-01/03	NET-OFFICE	4	34,9	PP-01-03 > TO-L1-025-A	TO-L1-025-A > PP-01-03	ap AP-L1-03
C-TO-L1-026-A	TO-L1-026-A	L1-NCORR	PP-01/04	SW-ACC-01/04	NET-OFFICE	4	26,7	PP-01-04 > TO-L1-026-A	TO-L1-026-A > PP-01-04	ap AP-L1-04
C-TO-L1-027-A	TO-L1-027-A	L1-NCORR	PP-01/05	SW-ACC-01/05	NET-OFFICE	4	12,7	PP-01-05 > TO-L1-027-A	TO-L1-027-A > PP-01-05	ap AP-L1-05
C-TO-L1-028-A	TO-L1-028-A	L1-LOBBY	PP-01/06	SW-ACC-01/06	NET-OFFICE	3	36,7	PP-01-06 > TO-L1-028-A	TO-L1-028-A > PP-01-06	camera CAM-L1-01
C-TO-L1-029-A	TO-L1-029-A	L1-CORR	PP-01/07	SW-ACC-01/07	NET-OFFICE	3	40,9	PP-01-07 > TO-L1-029-A	TO-L1-029-A > PP-01-07	camera CAM-L1-02
C-TO-L1-030-A	TO-L1-030-A	L1-BRUNO	PP-01/08	SW-ACC-01/08	NET-OFFICE	3	17,2	PP-01-08 > TO-L1-030-A	TO-L1-030-A > PP-01-08	camera CAM-L1-03
C-TO-L2-008-A	TO-L2-008-A	L2-LOUNGE	PP-01/09	SW-ACC-01/09	NET-OFFICE	4	43,1	PP-01-09 > TO-L2-008-A	TO-L2-008-A > PP-01-09	ap AP-L2-01
C-TO-L2-009-A	TO-L2-009-A	L2-DINE	PP-01/10	SW-ACC-01/10	NET-OFFICE	4	46,1	PP-01-10 > TO-L2-009-A	TO-L2-009-A > PP-01-10	ap AP-L2-02
C-TO-L2-010-A	TO-L2-010-A	L2-GAME	PP-01/11	SW-ACC-01/11	NET-OFFICE	4	21,1	PP-01-11 > TO-L2-010-A	TO-L2-010-A > PP-01-11	ap AP-L2-03
C-TO-L2-011-A	TO-L2-011-A	L2-CORR	PP-01/12	SW-ACC-01/12	NET-OFFICE	4	45,9	PP-01-12 > TO-L2-011-A	TO-L2-011-A > PP-01-12	ap AP-L2-04
C-TO-L2-012-A	TO-L2-012-A	L2-NCORR	PP-01/13	SW-ACC-01/13	NET-OFFICE	4	33,1	PP-01-13 > TO-L2-012-A	TO-L2-012-A > PP-01-13	ap AP-L2-05
C-TO-L2-013-A	TO-L2-013-A	L2-GYM	PP-01/14	SW-ACC-01/14	NET-OFFICE	4	29,1	PP-01-14 > TO-L2-013-A	TO-L2-013-A > PP-01-14	ap AP-L2-06
C-TO-L2-014-A	TO-L2-014-A	L2-CORR	PP-01/15	SW-ACC-01/15	NET-OFFICE	3	48,9	PP-01-15 > TO-L2-014-A	TO-L2-014-A > PP-01-15	camera CAM-L2-01
C-TO-L2-015-A	TO-L2-015-A	L2-NCORR	PP-01/16	SW-ACC-01/16	NET-OFFICE	3	15,6	PP-01-16 > TO-L2-015-A	TO-L2-015-A > PP-01-16	camera CAM-L2-02
C-TO-L1-001-A	TO-L1-001-A	L1-LOBBY	PP-01/17	SW-ACC-01/17	NET-OFFICE	-	36,9	PP-01-17 > TO-L1-001-A	TO-L1-001-A > PP-01-17	workstation FX-L1-001
C-TO-L1-001-B	TO-L1-001-B	L1-LOBBY	PP-01/18	SW-ACC-01/18	NET-OFFICE	-	36,9	PP-01-18 > TO-L1-001-B	TO-L1-001-B > PP-01-18	printer FX-L1-001
C-TO-L1-002-A	TO-L1-002-A	L1-LOBBY	PP-01/19	SW-ACC-01/19	NET-DEMO	-	35,6	PP-01-19 > TO-L1-002-A	TO-L1-002-A > PP-01-19	signage FX-L1-009
C-TO-L1-003-A	TO-L1-003-A	L1-MEET	PP-01/20	SW-ACC-01/20	NET-OFFICE	-	47,7	PP-01-20 > TO-L1-003-A	TO-L1-003-A > PP-01-20	table_box FX-L1-011
C-TO-L1-003-B	TO-L1-003-B	L1-MEET	PP-01/21	SW-ACC-01/21	NET-OFFICE	-	47,7	PP-01-21 > TO-L1-003-B	TO-L1-003-B > PP-01-21	spare FX-L1-011
C-TO-L1-004-A	TO-L1-004-A	L1-MEET	PP-01/22	SW-ACC-01/22	NET-OFFICE	-	50,6	PP-01-22 > TO-L1-004-A	TO-L1-004-A > PP-01-22	display FX-L1-022
C-TO-L1-005-A	TO-L1-005-A	L1-IMPL	PP-01/23	SW-ACC-01/23	NET-OFFICE	-	34,7	PP-01-23 > TO-L1-005-A	TO-L1-005-A > PP-01-23	workstation FX-L1-053
C-TO-L1-005-B	TO-L1-005-B	L1-IMPL	PP-01/24	SW-ACC-01/24	NET-OFFICE	-	34,7	PP-01-24 > TO-L1-005-B	TO-L1-005-B > PP-01-24	phone_or_spare FX-L1-053
C-TO-L1-006-A	TO-L1-006-A	L1-IMPL	PP-02/01	SW-ACC-02/01	NET-OFFICE	-	31,9	PP-02-01 > TO-L1-006-A	TO-L1-006-A > PP-02-01	workstation FX-L1-055
C-TO-L1-006-B	TO-L1-006-B	L1-IMPL	PP-02/02	SW-ACC-02/02	NET-OFFICE	-	31,9	PP-02-02 > TO-L1-006-B	TO-L1-006-B > PP-02-02	phone_or_spare FX-L1-055
C-TO-L1-007-A	TO-L1-007-A	L1-IMPL	PP-02/03	SW-ACC-02/03	NET-OFFICE	-	33,1	PP-02-03 > TO-L1-007-A	TO-L1-007-A > PP-02-03	workstation FX-L1-057
C-TO-L1-007-B	TO-L1-007-B	L1-IMPL	PP-02/04	SW-ACC-02/04	NET-OFFICE	-	33,1	PP-02-04 > TO-L1-007-B	TO-L1-007-B > PP-02-04	phone_or_spare FX-L1-057
C-TO-L1-008-A	TO-L1-008-A	L1-IMPL	PP-02/05	SW-ACC-02/05	NET-OFFICE	-	30,3	PP-02-05 > TO-L1-008-A	TO-L1-008-A > PP-02-05	workstation FX-L1-059
C-TO-L1-008-B	TO-L1-008-B	L1-IMPL	PP-02/06	SW-ACC-02/06	NET-OFFICE	-	30,3	PP-02-06 > TO-L1-008-B	TO-L1-008-B > PP-02-06	phone_or_spare FX-L1-059
C-TO-L1-009-A	TO-L1-009-A	L1-IMPL	PP-02/07	SW-ACC-02/07	NET-OFFICE	-	31,5	PP-02-07 > TO-L1-009-A	TO-L1-009-A > PP-02-07	workstation FX-L1-061
C-TO-L1-009-B	TO-L1-009-B	L1-IMPL	PP-02/08	SW-ACC-02/08	NET-OFFICE	-	31,5	PP-02-08 > TO-L1-009-B	TO-L1-009-B > PP-02-08	phone_or_spare FX-L1-061
C-TO-L1-010-A	TO-L1-010-A	L1-IMPL	PP-02/09	SW-ACC-02/09	NET-OFFICE	-	28,7	PP-02-09 > TO-L1-010-A	TO-L1-010-A > PP-02-09	workstation FX-L1-063
C-TO-L1-010-B	TO-L1-010-B	L1-IMPL	PP-02/10	SW-ACC-02/10	NET-OFFICE	-	28,7	PP-02-10 > TO-L1-010-B	TO-L1-010-B > PP-02-10	phone_or_spare FX-L1-063
C-TO-L1-011-A	TO-L1-011-A	L1-IMPL	PP-02/11	SW-ACC-02/11	NET-OFFICE	-	27,5	PP-02-11 > TO-L1-011-A	TO-L1-011-A > PP-02-11	display FX-L1-065
C-TO-L1-012-A	TO-L1-012-A	L1-NOVA	PP-02/12	SW-ACC-02/12	NET-OFFICE	-	18,3	PP-02-12 > TO-L1-012-A	TO-L1-012-A > PP-02-12	workstation FX-L1-069
C-TO-L1-012-B	TO-L1-012-B	L1-NOVA	PP-02/13	SW-ACC-02/13	NET-OFFICE	-	18,3	PP-02-13 > TO-L1-012-B	TO-L1-012-B > PP-02-13	phone_or_spare FX-L1-069
C-TO-L1-013-A	TO-L1-013-A	L1-NOVA	PP-02/14	SW-ACC-02/14	NET-OFFICE	-	15,5	PP-02-14 > TO-L1-013-A	TO-L1-013-A > PP-02-14	workstation FX-L1-071
C-TO-L1-013-B	TO-L1-013-B	L1-NOVA	PP-02/15	SW-ACC-02/15	NET-OFFICE	-	15,5	PP-02-15 > TO-L1-013-B	TO-L1-013-B > PP-02-15	phone_or_spare FX-L1-071
C-TO-L1-014-A	TO-L1-014-A	L1-LAB	PP-02/16	SW-ACC-02/16	NET-LAB	-	20,8	PP-02-16 > TO-L1-014-A	TO-L1-014-A > PP-02-16	lab_device FX-L1-075
C-TO-L1-014-B	TO-L1-014-B	L1-LAB	PP-02/17	SW-ACC-02/17	NET-LAB	-	20,8	PP-02-17 > TO-L1-014-B	TO-L1-014-B > PP-02-17	lab_device FX-L1-075
C-TO-L1-014-C	TO-L1-014-C	L1-LAB	PP-02/18	SW-ACC-02/18	NET-LAB	-	20,8	PP-02-18 > TO-L1-014-C	TO-L1-014-C > PP-02-18	lab_device FX-L1-075
C-TO-L1-014-D	TO-L1-014-D	L1-LAB	PP-02/19	SW-ACC-02/19	NET-LAB	-	20,8	PP-02-19 > TO-L1-014-D	TO-L1-014-D > PP-02-19	lab_device FX-L1-075
C-TO-L1-015-A	TO-L1-015-A	L1-LAB	PP-02/20	SW-ACC-02/20	NET-LAB	-	18,7	PP-02-20 > TO-L1-015-A	TO-L1-015-A > PP-02-20	lab_device FX-L1-076
C-TO-L1-015-B	TO-L1-015-B	L1-LAB	PP-02/21	SW-ACC-02/21	NET-LAB	-	18,7	PP-02-21 > TO-L1-015-B	TO-L1-015-B > PP-02-21	lab_device FX-L1-076
C-TO-L1-015-C	TO-L1-015-C	L1-LAB	PP-02/22	SW-ACC-02/22	NET-LAB	-	18,7	PP-02-22 > TO-L1-015-C	TO-L1-015-C > PP-02-22	lab_device FX-L1-076
C-TO-L1-015-D	TO-L1-015-D	L1-LAB	PP-02/23	SW-ACC-02/23	NET-LAB	-	18,7	PP-02-23 > TO-L1-015-D	TO-L1-015-D > PP-02-23	lab_device FX-L1-076
C-TO-L1-016-A	TO-L1-016-A	L1-LAB	PP-02/24	SW-ACC-02/24	NET-LAB	-	17,1	PP-02-24 > TO-L1-016-A	TO-L1-016-A > PP-02-24	lab_device FX-L1-077
C-TO-L1-016-B	TO-L1-016-B	L1-LAB	PP-03/01	SW-ACC-03/01	NET-LAB	-	17,1	PP-03-01 > TO-L1-016-B	TO-L1-016-B > PP-03-01	lab_device FX-L1-077
C-TO-L1-016-C	TO-L1-016-C	L1-LAB	PP-03/02	SW-ACC-03/02	NET-LAB	-	17,1	PP-03-02 > TO-L1-016-C	TO-L1-016-C > PP-03-02	lab_device FX-L1-077

Label dua ujung: sisi rack 'PP-nn-pp > port outlet', sisi outlet sebaliknya. Panjang mengikuti AS-ICT-02; batas 90 m AS-ICT-03.

STATUS KONSEP

Bukan untuk konstruksi

kantor-rpg Proyek kantor-rpg · gedung KRPG-01

Port dan device schedule

Skala	NTS @ A3 lanskap	Revisi	P03 · 2026-10-01
Render	2026-10-01 15:47:39 UTC	Halaman	halaman 1/3
Digambar	Claude Code cloud (generator)	Diperiksa	Max (supervisor) belum review
Sumber	world.json sha256 488597bb0552fbde		

Nomor lembar

ICT-401

Rev P03 · 1/3

PORT SCHEDULE

rancangan virtual, bukan topologi produksi · sumber design/derived/ict-portmap.json (world P03)

Kabel	Port outlet	Ruang	PP/port	Switch/port	Domain	PoE	m	Label sisi rack	Label sisi outlet	Endpoint
C-TO-L1-016-D	TO-L1-016-D	L1-LAB	PP-03/03	SW-ACC-03/03	NET-LAB	-	17,1	PP-03-03 > TO-L1-016-D	TO-L1-016-D > PP-03-03	lab_device FX-L1-077
C-TO-L1-017-A	TO-L1-017-A	L1-LAB	PP-03/04	SW-ACC-03/04	NET-LAB	-	13,4	PP-03-04 > TO-L1-017-A	TO-L1-017-A > PP-03-04	lab_uplink FX-L1-079
C-TO-L1-017-B	TO-L1-017-B	L1-LAB	PP-03/05	SW-ACC-03/05	NET-LAB	-	13,4	PP-03-05 > TO-L1-017-B	TO-L1-017-B > PP-03-05	spare FX-L1-079
C-TO-L1-018-A	TO-L1-018-A	L1-CEO	PP-03/06	SW-ACC-03/06	NET-OFFICE	-	39,6	PP-03-06 > TO-L1-018-A	TO-L1-018-A > PP-03-06	workstation FX-L1-082
C-TO-L1-018-B	TO-L1-018-B	L1-CEO	PP-03/07	SW-ACC-03/07	NET-OFFICE	-	39,6	PP-03-07 > TO-L1-018-B	TO-L1-018-B > PP-03-07	phone_or_spare FX-L1-082
C-TO-L1-019-A	TO-L1-019-A	L1-HUGO	PP-03/08	SW-ACC-03/08	NET-OFFICE	-	35,7	PP-03-08 > TO-L1-019-A	TO-L1-019-A > PP-03-08	workstation FX-L1-089
C-TO-L1-019-B	TO-L1-019-B	L1-HUGO	PP-03/09	SW-ACC-03/09	NET-OFFICE	-	35,7	PP-03-09 > TO-L1-019-B	TO-L1-019-B > PP-03-09	phone_or_spare FX-L1-089
C-TO-L1-020-A	TO-L1-020-A	L1-HUGO	PP-03/10	SW-ACC-03/10	NET-OFFICE	-	33,9	PP-03-10 > TO-L1-020-A	TO-L1-020-A > PP-03-10	workstation FX-L1-091
C-TO-L1-020-B	TO-L1-020-B	L1-HUGO	PP-03/11	SW-ACC-03/11	NET-OFFICE	-	33,9	PP-03-11 > TO-L1-020-B	TO-L1-020-B > PP-03-11	phone_or_spare FX-L1-091
C-TO-L1-021-A	TO-L1-021-A	L1-KEVIN	PP-03/12	SW-ACC-03/12	NET-OFFICE	-	28,3	PP-03-12 > TO-L1-021-A	TO-L1-021-A > PP-03-12	workstation FX-L1-096
C-TO-L1-021-B	TO-L1-021-B	L1-KEVIN	PP-03/13	SW-ACC-03/13	NET-OFFICE	-	28,3	PP-03-13 > TO-L1-021-B	TO-L1-021-B > PP-03-13	phone_or_spare FX-L1-096
C-TO-L1-022-A	TO-L1-022-A	L1-BRUNO	PP-03/14	SW-ACC-03/14	NET-OFFICE	-	21,9	PP-03-14 > TO-L1-022-A	TO-L1-022-A > PP-03-14	workstation FX-L1-101
C-TO-L1-022-B	TO-L1-022-B	L1-BRUNO	PP-03/15	SW-ACC-03/15	NET-OFFICE	-	21,9	PP-03-15 > TO-L1-022-B	TO-L1-022-B > PP-03-15	phone_or_spare FX-L1-101
C-TO-L2-001-A	TO-L2-001-A	L2-DINE	PP-03/16	SW-ACC-03/16	NET-DEMO	-	42,5	PP-03-16 > TO-L2-001-A	TO-L2-001-A > PP-03-16	display FX-L2-034
C-TO-L2-002-A	TO-L2-002-A	L2-GAME	PP-03/17	SW-ACC-03/17	NET-DEMO	-	24,7	PP-03-17 > TO-L2-002-A	TO-L2-002-A > PP-03-17	console FX-L2-058
C-TO-L2-002-B	TO-L2-002-B	L2-GAME	PP-03/18	SW-ACC-03/18	NET-DEMO	-	24,7	PP-03-18 > TO-L2-002-B	TO-L2-002-B > PP-03-18	display FX-L2-058
C-TO-L2-003-A	TO-L2-003-A	L2-GAME	PP-03/19	SW-ACC-03/19	NET-DEMO	-	19,1	PP-03-19 > TO-L2-003-A	TO-L2-003-A > PP-03-19	console FX-L2-061
C-TO-L2-003-B	TO-L2-003-B	L2-GAME	PP-03/20	SW-ACC-03/20	NET-DEMO	-	19,1	PP-03-20 > TO-L2-003-B	TO-L2-003-B > PP-03-20	display FX-L2-061
C-TO-L2-004-A	TO-L2-004-A	L2-GAME	PP-03/21	SW-ACC-03/21	NET-DEMO	-	24,6	PP-03-21 > TO-L2-004-A	TO-L2-004-A > PP-03-21	arcade FX-L2-064
C-TO-L2-005-A	TO-L2-005-A	L2-GAME	PP-03/22	SW-ACC-03/22	NET-DEMO	-	23,7	PP-03-22 > TO-L2-005-A	TO-L2-005-A > PP-03-22	arcade FX-L2-065
C-TO-L2-006-A	TO-L2-006-A	L2-BILLIARD	PP-03/23	SW-ACC-03/23	NET-DEMO	-	42,2	PP-03-23 > TO-L2-006-A	TO-L2-006-A > PP-03-23	display FX-L2-079
C-TO-L2-007-A	TO-L2-007-A	L2-CYM	PP-03/24	SW-ACC-03/24	NET-DEMO	-	34,2	PP-03-24 > TO-L2-007-A	TO-L2-007-A > PP-03-24	display FX-L2-087
Total	72 kabel						2074,8	port map: 2074,8 m	COCOK	

Label dua ujung: sisi rack 'PP-nn-pp > port outlet', sisi outlet sebaliknya. Panjang mengikuti AS-ICT-02; batas 90 m AS-ICT-03.

STATUS KONSEP

Bukan untuk konstruksi

kantor-rpg Proyek kantor-rpg · gedung KRPG-01

Port dan device schedule

Skala	NTS @ A3 lanskap	Revisi	P03 · 2026-10-01
Render	2026-10-01 15:47:39 UTC	Halaman	halaman 2/3
Digambar	Claude Code cloud (generator)	Diperiksa	Max (supervisor) belum review
Sumber	world.json sha256 488597bb0552fbde		

Nomor lembar

ICT-401

Rev P03 · 2/3

BOM RINGKAS DAN POE

BOM (tanpa harga): jumlah turunan dari port map; tanpa harga (AS-ICT-05)

Item	Satuan	Jumlah
Kabel tembaga horizontal (kategori TBD)	m	2074,8
Box kabel 305 m (pembulatan, belum termasuk waste)	box	7
Keystone jack sisi outlet	pcs	72
Faceplate 1 port	pcs	24
Faceplate 2 port	pcs	18
Faceplate 4 port	pcs	3
Patch panel 24 port	pcs	4
Patch cord sisi rack (1 per port terpakai, asumsi)	pcs	72
Patch cord sisi perangkat (1 per port terpakai, asumsi)	pcs	72
Access switch 48 port PoE (kelas, model TBD)	pcs	3
Access point (placeholder AS-ICT-01)	pcs	11
Kamera konsep (opsional)	pcs	5
Rack 42U (target)	pcs	2
UPS (rating TBD)	pcs	1

Harga: tidak ada (tidak ada quote bertanggal; tidak diestimasi; AS-ICT-05).

POE PER SWITCH (BELUM DIVALIDASI)

Switch	Port	Spare	Worst W	Budget W	Status
SW-ACC-01	24/48	20	407	belum ada	belum divalidasi: datasheet switch belum dipilih
SW-ACC-02	24/48	20	0	belum ada	belum divalidasi: datasheet switch belum dipilih
SW-ACC-03	24/48	20	0	belum ada	belum divalidasi: datasheet switch belum dipilih

Total PoE worst-case 407 W dari nilai PSE kelas IEEE (AS-ICT-04): belum divalidasi karena datasheet switch belum dipilih.

TOTAL

Outlet / port	45 / 72
Panjang kabel	2074,8 m (baris) vs 2074,8 m (port map): COCOK
Terpanjang / terpendek	50,6 / 12,7 m
Revisi data	port map P03 / world P03: sama

STATUS KONSEP

Bukan untuk konstruksi

kantor-rpg Proyek kantor-rpg - gedung KRPG-01

Port dan device schedule

Skala	NTS @ A3 lanskap	Revisi	P03 - 2026-10-01
Render	2026-10-01 15:47:39 UTC	Halaman	halaman 3/3
Digambar	Claude Code cloud (generator)	Diperiksa	Max (supervisor) belum review
Sumber	world.json sha256 488597bb0552fbde		

Nomor lembar

ICT-401

Rev P03 · 3/3