


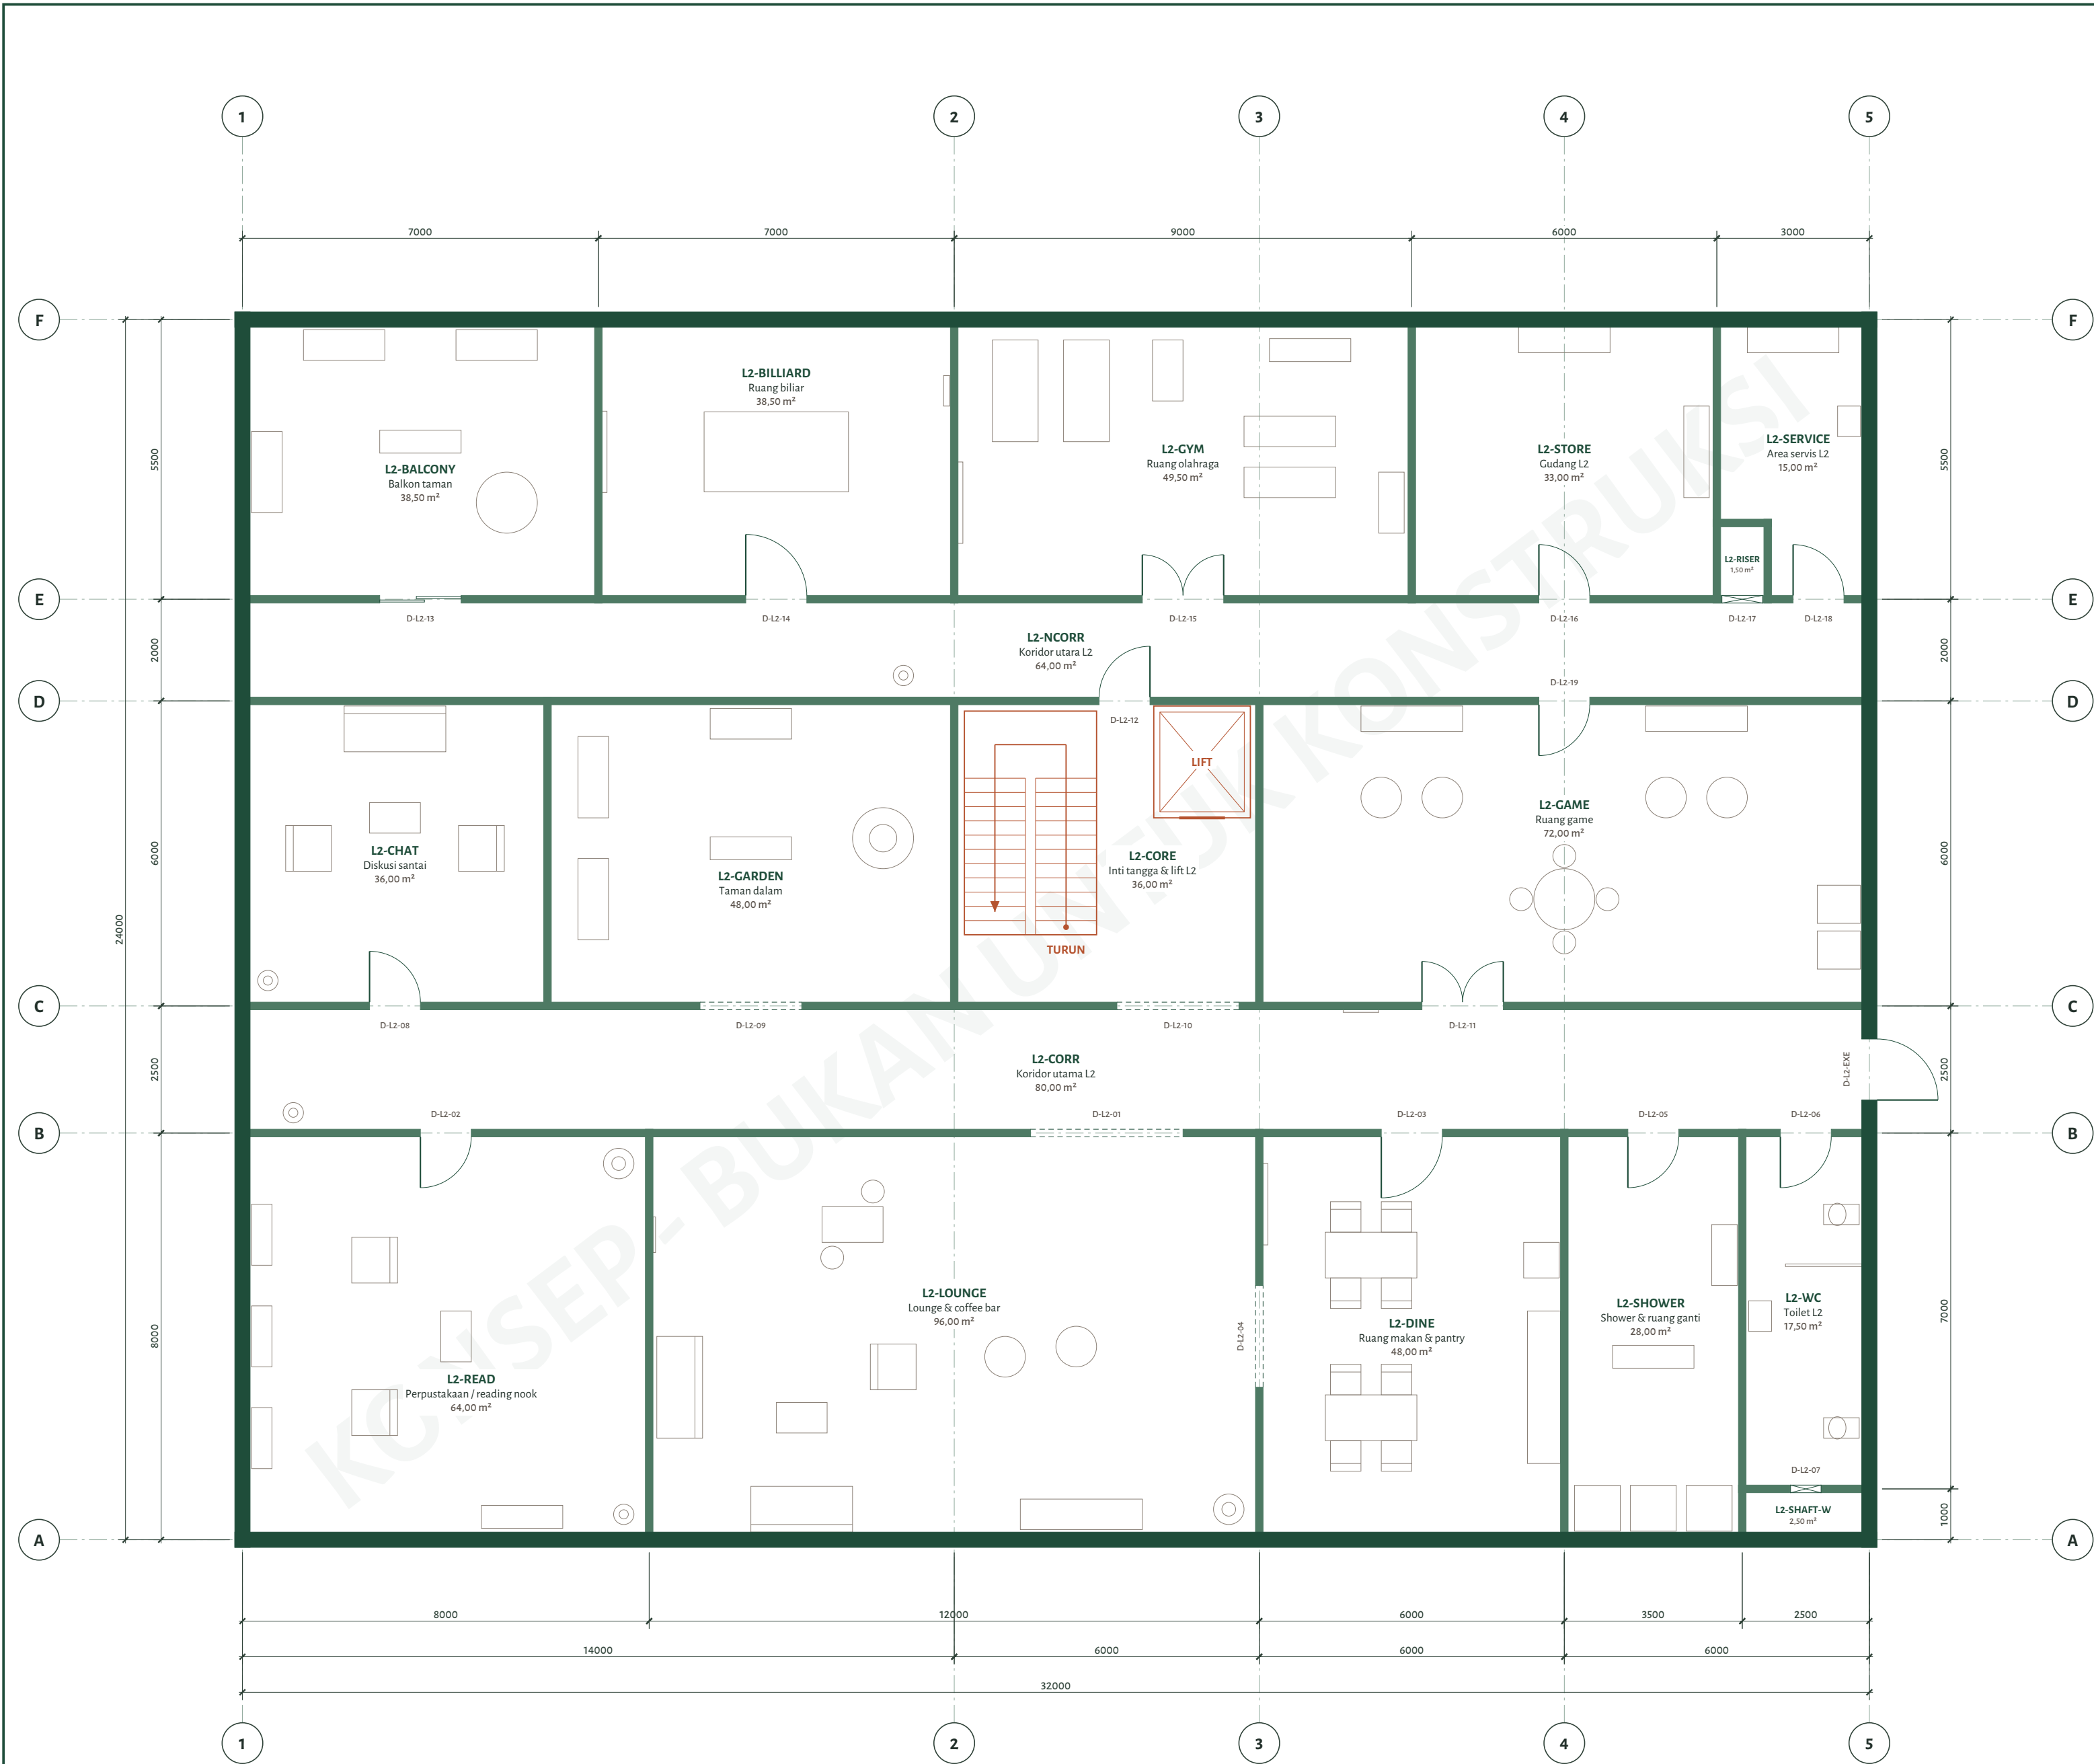

DENAH LANTAI 2

Skala 1:100 @ A2 · lantai L2 · ukuran dalam mm, as ke as dinding



Utara = sumbu Y+ dunia
Origin (0,0) sudut barat daya L1, X timur.
Grid acuan konsep dari tepi ruang (1..n, A..n),
bukan grid struktur (AS-DIM-03).

LEGENDA

	Dinding luar 0,30 m (poche hijau tua)		Dinding dalam 0,15 m
	Pintu tunggal + arah buka 90°		Pintu ganda
	Bukaan tanpa daun (garis atas putus)		Hatch akses shaft / riser
	Furniture dan fixture (catalog, AS-DIM-04)		Tangga U / lift, panah dari lantai ini
	Garis grid acuan konsep		Dimensi mm, as ke as (AS-DIM-02)
	Tag ruang: ID, nama, luas as-drawn		ID pintu (sisi tanpa ayunan)

ASUMSI (lengkap di design/world.json dan docs/assumptions.md)

- AS-DIM-01** Footprint 32 x 24 m dan tinggi antar lantai 4,0 m adalah proposal PRD, bukan lahan yang disahkan.
- AS-DIM-02** Polygon ruang diukur di as dinding; luas = luas as-drawn, bukan luas bersih.
- AS-DIM-03** Tebal dinding konsep luar 0,30 m, dalam 0,15 m; plafon 3,0 m; belum ada desain struktur.
- AS-DIM-04** Ukuran furniture dari catalog adalah target konsep, bukan katalog vendor.
- AS-DIM-05** Tangga U 24 riser x 0,1667 m, tread 0,28 m, lebar flight 1,2 m: target konsep, bukan tangga layak konstruksi.
- AS-OCC-02** Kapasitas kursi dihitung dari fixture, bukan target okupansi yang diputuskan.

DAFTAR RUANG L2 (luas as-drawn dari polygon)

ID	Nama	Luas
L2-READ	Perpustakaan / reading nook	64,00 m ²
L2-LOUNGE	Lounge & coffee bar	96,00 m ²
L2-DINE	Ruang makan & pantry	48,00 m ²
L2-SHOWER	Shower & ruang ganti	28,00 m ²
L2-SHAFT-W	Shaft basah L2	2,50 m ²
L2-WC	Toilet L2	17,50 m ²
L2-CORR	Koridor utama L2	80,00 m ²
L2-CHAT	Diskusi santai	36,00 m ²
L2-GARDEN	Taman dalam	48,00 m ²
L2-CORE	Inti tangga & lift L2	36,00 m ²
L2-GAME	Ruang game	72,00 m ²
L2-NCORR	Koridor utara L2	64,00 m ²
L2-BALCONY	Balkon taman	38,50 m ²
L2-BILLIARD	Ruang biliar	38,50 m ²
L2-CYM	Ruang olahraga	49,50 m ²
L2-STORE	Gudang L2	33,00 m ²
L2-RISER	Riser ICT L2	1,50 m ²
L2-SERVICE	Area servis L2	15,00 m ²
Jumlah 18 ruang		= envelope 32 x 24 m (768,00 m ²)
		768,00 m ²

CATATAN

- Sumber tunggal: design/world.json revisi P02; dinding diturunkan oleh tools/kantor/geometry.py (tepi polygon ruang dikurangi bukaan pintu).
- Arah ayun pintu adalah konvensi generator: pintu exit membuka ke luar, pintu lain membuka ke ruang, menjauhi koridor. world.json belum menyimpan arah ayun.
- Lantai L2: elevasi +4,00 m; 18 ruang, 20 pintu/bukaan, 91 fixture, 42 slot duduk (AS-OCC-02).
- DXF pasangan: cad/out/A-102.dxf (mm, 1:1). DWG native BLOCKED: tidak ada AutoCAD berlisensi di container; lihat cad/AUTOCAD-RUNBOOK.md.
- Pintu exit konsep di lantai ini: 1. Jalur keluar belum dinilai terhadap peraturan (AS-OCC-01).
- VL-ESC-E: Tangga darurat luar (penanda konsep, perlu kajian); tidak digambar karena di luar envelope (AS-EXIT-01).

KUNCI LANTAI

L2	elevasi +4,00 m	Lantai 2 - Rekreasi (lembar ini)
L1	elevasi ±0,00 m	Lantai 1 - Kerja & Kunjungan

RIWAYAT REVISI

Rev	Tanggal	Keterangan
P02	2026-10-01	MO seed layout dua lantai, konsep untuk review. Lembar dihasilkan dari world.json revisi ini.

kantor-rpg Proyek kantor-rpg · gedung KRPG-01

STATUS KONSEP

Bukan untuk konstruksi

Denah Lantai 2

Skala	1:100 @ A2 lanskap
Revisi	P02 · 2026-10-01
Render	2026-10-01 10:40:48 UTC
Satuan	mm (dimensi), m ² (luas)
Digambar	Claude Code cloud (generator)
Diperiksa	Max (supervisor) belum review
Sumber	world.json sha256 ac39b320919d6410
Generator	cad/generate.py v1

Nomor lembar

A-102

Rev P02

Huruf: KantorRPC Sans, turunan Alegreya Sans karya Juan Pablo del Peral (SIL OFL 1.1, paket Debian fonts-alegreya-sans), subset tertanam.