



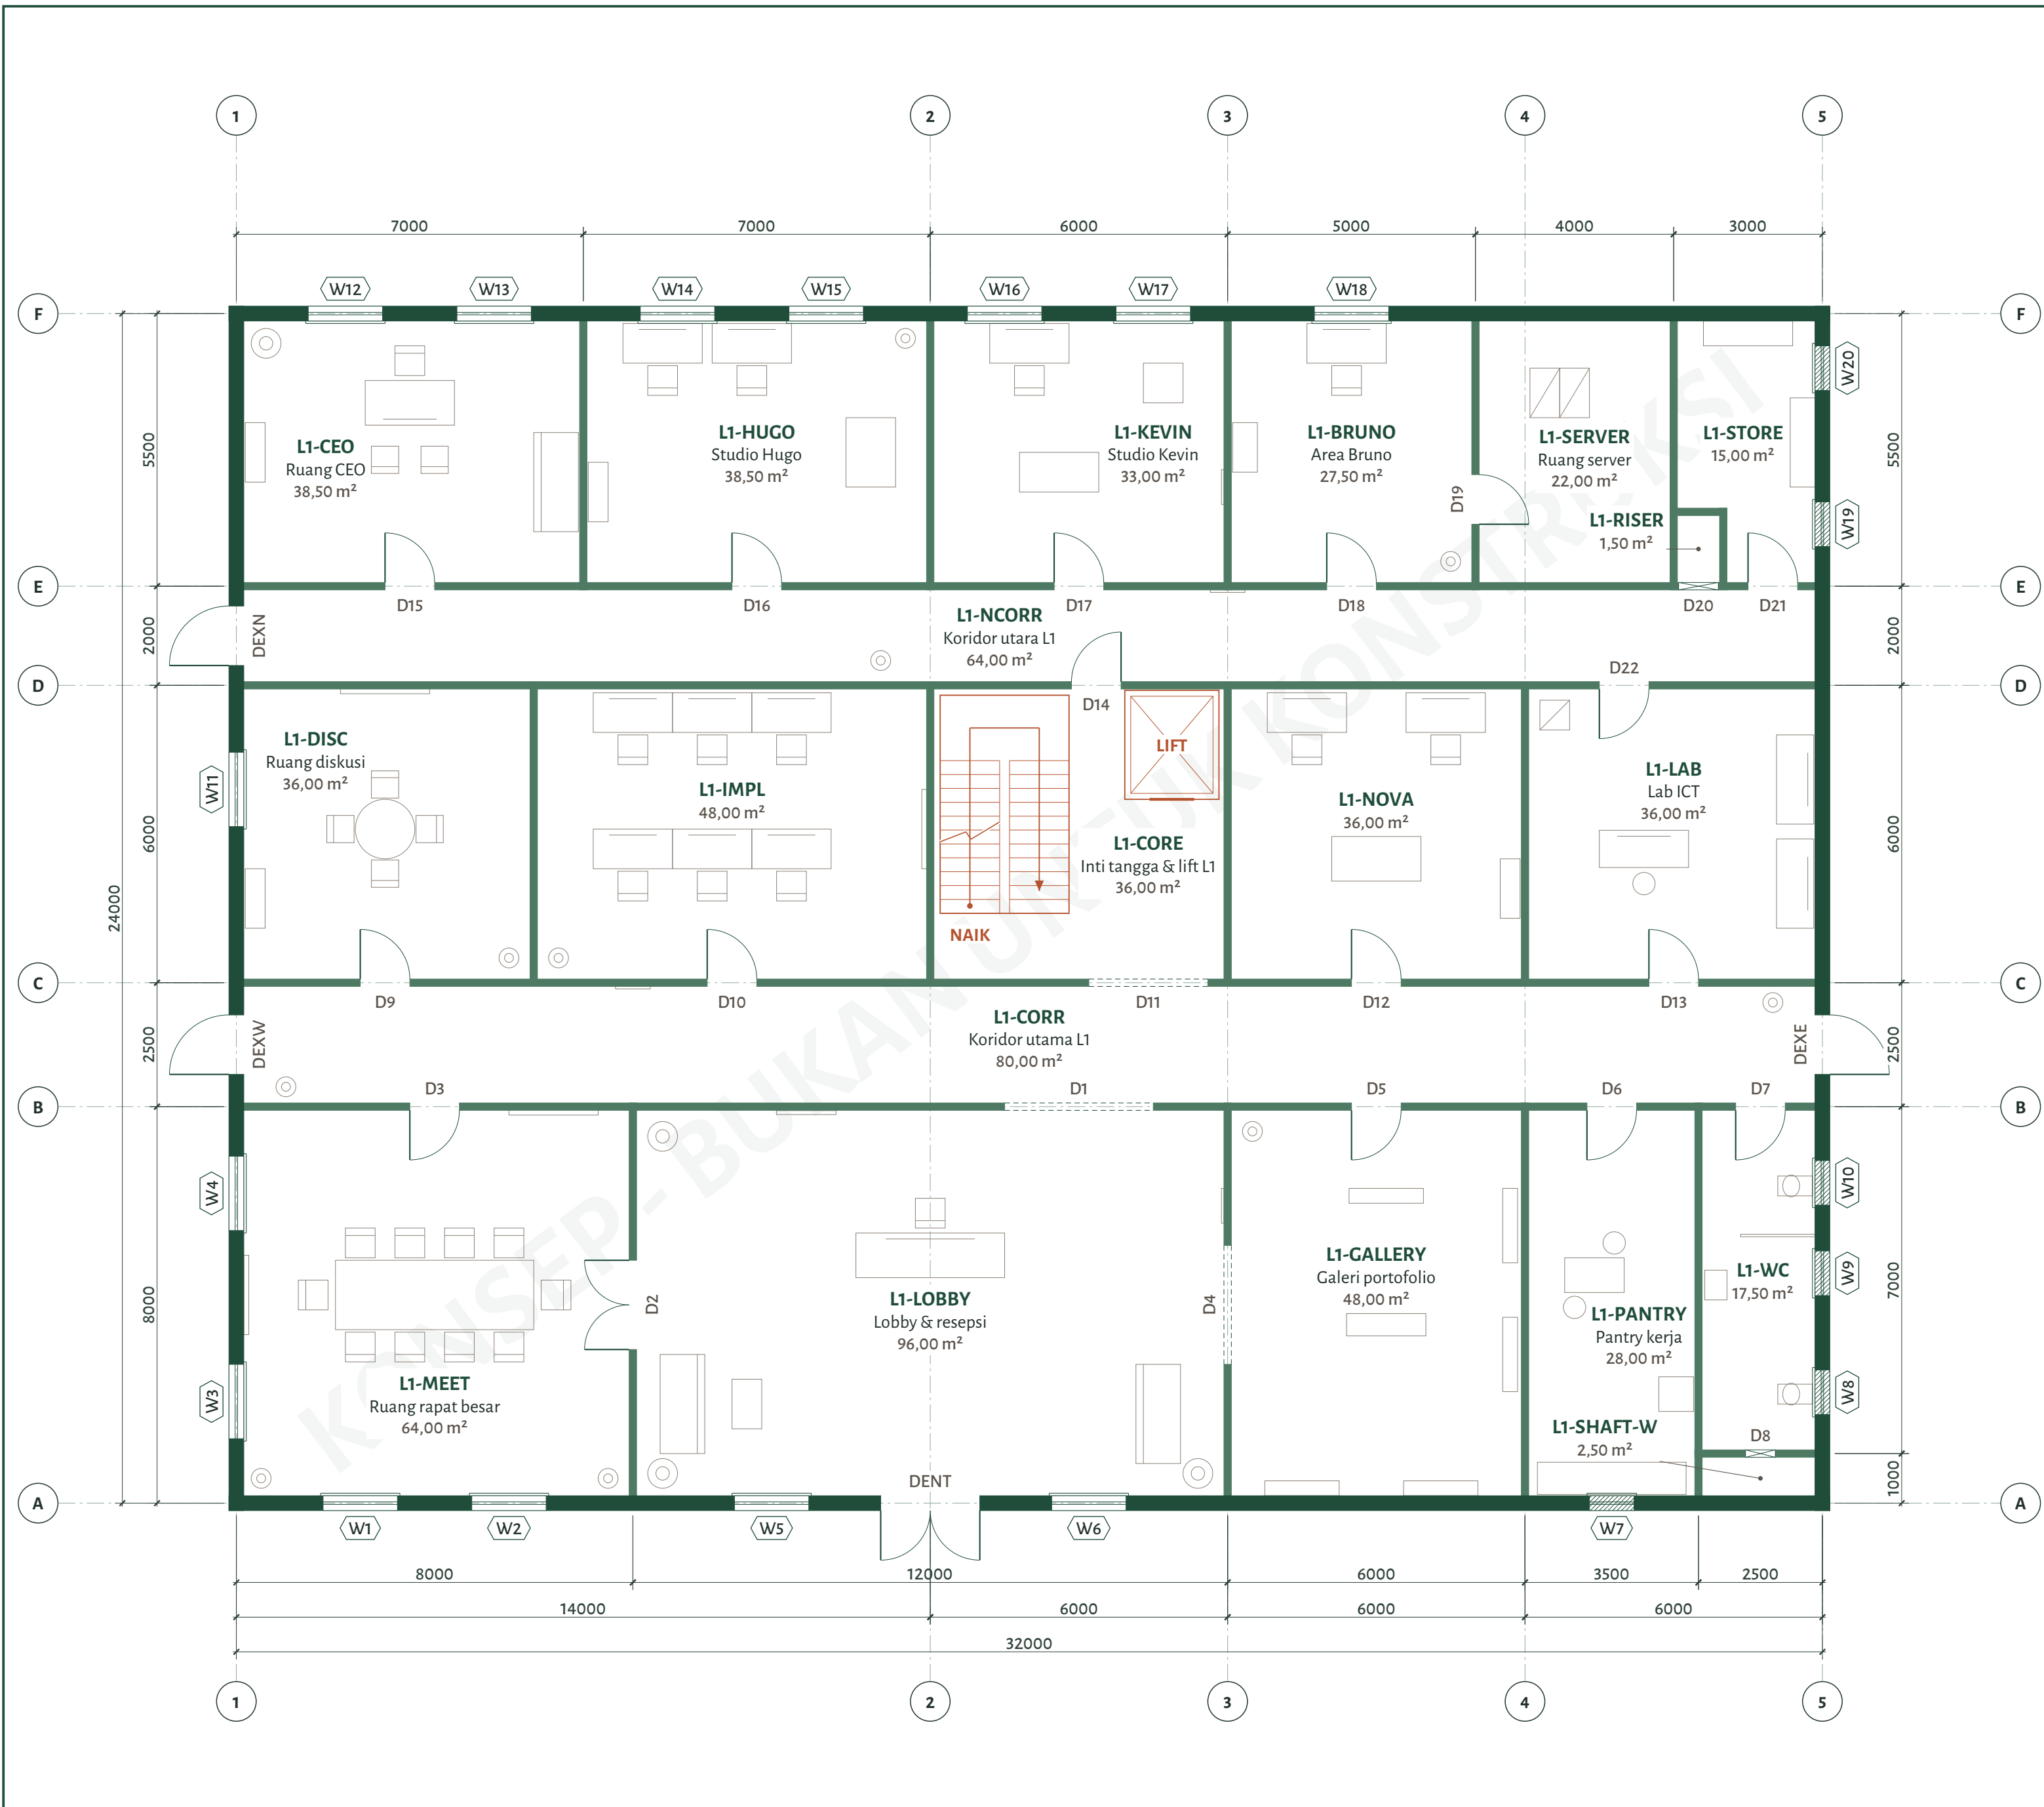

DENAH LANTAI 1

Skala 1:100 @ A2 · Lantai L1
Ukuran dalam mm, as ke as dinding

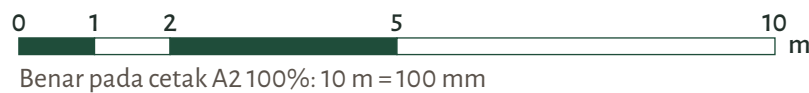

L2	+4,00 m	Rekreasi
L1	±0,00 m	Kerja & Kunjungan (lembar ini)



Utara = sumbu Y+ dunia
Origin (0,0) sudut barat daya L1, X timur. Grid acuan konsep (1..n, A..n), bukan grid struktur (AS-DIM-03).

LEGENDA

	Dinding luar 0,30 m		Dinding dalam 0,15 m
	Pintu tunggal, buka 90°		Pintu ganda
	Bukaan tanpa daun		Akses shaft / riser
	Furniture (AS-DIM-04)		Tangga U / lift
	Grid acuan konsep		Dimensi mm, as ke as
ID	Tag ruang: ID, nama, luas	Dnn	Tag pintu Dnn
	Jendela bening, tag Wnn		Jendela kaca buram

DAFTAR RUANG L1 (luas as-drawn)

ID	Nama	Luas
L1-MEET	Ruang rapat besar	64,00 m ²
L1-LOBBY	Lobby & resepsi	96,00 m ²
L1-GALLERY	Galeri portofolio	48,00 m ²
L1-PANTRY	Pantry kerja	28,00 m ²
L1-SHAFT-W	Shaft basah	2,50 m ²
L1-WC	Toilet aksesibel	17,50 m ²
L1-CORR	Koridor utama L1	80,00 m ²
L1-DISC	Ruang diskusi	36,00 m ²
L1-IMPL	Ruang implementasi & review	48,00 m ²
L1-CORE	Inti tangga & lift L1	36,00 m ²
L1-NOVA	Area Nova (spesifikasi ICT)	36,00 m ²
L1-LAB	Lab ICT	36,00 m ²
L1-NCORR	Koridor utara L1	64,00 m ²
L1-CEO	Ruang CEO	38,50 m ²
L1-HUGO	Studio Hugo	38,50 m ²
L1-KEVIN	Studio Kevin	33,00 m ²
L1-BRUNO	Area Bruno	27,50 m ²
L1-SERVER	Ruang server	22,00 m ²
L1-RISER	Riser ICT	1,50 m ²
L1-STORE	Gudang & utilitas	15,00 m ²
Jumlah 20 ruang		768,00 m ²

= envelope 32 x 24 m (768,00 m²)

CATATAN

- Sumber tunggal design/world.json revisi P03; dinding dari tools/kantor/geometry.py.
- Pintu: arah buka dan engsel dari doors[].swing. Tag Dnn = pintu D-L1-nn; daftar di A-103.
- Jendela: 20 di lantai ini, 6 buram. Tag Wnn = W-L1-Onn; ambang dan kepala di A-103 dan A-301.
- Lantai L1: 20 ruang, 26 pintu/bukaan, 108 fixture, 41 slot duduk (AS-OCC-02). Exit konsep: 4, belum dinilai terhadap peraturan (AS-OCC-01).
- Asumsi AS-DIM-01, AS-DIM-02, AS-DIM-04 dan AS-DIM-05: teks lengkap di A-001.
- DXF pasangan cad/out/A-101.dxf (mm, 1:1). DWG native BLOCKED, lihat cad/AUTOCAD-RUNBOOK.md.

RIWAYAT REVISI

Rev	Tanggal	Keterangan
P03	2026-10-01	Hardening: arah bukaan pintu dan jendela konsep di dataset; gym provisional (Q-03). Lembar dihasilkan dari world.json revisi ini.

kantor-rpg Proyek kantor-rpg · gedung KRPG-01

STATUS KONSEP

Bukan untuk konstruksi

Denah Lantai 1

L1: Lantai 1 - Kerja & Kunjungan

Skala 1:100 @ A2 lanskap
Revisi P03 · 2026-10-01
Render 2026-10-02 00:29:26 UTC
Satuan mm (dimensi), m² (luas)
Digambar Claude Code cloud (generator)
Diperiksa Max (supervisor) belum review
Sumber world.json sha256 488597bb0552fbde
Generator cad/generate.py v1

Huruf: KantorRPG Sans, turunan Alegreya Sans karya Juan Pablo del Peral (SIL OFL 1.1, paket Debian fonts-alegreya-sans), subset tertanam.

Nomor lembar

A-101

Rev P03