RK-L1-01 TAMPAK DEPAN

1:10 · L1-SERVER · 42U

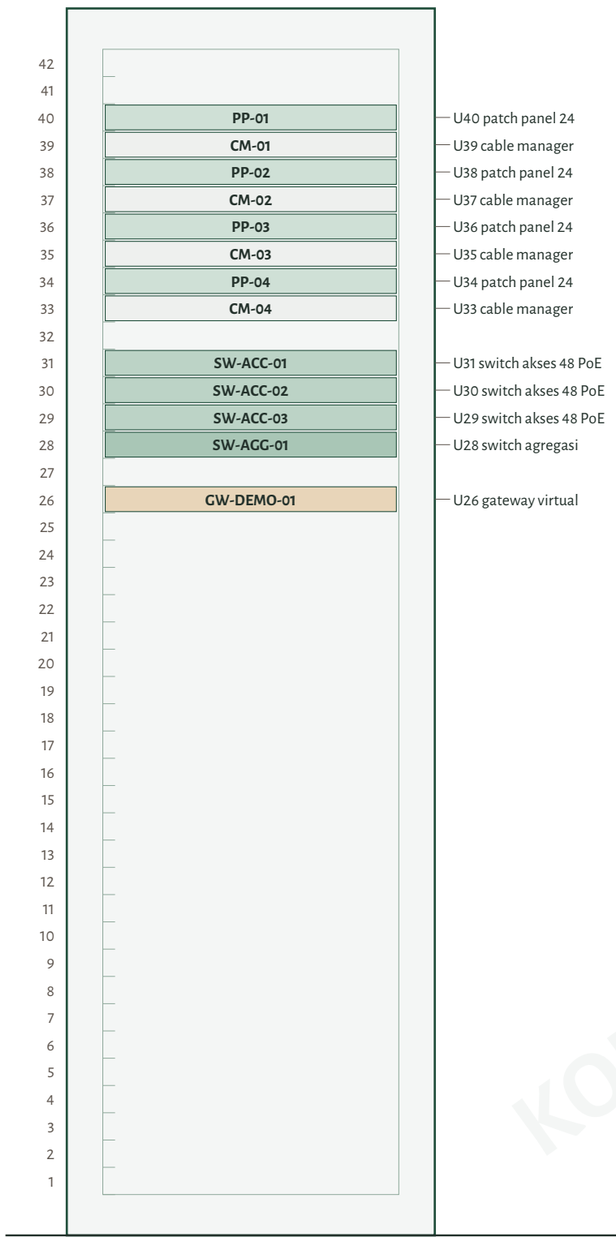

RK-L1-02 TAMPAK DEPAN

1:10 · L1-SERVER · 42U

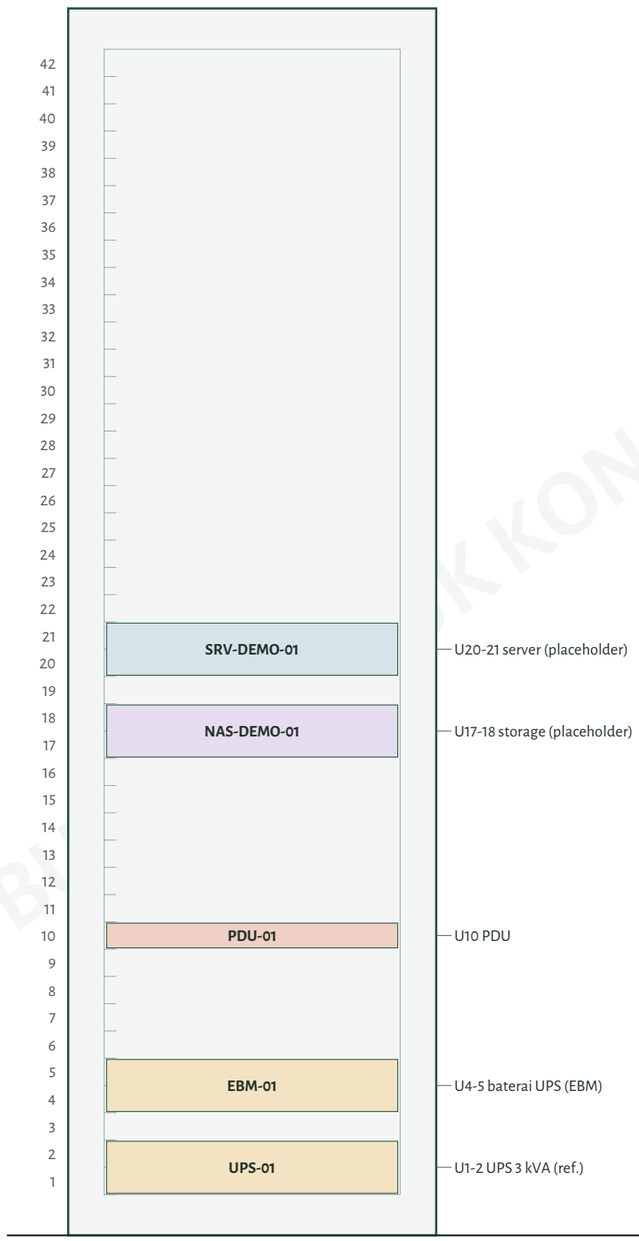

CLEARANCE RACK 1:100 (AS-ICT-06)

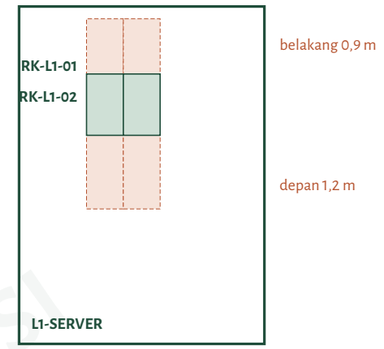

ISI RACK (world.json racks[].contents)

Rack	U	Tg	Perangkat	Tipe	Port
RK-L1-01	U40	1	PP-01	patch panel 24	24
RK-L1-01	U39	1	CM-01	cable manager	-
RK-L1-01	U38	1	PP-02	patch panel 24	24
RK-L1-01	U37	1	CM-02	cable manager	-
RK-L1-01	U36	1	PP-03	patch panel 24	24
RK-L1-01	U35	1	CM-03	cable manager	-
RK-L1-01	U34	1	PP-04	patch panel 24	24
RK-L1-01	U33	1	CM-04	cable manager	-
RK-L1-01	U31	1	SW-ACC-01	switch akses 48 PoE	48
RK-L1-01	U30	1	SW-ACC-02	switch akses 48 PoE	48
RK-L1-01	U29	1	SW-ACC-03	switch akses 48 PoE	48
RK-L1-01	U28	1	SW-AGG-01	switch agregasi	24
RK-L1-01	U26	1	GW-DEMO-01	gateway virtual	8
RK-L1-02	U20	2	SRV-DEMO-01	server (placeholder)	2
RK-L1-02	U17	2	NAS-DEMO-01	storage (placeholder)	2
RK-L1-02	U10	1	PDU-01	PDU	-
RK-L1-02	U4	2	EBM-01	baterai UPS (EBM)	-
RK-L1-02	U1	2	UPS-01	UPS 3 kVA (ref.)	-

- Skala tampak rack 1:10; 1U = 44,45 mm, nomor U dihitung dari bawah. Tg = tinggi dalam U.
- Switch, UPS 3 kVA + 1 EBM = model referensi konsep (AS-ICT-07, AS-ICT-09), bukan keputusan beli; PDU belum dipilih; tanpa harga.
- Clearance depan 1,2 m / belakang 0,9 m adalah target konsep dari catalog (AS-ICT-06), wajib diverifikasi ke standar yang dipilih.

STATUS KONSEP — Bukan untuk konstruksi

kantor-rpg Proyek kantor-rpg · gedung KRPG-01

Elevasi rack

Skala 1:10 @ A3 lanskap
Revisi P03 · 2026-10-01
Render 2026-10-10 23:31:51 UTC
Halaman 1/1
Digambar Claude Code cloud (generator)
Diperiksa Max (supervisor) belum review
Sumber world.json sha256 0252db19b7b6af27

Nomor lembar

ICT-201

Rev P03 · 1/1

Huruf: KantorRPG Sans, turunan Alegreya Sans karya Juan Pablo del Peral (SIL OFL 1.1, paket Debian fonts-alegreya-sans), subset tertanam.

KONSEP - BUKAN UNTUK KONSTRUKSI