

kantor-rpg

Paket gambar konsep · revisi P03 (2026-10-01)

KONSEP - bukan untuk konstruksi. Semua ukuran proposal untuk review.

INDEKS LEMBAR (dari design/sheets.json)

ID	Judul	Disiplin	Ukuran	Skala	Rev	Hlm	Status
A-001	Cover, indeks dan catatan umum	A	A3	NTS	P03	1	produced (konsep)
A-101	Denah Lantai 1	A	A2	1:100	P03	1	produced (konsep)
A-102	Denah Lantai 2	A	A2	1:100	P03	1	produced (konsep)
A-103	Room schedule, pintu dan jendela	A	A3	NTS	P03	2	produced (konsep)
A-201	Layout furniture Lantai 1	A	A2	1:100	P03	2	produced (konsep)
A-202	Layout furniture Lantai 2	A	A2	1:100	P03	2	produced (konsep)
A-301	Tampak	A	A3	1:200	P03	1	produced (konsep)
A-401	Potongan	A	A3	1:100	P03	1	produced (konsep)
I-101	Finish interior dan material	I	A3	1:200	P03	1	produced (konsep)
ICT-001	Topologi jaringan (virtual)	ICT	A3	NTS	P03	1	produced (konsep)
ICT-101	Outlet, AP dan kamera Lantai 1	ICT	A2	1:100	P03	1	produced (konsep)
ICT-102	Outlet, AP dan kamera Lantai 2	ICT	A2	1:100	P03	1	produced (konsep)
ICT-201	Elevasi rack	ICT	A3	1:10	P03	1	produced (konsep)
ICT-301	Pathway dan riser	ICT	A3	1:200	P03	1	produced (konsep)
ICT-401	Port dan device schedule	ICT	A3	NTS	P03	3	produced (konsep)

Total 15 lembar, 20 halaman PDF (berkas gabungan drawings/pdf/kantor-rpg-sheets-all.pdf, label halaman = ID lembar).

LEGENDA STATUS

produced (konsep)	DXF + PDF dihasilkan generator dari world.json dan dibuka ulang oleh test.
target	Belum diproduksi.
DWG native	BLOCKED: AutoCAD berlisensi tidak tersedia di container cloud. DXF bukan DWG; lihat cad/AUTOCAD-RUNBOOK.md.

CATATAN UMUM

- Satuan: dimensi gambar dalam mm (DXF model space 1:1 mm, \$INSUNITS = 4), luas dalam m², elevasi dalam m. Origin (0,0) sudut barat daya L1; X timur, Y utara.
- Semua lembar adalah KONSEP untuk review, bukan gambar konstruksi bertanda tangan. Ukuran adalah proposal (AS-DIM-01), bukan lahan, struktur, atau okupansi yang disahkan (AS-SITE-01).
- ICT adalah rancangan virtual, bukan topologi atau perangkat produksi (AS-NET-01).

DAFTAR ASUMSI (17, dari world.json)

AS-DIM-01	Footprint 32 m x 24 m per lantai dan tinggi antar lantai 4,0 m adalah proposal PRD, bukan luas lahan yang disahkan.
AS-DIM-02	Polygon ruang diukur pada garis as dinding; luas adalah luas as-drawn, bukan luas bersih/usable.
AS-DIM-03	Tebal dinding konsep: luar 0,30 m, dalam 0,15 m; plafon 3,0 m; slab 0,30 m. Belum ada desain struktur.
AS-DIM-04	Ukuran furniture dari catalog adalah target konsep (bukan katalog vendor). Meja biliar 9 ft memakai luas main 2,54 x 1,27 m dan clearance stik 1,47 m sebagai target ukuran umum, wajib dicek ulang ke spesifikasi produk.
AS-DIM-05	Tangga U: 24 riser x 0,1667 m, tread 0,28 m, lebar flight 1,2 m. Target konsep game; tidak menyatakan tangga layak konstruksi.
AS-OCC-01	Faktor beban hunian memakai IBC 2021 Table 1004.5 sebagai pembanding, bukan regulasi Indonesia yang berlaku. Perhitungan egress resmi butuh profesional.
AS-OCC-02	Kapasitas kursi dihitung dari fixture; bukan target okupansi manusia yang diputuskan Budi.
AS-EXIT-01	Tangga darurat timur L2 hanya penanda konsep di luar envelope; jalur keluar belum dinilai memenuhi peraturan.
AS-ICT-01	Jumlah AP adalah placeholder; belum ada model site/material dan target coverage. Tidak ada radius Wi-Fi efektif yang diklaim.
AS-ICT-02	Slack kabel: 3,0 m sisi rack + 0,3 m sisi outlet; tray pada 3,2 m di atas lantai jadi; outlet meja 0,3 m; outlet plafon 3,0 m. Asumsi proyek, bukan standar.
AS-ICT-03	Batas panjang permanent link 90 m dipakai sebagai target konsep (praktik umum kabel tembaga terstruktur), wajib diverifikasi ke standar yang dipilih.
AS-ICT-04	Daya PoE worst-case per kelas memakai nilai PSE IEEE 802.3af/at/bt (Class 3 = 15,4 W, Class 4 = 30 W). Kelas perangkat placeholder sampai datasheet dipilih.
AS-ICT-05	Rating UPS, thermal/AC dan harga belum ditentukan; tidak ada harga pengadaan dalam paket ini.
AS-ICT-06	Clearance rack depan 1,2 m / belakang 0,9 m adalah target konsep; verifikasi ke standar/panduan yang dipilih.
AS-NET-01	Domain jaringan office/demo/guest/lab/server adalah ID abstrak; bukan subnet, VLAN atau perangkat produksi.
AS-PERF-01	Target FPS/transfer/triangle adalah target PRD; angka hanya disebut terukur setelah benchmark tercatat.
AS-SITE-01	Lahan fisik, lokasi, budget, hosting dan okupansi manusia belum diputuskan.

STATUS KONSEP

Bukan untuk konstruksi

kantor-rpg Proyek kantor-rpg · gedung KRPG-01

Cover, indeks dan catatan umum


Skala	NTS @ A3 lanskap
Revisi	P03 · 2026-10-01
Render	2026-10-02 02:42:18 UTC
Halaman	1/1
Digambar	Claude Code cloud (generator)
Diperiksa	Max (supervisor) belum review
Sumber	world.json sha256 488597bb0552fbde

Huruf: Helvetica fallback (Alegreya Sans tidak tersedia saat build).

Nomor lembar


A-001

Rev P03 · 1/1

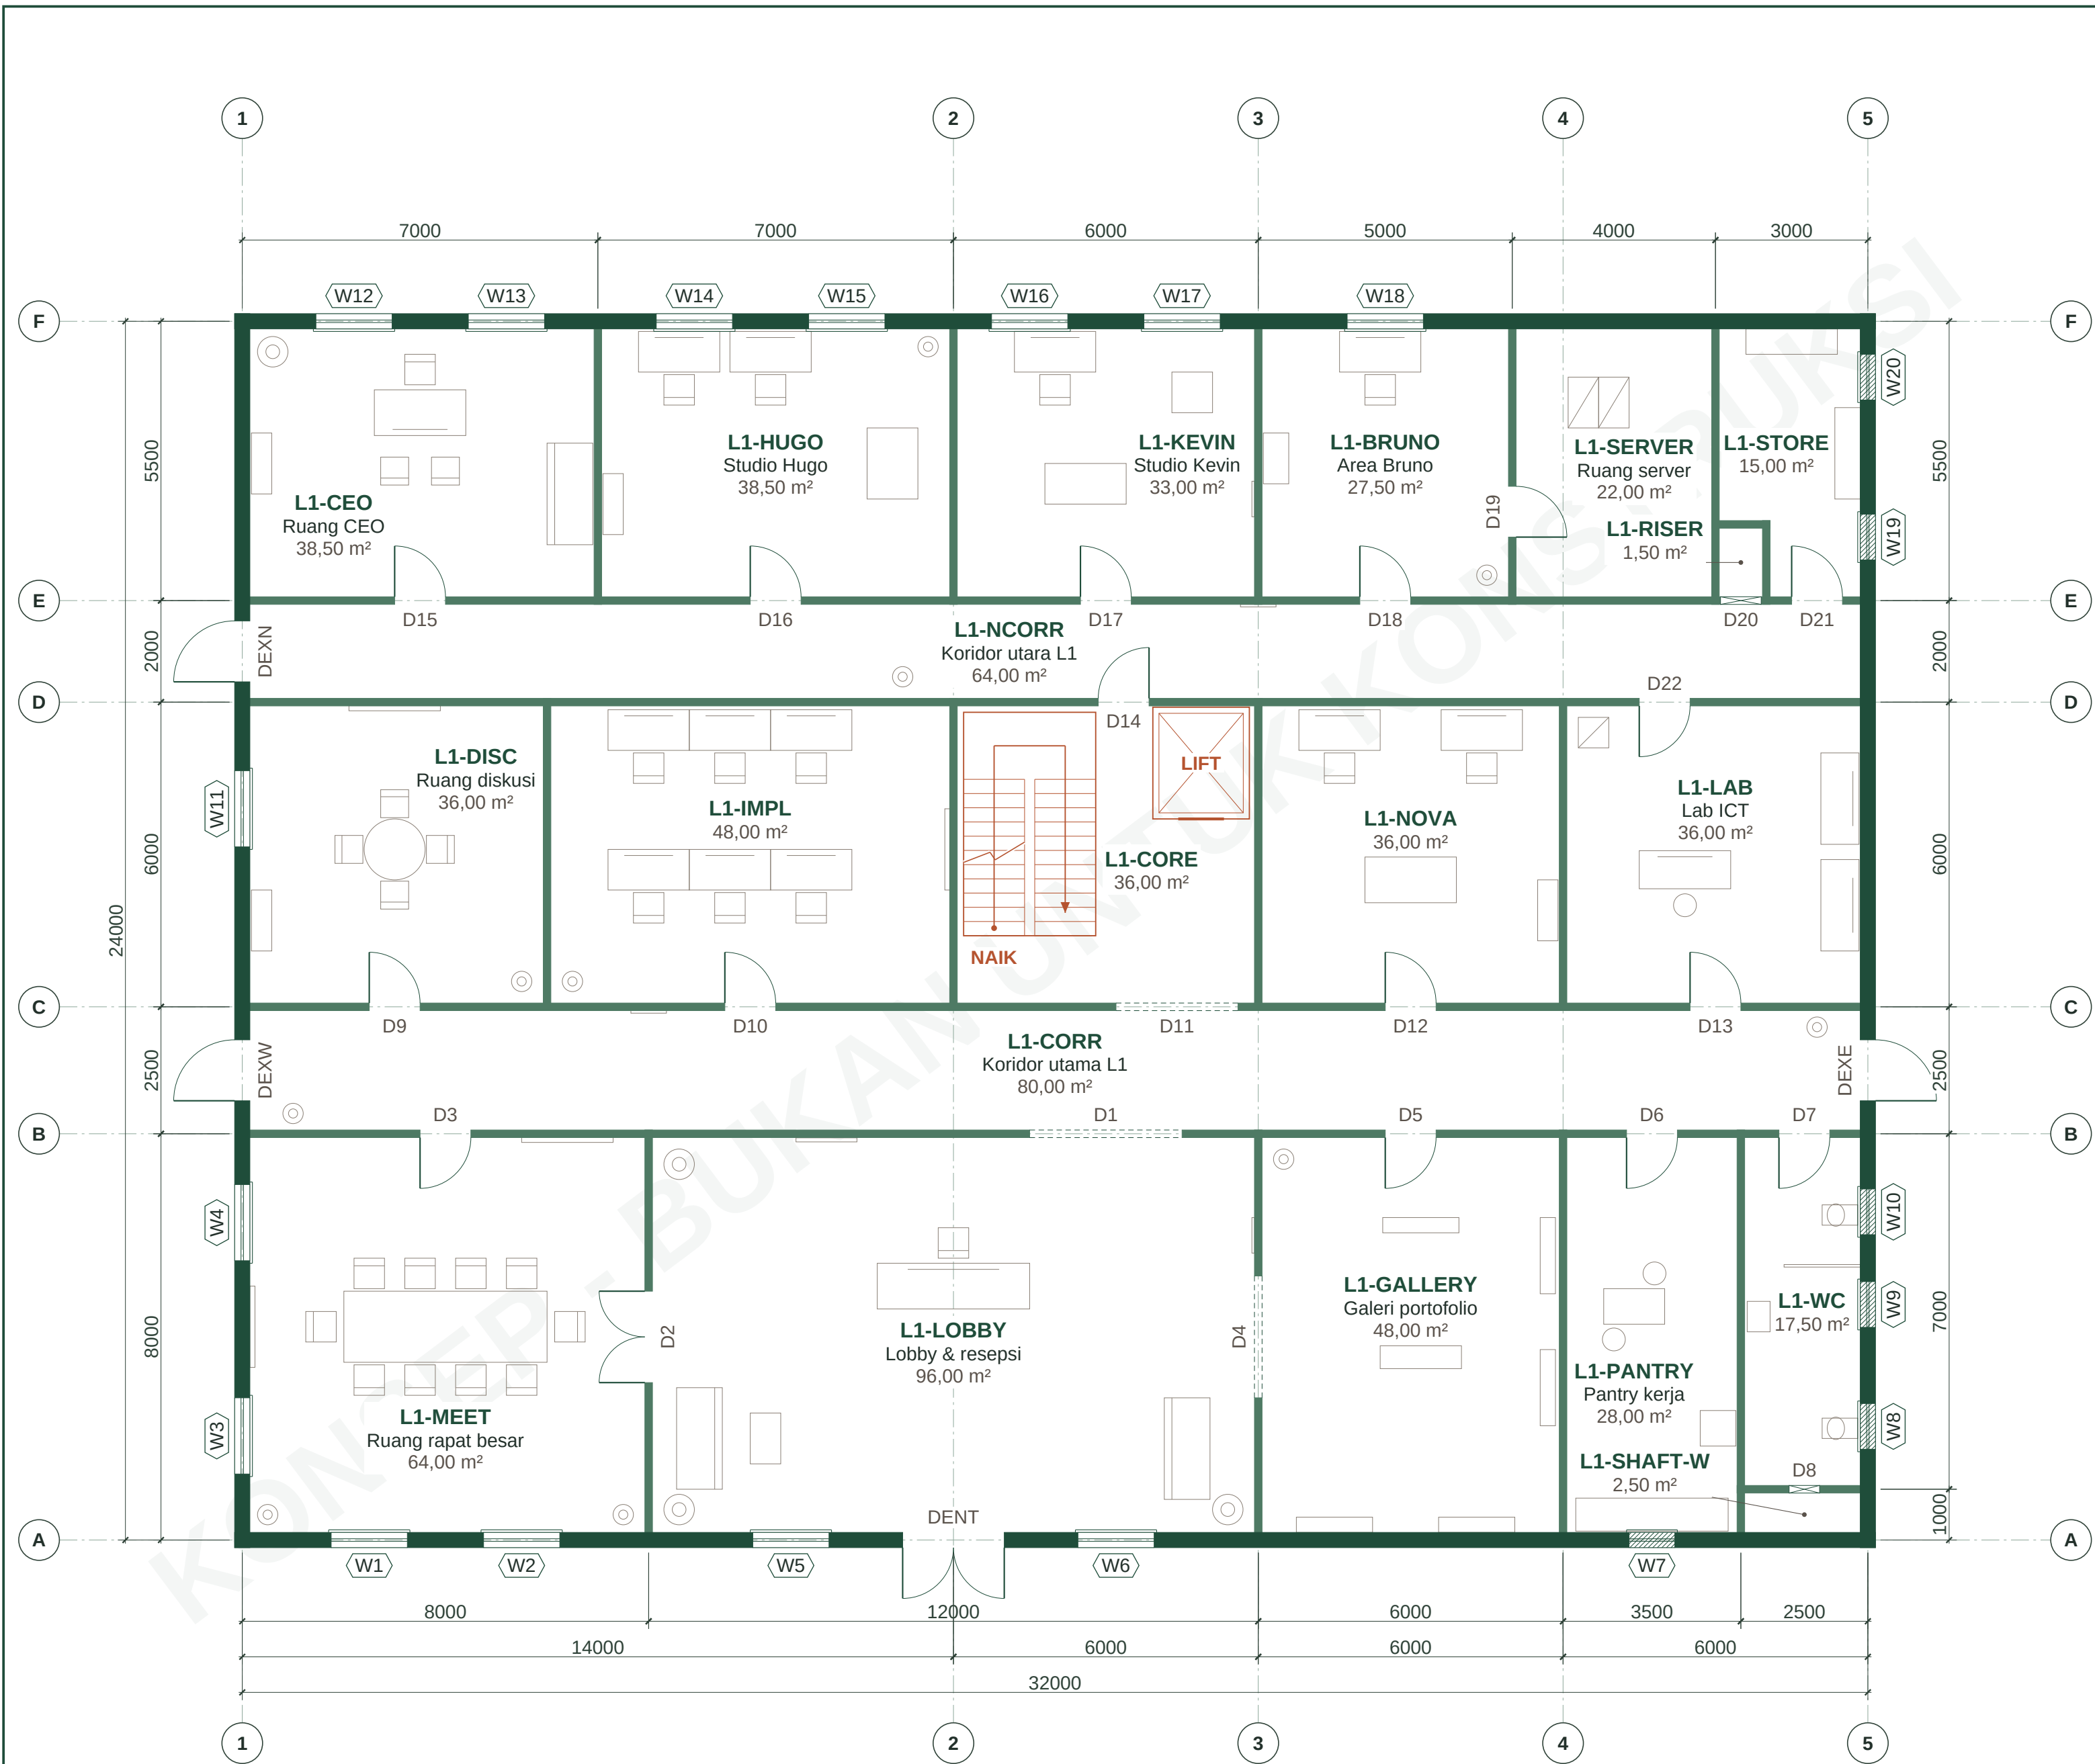

DENAH LANTAI 1

Skala 1:100 @ A2 · lantai L1
Ukuran dalam mm, as ke as dinding

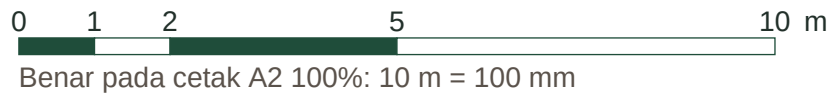

L2 +4,00 m	Rekreasi
L1 ±0,00 m	Kerja & Kunjungan (lembar ini)



Utara = sumbu Y+ dunia
Origin (0,0) sudut barat daya L1, X timur. Grid acuan konsep (1..n, A..n), bukan grid struktur (AS-DIM-03).

LEGENDA

	Dinding luar 0,30 m		Dinding dalam 0,15 m
	Pintu tunggal, buka 90°		Pintu ganda
	Bukaan tanpa daun		Akses shaft / riser
	Furniture (AS-DIM-04)		Tangga U / lift
	① Grid acuan konsep		8000 Dimensi mm, as ke as
ID	Tag ruang: ID, nama, luas	Dnn	Tag pintu Dnn
	Jendela bening, tag Wnn		Jendela kaca buram

DAFTAR RUANG L1 (luas as-drawn)

ID	Nama	Luas
L1-MEET	Ruang rapat besar	64,00 m²
L1-LOBBY	Lobby & resepsi	96,00 m²
L1-GALLERY	Galeri portofolio	48,00 m²
L1-PANTRY	Pantry kerja	28,00 m²
L1-SHAFT-W	Shaft basah	2,50 m²
L1-WC	Toilet aksesibel	17,50 m²
L1-CORR	Koridor utama L1	80,00 m²
L1-DISC	Ruang diskusi	36,00 m²
L1-IMPL	Ruang implementasi & review	48,00 m²
L1-CORE	Inti tangga & lift L1	36,00 m²
L1-NOVA	Area Nova (spesifikasi ICT)	36,00 m²
L1-LAB	Lab ICT	36,00 m²
L1-NCORR	Koridor utara L1	64,00 m²
L1-CEO	Ruang CEO	38,50 m²
L1-HUGO	Studio Hugo	38,50 m²
L1-KEVIN	Studio Kevin	33,00 m²
L1-BRUNO	Area Bruno	27,50 m²
L1-SERVER	Ruang server	22,00 m²
L1-RISER	Riser ICT	1,50 m²
L1-STORE	Gudang & utilitas	15,00 m²
Jumlah 20 ruang		768,00 m²
= envelope 32 x 24 m (768,00 m²)		

CATATAN

- Sumber tunggal design/world.json revisi P03; dinding dari tools/kantor/geometry.py.
- Pintu: arah buka dan engsel dari doors[].swing. Tag Dnn = pintu D-L1-nn; daftar di A-103.
- Jendela: 20 di lantai ini, 6 buram. Tag Wnn = W-L1-0nn; ambang dan kepala di A-103 dan A-301.
- Lantai L1: 20 ruang, 26 pintu/bukaan, 108 fixture, 41 slot duduk (AS-OCC-02). Exit konsep: 4, belum dinilai terhadap peraturan (AS-OCC-01).
- Asumsi AS-DIM-01, AS-DIM-02, AS-DIM-04 dan AS-DIM-05: teks lengkap di A-001.
- DXF pasangan cad/out/A-101.dxf (mm, 1:1). DWG native BLOCKED, lihat cad/AUTOCAD-RUNBOOK.md.

RIWAYAT REVISI

Rev	Tanggal	Keterangan
P03	2026-10-01	Hardening: arah bukaan pintu dan jendela konsep di dataset; gym provisional (Q-03). Lembar dihasilkan dari world.json revisi ini.

kantor-rpg Proyek kantor-rpg · gedung KRPG-01

STATUS KONSEP

Bukan untuk konstruksi

Denah Lantai 1

L1: Lantai 1 - Kerja & Kunjungan


Skala 1:100 @ A2 lanskap
Revisi P03 · 2026-10-01
Render 2026-10-02 02:42:18 UTC
Satuan mm (dimensi), m² (luas)
Digambar Claude Code cloud (generator)
Diperiksa Max (supervisor) belum review
Sumber world.json sha256 488597bb0552fbde
Generator cad/generate.py v1

Huruf: Helvetica fallback (Alegreya Sans tidak tersedia saat build).

Nomor lembar


A-101

Rev P03

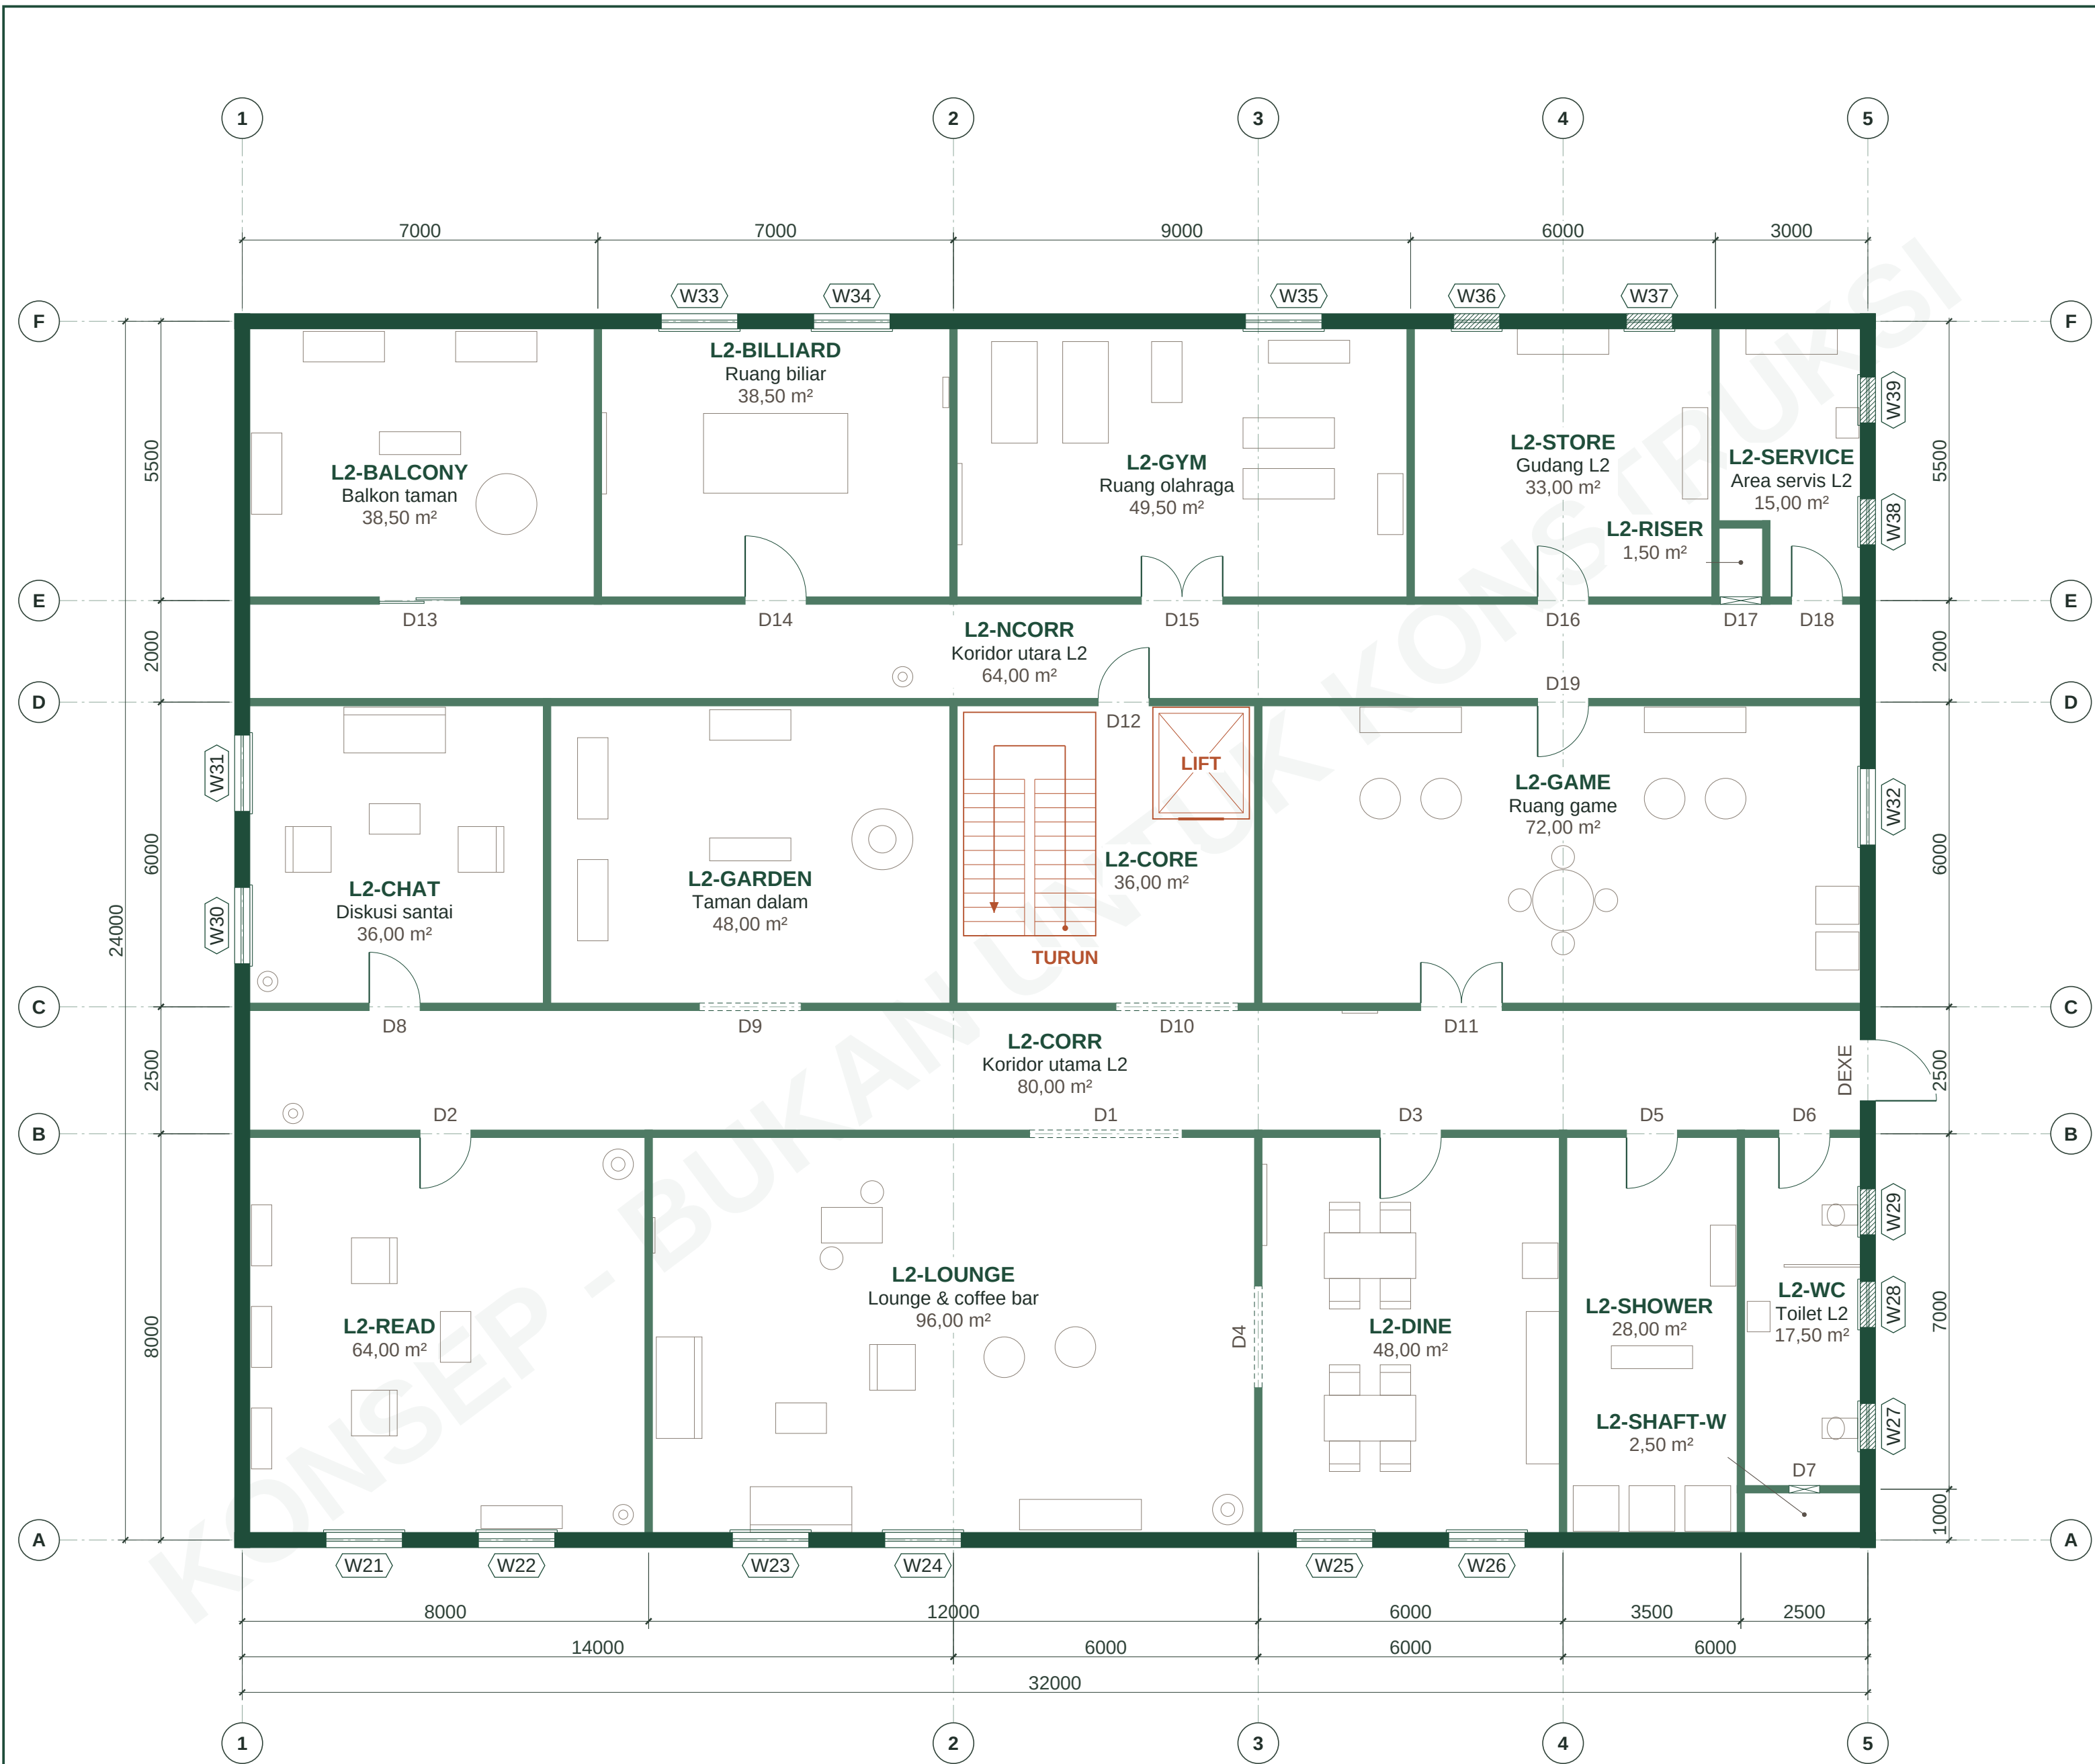

DENAH LANTAI 2

Skala 1:100 @ A2 · lantai L2
Ukuran dalam mm, as ke as dinding

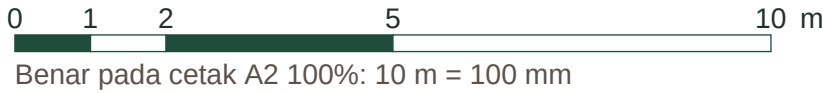

L2 +4,00 m	Rekreasi (lembar ini)
L1 ±0,00 m	Kerja & Kunjungan



Utara = sumbu Y+ dunia
Origin (0,0) sudut barat daya L1, X timur. Grid acuan konsep (1..n, A..n), bukan grid struktur (AS-DIM-03).

LEGENDA

Dinding luar 0,30 m	Dinding dalam 0,15 m
Pintu tunggal, buka 90°	Pintu ganda
Bukaan tanpa daun	Akses shaft / riser
Furniture (AS-DIM-04)	Tangga U / lift
Grid acuan konsep	Dimensi mm, as ke as
ID Tag ruang: ID, nama, luas	Dnn Tag pintu Dnn
Jendela bening, tag Wnn	Jendela kaca buram

DAFTAR RUANG L2 (luas as-drawn)

ID	Nama	Luas
L2-READ	Perpustakaan / reading nook	64,00 m²
L2-LOUNGE	Lounge & coffee bar	96,00 m²
L2-DINE	Ruang makan & pantry	48,00 m²
L2-SHOWER	Shower & ruang ganti	28,00 m²
L2-SHAFT-W	Shaft basah L2	2,50 m²
L2-WC	Toilet L2	17,50 m²
L2-CORR	Koridor utama L2	80,00 m²
L2-CHAT	Diskusi santai	36,00 m²
L2-GARDEN	Taman dalam	48,00 m²
L2-CORE	Inti tangga & lift L2	36,00 m²
L2-GAME	Ruang game	72,00 m²
L2-NCORR	Koridor utara L2	64,00 m²
L2-BALCONY	Balkon taman	38,50 m²
L2-BILLIARD	Ruang biliar	38,50 m²
L2-GYM	Ruang olahraga	49,50 m²
L2-STORE	Gudang L2	33,00 m²
L2-RISER	Riser ICT L2	1,50 m²
L2-SERVICE	Area servis L2	15,00 m²
Jumlah 18 ruang		768,00 m²
= envelope 32 x 24 m (768,00 m²)		

CATATAN

- Sumber tunggal design/world.json revisi P03; dinding dari tools/kantor/geometry.py.
- Pintu: arah buka dan engsel dari doors[].swing. Tag Dnn = pintu D-L2-nn; daftar di A-103.
- Jendela: 19 di lantai ini, 7 buram. Tag Wnn = W-L2-0nn; ambang dan kepala di A-103 dan A-301.
- Lantai L2: 18 ruang, 20 pintu/bukaan, 91 fixture, 42 slot duduk (AS-OCC-02). Exit konsep: 1, belum dinilai terhadap peraturan (AS-OCC-01).
- Asumsi AS-DIM-01, AS-DIM-02, AS-DIM-04 dan AS-DIM-05: teks lengkap di A-001.
- DXF pasangan cad/out/A-102.dxf (mm, 1:1). DWG native BLOCKED, lihat cad/AUTOCAD-RUNBOOK.md.
- VL-ESC-E: Tangga darurat luar (penanda konsep, perlu kajian); di luar envelope, tidak digambar (AS-EXIT-01).

RIWAYAT REVISI

Rev	Tanggal	Keterangan
P03	2026-10-01	Hardening: arah bukaan pintu dan jendela konsep di dataset; gym provisional (Q-03). Lembar dihasilkan dari world.json revisi ini.

kantor-rpg Proyek kantor-rpg · gedung KRPG-01

STATUS KONSEP

Bukan untuk konstruksi

Denah Lantai 2

L2: Lantai 2 - Rekreasi

Skala 1:100 @ A2 lanskap
Revisi P03 · 2026-10-01
Render 2026-10-02 02:42:18 UTC
Satuan mm (dimensi), m² (luas)
Digambar Claude Code cloud (generator)
Diperiksa Max (supervisor) belum review
Sumber world.json sha256 488597bb0552fbde
Generator cad/generate.py v1

Huruf: Helvetica fallback (Alegreya Sans tidak tersedia saat build).

Nomor lembar

A-102

Rev P03

ROOM SCHEDULE NTS · luas as-drawn dari polygon (AS-DIM-02)

ID	Nama	Lantai	Kategori	Akses	Luas m²	Kursi	Pintu	Finish lantai	Finish dinding	Finish plafon
L1-MEET	Ruang rapat besar	L1	work	public	64,00	10	D-L1-02, D-L1-03	karpet tile matte	cat matte krem	akustik panel
L1-LOBBY	Lobby & resepsi	L1	public	public	96,00	5	D-L1-ENT, D-L1-01, D-L1-02, D-L1-04	vinyl motif kayu	cat matte krem + panel kayu	gypsum
L1-GALLERY	Galeri portofolio	L1	public	public	48,00	2	D-L1-04, D-L1-05	vinyl motif kayu	cat matte krem + panel kayu	gypsum
L1-PANTRY	Pantry kerja	L1	wet	staff	28,00	2	D-L1-06	keramik anti-slip	keramik dinding	gypsum tahan lembab
L1-SHAFT-W	Shaft basah	L1	shaft	restricted	2,50	0	D-L1-08	-	-	-
L1-WC	Toilet aksesibel	L1	wet	public	17,50	0	D-L1-07, D-L1-08	keramik anti-slip	keramik dinding	gypsum tahan lembab
L1-CORR	Koridor utama L1	L1	circulation	public	80,00	0	D-L1-01, D-L1-03, D-L1-05, D-L1-06, D-L1-07, D-L1-EXW, D-L1-EXE, D-L1-09, D-L1-10, D-L1-11, D-L1-12, D-L1-13	vinyl motif kayu	cat matte krem + panel kayu	gypsum
L1-DISC	Ruang diskusi	L1	quiet	staff	36,00	4	D-L1-09	karpet tile matte	cat matte krem	akustik panel
L1-IMPL	Ruang implementasi & review	L1	work	staff	48,00	6	D-L1-10	karpet tile matte	cat matte krem	akustik panel
L1-CORE	Inti tangga & lift L1	L1	circulation	public	36,00	0	D-L1-11, D-L1-14	vinyl motif kayu	cat matte krem + panel kayu	gypsum
L1-NOVA	Area Nova (spesifikasi ICT)	L1	work	staff	36,00	2	D-L1-12	karpet tile matte	cat matte krem	akustik panel
L1-LAB	Lab ICT	L1	work	staff	36,00	1	D-L1-13, D-L1-22	vinyl anti-statik (target)	cat matte	gypsum + akses tray
L1-NCORR	Koridor utara L1	L1	circulation	staff	64,00	0	D-L1-14, D-L1-22, D-L1-EXN, D-L1-15, D-L1-16, D-L1-17, D-L1-18, D-L1-20, D-L1-21	vinyl motif kayu	cat matte krem + panel kayu	gypsum
L1-CEO	Ruang CEO	L1	quiet	staff	38,50	5	D-L1-15	karpet tile matte	cat matte krem	akustik panel
L1-HUGO	Studio Hugo	L1	work	staff	38,50	2	D-L1-16	vinyl motif kayu	cat matte krem + panel kayu	gypsum
L1-KEVIN	Studio Kevin	L1	work	staff	33,00	1	D-L1-17	vinyl motif kayu	cat matte krem + panel kayu	gypsum
L1-BRUNO	Area Bruno	L1	work	staff	27,50	1	D-L1-18, D-L1-19	vinyl anti-statik (target)	cat matte	gypsum + akses tray
L1-SERVER	Ruang server	L1	restricted	restricted	22,00	0	D-L1-19	vinyl anti-statik (target)	cat matte	gypsum + akses tray
L1-RISER	Riser ICT	L1	shaft	restricted	1,50	0	D-L1-20	-	-	-
L1-STORE	Gudang & utilitas	L1	service	staff	15,00	0	D-L1-21	epoxy	cat matte	gypsum
Subtotal L1	20 ruang				768,00	41	cek: jumlah = envelope 768,00 m² COCOK			
L2-READ	Perpustakaan / reading nook	L2	quiet	staff	64,00	4	D-L2-02	karpet tile matte	cat matte krem	akustik panel
L2-LOUNGE	Lounge & coffee bar	L2	recreation	staff	96,00	9	D-L2-01, D-L2-04	vinyl motif kayu	cat matte krem + panel kayu	gypsum
L2-DINE	Ruang makan & pantry	L2	recreation	staff	48,00	8	D-L2-03, D-L2-04	keramik anti-slip	keramik dinding	gypsum tahan lembab
L2-SHOWER	Shower & ruang ganti	L2	wet	staff	28,00	2	D-L2-05	keramik anti-slip	keramik dinding	gypsum tahan lembab
L2-SHAFT-W	Shaft basah L2	L2	shaft	restricted	2,50	0	D-L2-07	-	-	-
L2-WC	Toilet L2	L2	wet	staff	17,50	0	D-L2-06, D-L2-07	keramik anti-slip	keramik dinding	gypsum tahan lembab
L2-CORR	Koridor utama L2	L2	circulation	staff	80,00	0	D-L2-01, D-L2-02, D-L2-03, D-L2-05, D-L2-06, D-L2-EXE, D-L2-08, D-L2-09, D-L2-10, D-L2-11	vinyl motif kayu	cat matte krem + panel kayu	gypsum
L2-CHAT	Diskusi santai	L2	quiet	staff	36,00	4	D-L2-08	karpet tile matte	cat matte krem	akustik panel
L2-GARDEN	Taman dalam	L2	recreation	staff	48,00	2	D-L2-09	deck komposit	panel tanaman	terbuka/pergola
L2-CORE	Inti tangga & lift L2	L2	circulation	staff	36,00	0	D-L2-10, D-L2-12	vinyl motif kayu	cat matte krem + panel kayu	gypsum
L2-GAME	Ruang game	L2	recreation	staff	72,00	8	D-L2-11, D-L2-19	vinyl motif kayu	cat matte krem + panel kayu	gypsum
L2-NCORR	Koridor utara L2	L2	circulation	staff	64,00	0	D-L2-12, D-L2-19, D-L2-13, D-L2-14, D-L2-15, D-L2-16, D-L2-17, D-L2-18	vinyl motif kayu	cat matte krem + panel kayu	gypsum
L2-BALCONY	Balkon taman	L2	outdoor	staff	38,50	2	D-L2-13	deck komposit	panel tanaman	terbuka/pergola
L2-BILLIARD	Ruang biliar	L2	recreation	staff	38,50	0	D-L2-14	karpet tile matte	cat matte krem	akustik panel
L2-GYM	Ruang olahraga	L2	recreation	staff	49,50	3	D-L2-15	lantai karet olahraga	cat matte	akustik panel
L2-STORE	Gudang L2	L2	service	staff	33,00	0	D-L2-16	epoxy	cat matte	gypsum
L2-RISER	Riser ICT L2	L2	shaft	restricted	1,50	0	D-L2-17	-	-	-
L2-SERVICE	Area servis L2	L2	service	staff	15,00	0	D-L2-18	epoxy	cat matte	gypsum
Subtotal L2	18 ruang				768,00	42	cek: jumlah = envelope 768,00 m² COCOK			

- Sumber: tools/room_schedule.py atas design/world.json revisi P03; tabel dan subtotal dihitung saat render.
- Kursi = slot duduk dari fixture (AS-OCC-02), bukan target okupansi.
- Pemeriksaan: jumlah luas ruang per lantai harus sama dengan luas envelope; hasil tertulis di baris subtotal tiap lantai.
- Halaman 1 dari 2; schedule pintu dan jendela di halaman 2.

STATUS KONSEP

Bukan untuk konstruksi

kantor-rpg Proyek kantor-rpg · gedung KRPg-01

Room schedule, pintu dan jendela

Skala NTS @ A3 lanskap
Revisi P03 · 2026-10-01
Render 2026-10-02 02:42:18 UTC
Halaman 1/2
Digambar Claude Code cloud (generator)
Diperiksa Max (supervisor) belum review
Sumber world.json sha256 488597bb0552fbde

Huruf: Helvetica fallback (Alegreya Sans tidak tersedia saat build).

Nomor lembar

A-103

Rev P03 · 1/2

SCHEDULE PINTU DAN JENDELA

NTS · dari world.json doors[] dan windows[] revisi P03

ID pintu	Tag	Lantai	Ruang yang dihubungkan	Tipe	Lebar m	Buka ke	Engsel	Exit
D-L1-ENT	DENT	L1	EXT / L1-LOBBY	double	2	EXT (luar)	both (2 daun)	ya
D-L1-01	D1	L1	L1-LOBBY / L1-CORR	opening	3	-	-	
D-L1-02	D2	L1	L1-LOBBY / L1-MEET	double	1,8	L1-MEET	both (2 daun)	
D-L1-03	D3	L1	L1-MEET / L1-CORR	single	1	L1-MEET	low (barat)	
D-L1-04	D4	L1	L1-LOBBY / L1-GALLERY	opening	2,4	-	-	
D-L1-05	D5	L1	L1-GALLERY / L1-CORR	single	1	L1-GALLERY	low (barat)	
D-L1-06	D6	L1	L1-PANTRY / L1-CORR	single	1	L1-PANTRY	low (barat)	
D-L1-07	D7	L1	L1-WC / L1-CORR	single	1	L1-WC	low (barat)	
D-L1-08	D8	L1	L1-WC / L1-SHAFT-W	hatch	0,6	-	-	
D-L1-EXW	DEXW	L1	EXT / L1-CORR	single	1,2	EXT (luar)	low (selatan)	ya
D-L1-EXE	DEXE	L1	EXT / L1-CORR	single	1,2	EXT (luar)	low (selatan)	ya
D-L1-09	D9	L1	L1-CORR / L1-DISC	single	1	L1-DISC	low (barat)	
D-L1-10	D10	L1	L1-CORR / L1-IMPL	single	1	L1-IMPL	low (barat)	
D-L1-11	D11	L1	L1-CORR / L1-CORE	opening	2,4	-	-	
D-L1-12	D12	L1	L1-CORR / L1-NOVA	single	1	L1-NOVA	low (barat)	
D-L1-13	D13	L1	L1-CORR / L1-LAB	single	1	L1-LAB	low (barat)	
D-L1-14	D14	L1	L1-CORE / L1-NCORR	single	1	L1-NCORR	high (timur)	
D-L1-22	D22	L1	L1-LAB / L1-NCORR	single	1	L1-LAB	low (barat)	
D-L1-EXN	DEXN	L1	EXT / L1-NCORR	single	1,2	EXT (luar)	low (selatan)	ya
D-L1-15	D15	L1	L1-NCORR / L1-CEO	single	1	L1-CEO	low (barat)	
D-L1-16	D16	L1	L1-NCORR / L1-HUGO	single	1	L1-HUGO	low (barat)	
D-L1-17	D17	L1	L1-NCORR / L1-KEVIN	single	1	L1-KEVIN	low (barat)	
D-L1-18	D18	L1	L1-NCORR / L1-BRUNO	single	1	L1-BRUNO	low (barat)	
D-L1-19	D19	L1	L1-BRUNO / L1-SERVER	single	1	L1-SERVER	low (selatan)	
D-L1-20	D20	L1	L1-NCORR / L1-RISER	hatch	0,8	-	-	
D-L1-21	D21	L1	L1-NCORR / L1-STORE	single	1	L1-STORE	low (barat)	
D-L2-01	D1	L2	L2-LOUNGE / L2-CORR	opening	3	-	-	
D-L2-02	D2	L2	L2-READ / L2-CORR	single	1	L2-READ	low (barat)	
D-L2-03	D3	L2	L2-DINE / L2-CORR	single	1,2	L2-DINE	low (barat)	
D-L2-04	D4	L2	L2-LOUNGE / L2-DINE	opening	2	-	-	
D-L2-05	D5	L2	L2-SHOWER / L2-CORR	single	1	L2-SHOWER	low (barat)	
D-L2-06	D6	L2	L2-WC / L2-CORR	single	1	L2-WC	low (barat)	
D-L2-07	D7	L2	L2-WC / L2-SHAFT-W	hatch	0,6	-	-	
D-L2-EXE	DEXE	L2	EXT / L2-CORR	single	1,2	EXT (luar)	low (selatan)	ya
D-L2-08	D8	L2	L2-CORR / L2-CHAT	single	1	L2-CHAT	low (barat)	
D-L2-09	D9	L2	L2-CORR / L2-GARDEN	opening	2	-	-	
D-L2-10	D10	L2	L2-CORR / L2-CORE	opening	2,4	-	-	
D-L2-11	D11	L2	L2-CORR / L2-GAME	double	1,6	L2-GAME	both (2 daun)	
D-L2-12	D12	L2	L2-CORE / L2-NCORR	single	1	L2-NCORR	high (timur)	
D-L2-19	D19	L2	L2-GAME / L2-NCORR	single	1	L2-GAME	low (barat)	
D-L2-13	D13	L2	L2-NCORR / L2-BALCONY	sliding	1,6	-	-	
D-L2-14	D14	L2	L2-NCORR / L2-BILLIARD	single	1,2	L2-BILLIARD	low (barat)	
D-L2-15	D15	L2	L2-NCORR / L2-GYM	double	1,6	L2-GYM	both (2 daun)	
D-L2-16	D16	L2	L2-NCORR / L2-STORE	single	1	L2-STORE	low (barat)	
D-L2-17	D17	L2	L2-NCORR / L2-RISER	hatch	0,8	-	-	
D-L2-18	D18	L2	L2-NCORR / L2-SERVICE	single	1	L2-SERVICE	low (barat)	

ID jendela	Tag	Lantai	Ruang	Fasad	Lebar m	Ambang m	Kepala m	Kaca
W-L1-001	W1	L1	L1-MEET	S	1,5	0,9	2,4	bening
W-L1-002	W2	L1	L1-MEET	S	1,5	0,9	2,4	bening
W-L1-003	W3	L1	L1-MEET	W	1,5	0,9	2,4	bening
W-L1-004	W4	L1	L1-MEET	W	1,5	0,9	2,4	bening
W-L1-005	W5	L1	L1-LOBBY	S	1,5	0,9	2,4	bening
W-L1-006	W6	L1	L1-LOBBY	S	1,5	0,9	2,4	bening
W-L1-007	W7	L1	L1-PANTRY	S	0,9	1,6	2,4	buram
W-L1-008	W8	L1	L1-WC	E	0,9	1,6	2,4	buram
W-L1-009	W9	L1	L1-WC	E	0,9	1,6	2,4	buram
W-L1-010	W10	L1	L1-WC	E	0,9	1,6	2,4	buram
W-L1-011	W11	L1	L1-DISC	W	1,5	0,9	2,4	bening
W-L1-012	W12	L1	L1-CEO	N	1,5	0,9	2,4	bening
W-L1-013	W13	L1	L1-CEO	N	1,5	0,9	2,4	bening
W-L1-014	W14	L1	L1-HUGO	N	1,5	0,9	2,4	bening
W-L1-015	W15	L1	L1-HUGO	N	1,5	0,9	2,4	bening
W-L1-016	W16	L1	L1-KEVIN	N	1,5	0,9	2,4	bening
W-L1-017	W17	L1	L1-KEVIN	N	1,5	0,9	2,4	bening
W-L1-018	W18	L1	L1-BRUNO	N	1,5	0,9	2,4	bening
W-L1-019	W19	L1	L1-STORE	E	0,9	1,6	2,4	buram
W-L1-020	W20	L1	L1-STORE	E	0,9	1,6	2,4	buram
W-L2-021	W21	L2	L2-READ	S	1,5	0,9	2,4	bening
W-L2-022	W22	L2	L2-READ	S	1,5	0,9	2,4	bening
W-L2-023	W23	L2	L2-LOUNGE	S	1,5	0,9	2,4	bening
W-L2-024	W24	L2	L2-LOUNGE	S	1,5	0,9	2,4	bening
W-L2-025	W25	L2	L2-DINE	S	1,5	0,9	2,4	bening
W-L2-026	W26	L2	L2-DINE	S	1,5	0,9	2,4	bening
W-L2-027	W27	L2	L2-WC	E	0,9	1,6	2,4	buram
W-L2-028	W28	L2	L2-WC	E	0,9	1,6	2,4	buram
W-L2-029	W29	L2	L2-WC	E	0,9	1,6	2,4	buram
W-L2-030	W30	L2	L2-CHAT	W	1,5	0,9	2,4	bening
W-L2-031	W31	L2	L2-CHAT	W	1,5	0,9	2,4	bening
W-L2-032	W32	L2	L2-GAME	E	1,5	0,9	2,4	bening
W-L2-033	W33	L2	L2-BILLIARD	N	1,5	0,9	2,4	bening
W-L2-034	W34	L2	L2-BILLIARD	N	1,5	0,9	2,4	bening
W-L2-035	W35	L2	L2-GYM	N	1,5	0,9	2,4	bening
W-L2-036	W36	L2	L2-STORE	N	0,9	1,6	2,4	buram
W-L2-037	W37	L2	L2-STORE	N	0,9	1,6	2,4	buram
W-L2-038	W38	L2	L2-SERVICE	E	0,9	1,6	2,4	buram
W-L2-039	W39	L2	L2-SERVICE	E	0,9	1,6	2,4	buram

CATATAN SCHEDULE

- 46 pintu/bukaan (34 berdaun, data swing), 39 jendela (13 kaca buram).
- Tag = label di denah, tampak dan potongan. Jendela: W + nomor urut, unik untuk kedua lantai. Pintu: D + kode pintu pada lantainya (denah per lantai).
- Buka ke = ruang tempat daun berayun (swing.into). Engsel low/high = kusen di koordinat lebih kecil/besar sepanjang dinding; arah mata angin dalam kurung.
- Ambang dan kepala dari lantai jadi masing-masing (L1 ±0,00 m, L2 +4,00 m). Fasad S/E/N/W = selatan/timur/utara/barat (Y+ utara).
- Semua jendela konsep; kusen, material dan U-value belum didesain.

STATUS KONSEP

Bukan untuk konstruksi

kantor-rpg Proyek kantor-rpg · gedung KRPg-01

Room schedule, pintu dan jendela

Skala NTS @ A3 lanskap
Revisi P03 · 2026-10-01
Render 2026-10-02 02:42:18 UTC
Halaman 2/2
Digambar Claude Code cloud (generator)
Diperiksa Max (supervisor) belum review
Sumber world.json sha256 488597bb0552fbde

Huruf: Helvetica fallback (Alegreya Sans tidak tersedia saat build).


Nomor lembar

A-103

Rev P03 · 2/2

LAYOUT FURNITURE LANTAI 1 Skala 1:100 @ A2

Angka pada furniture = nomor fixture (FX-L1-nnn tanpa nol depan); ID lengkap di halaman 2. Segi enam Wnn = jendela (schedule A-103).

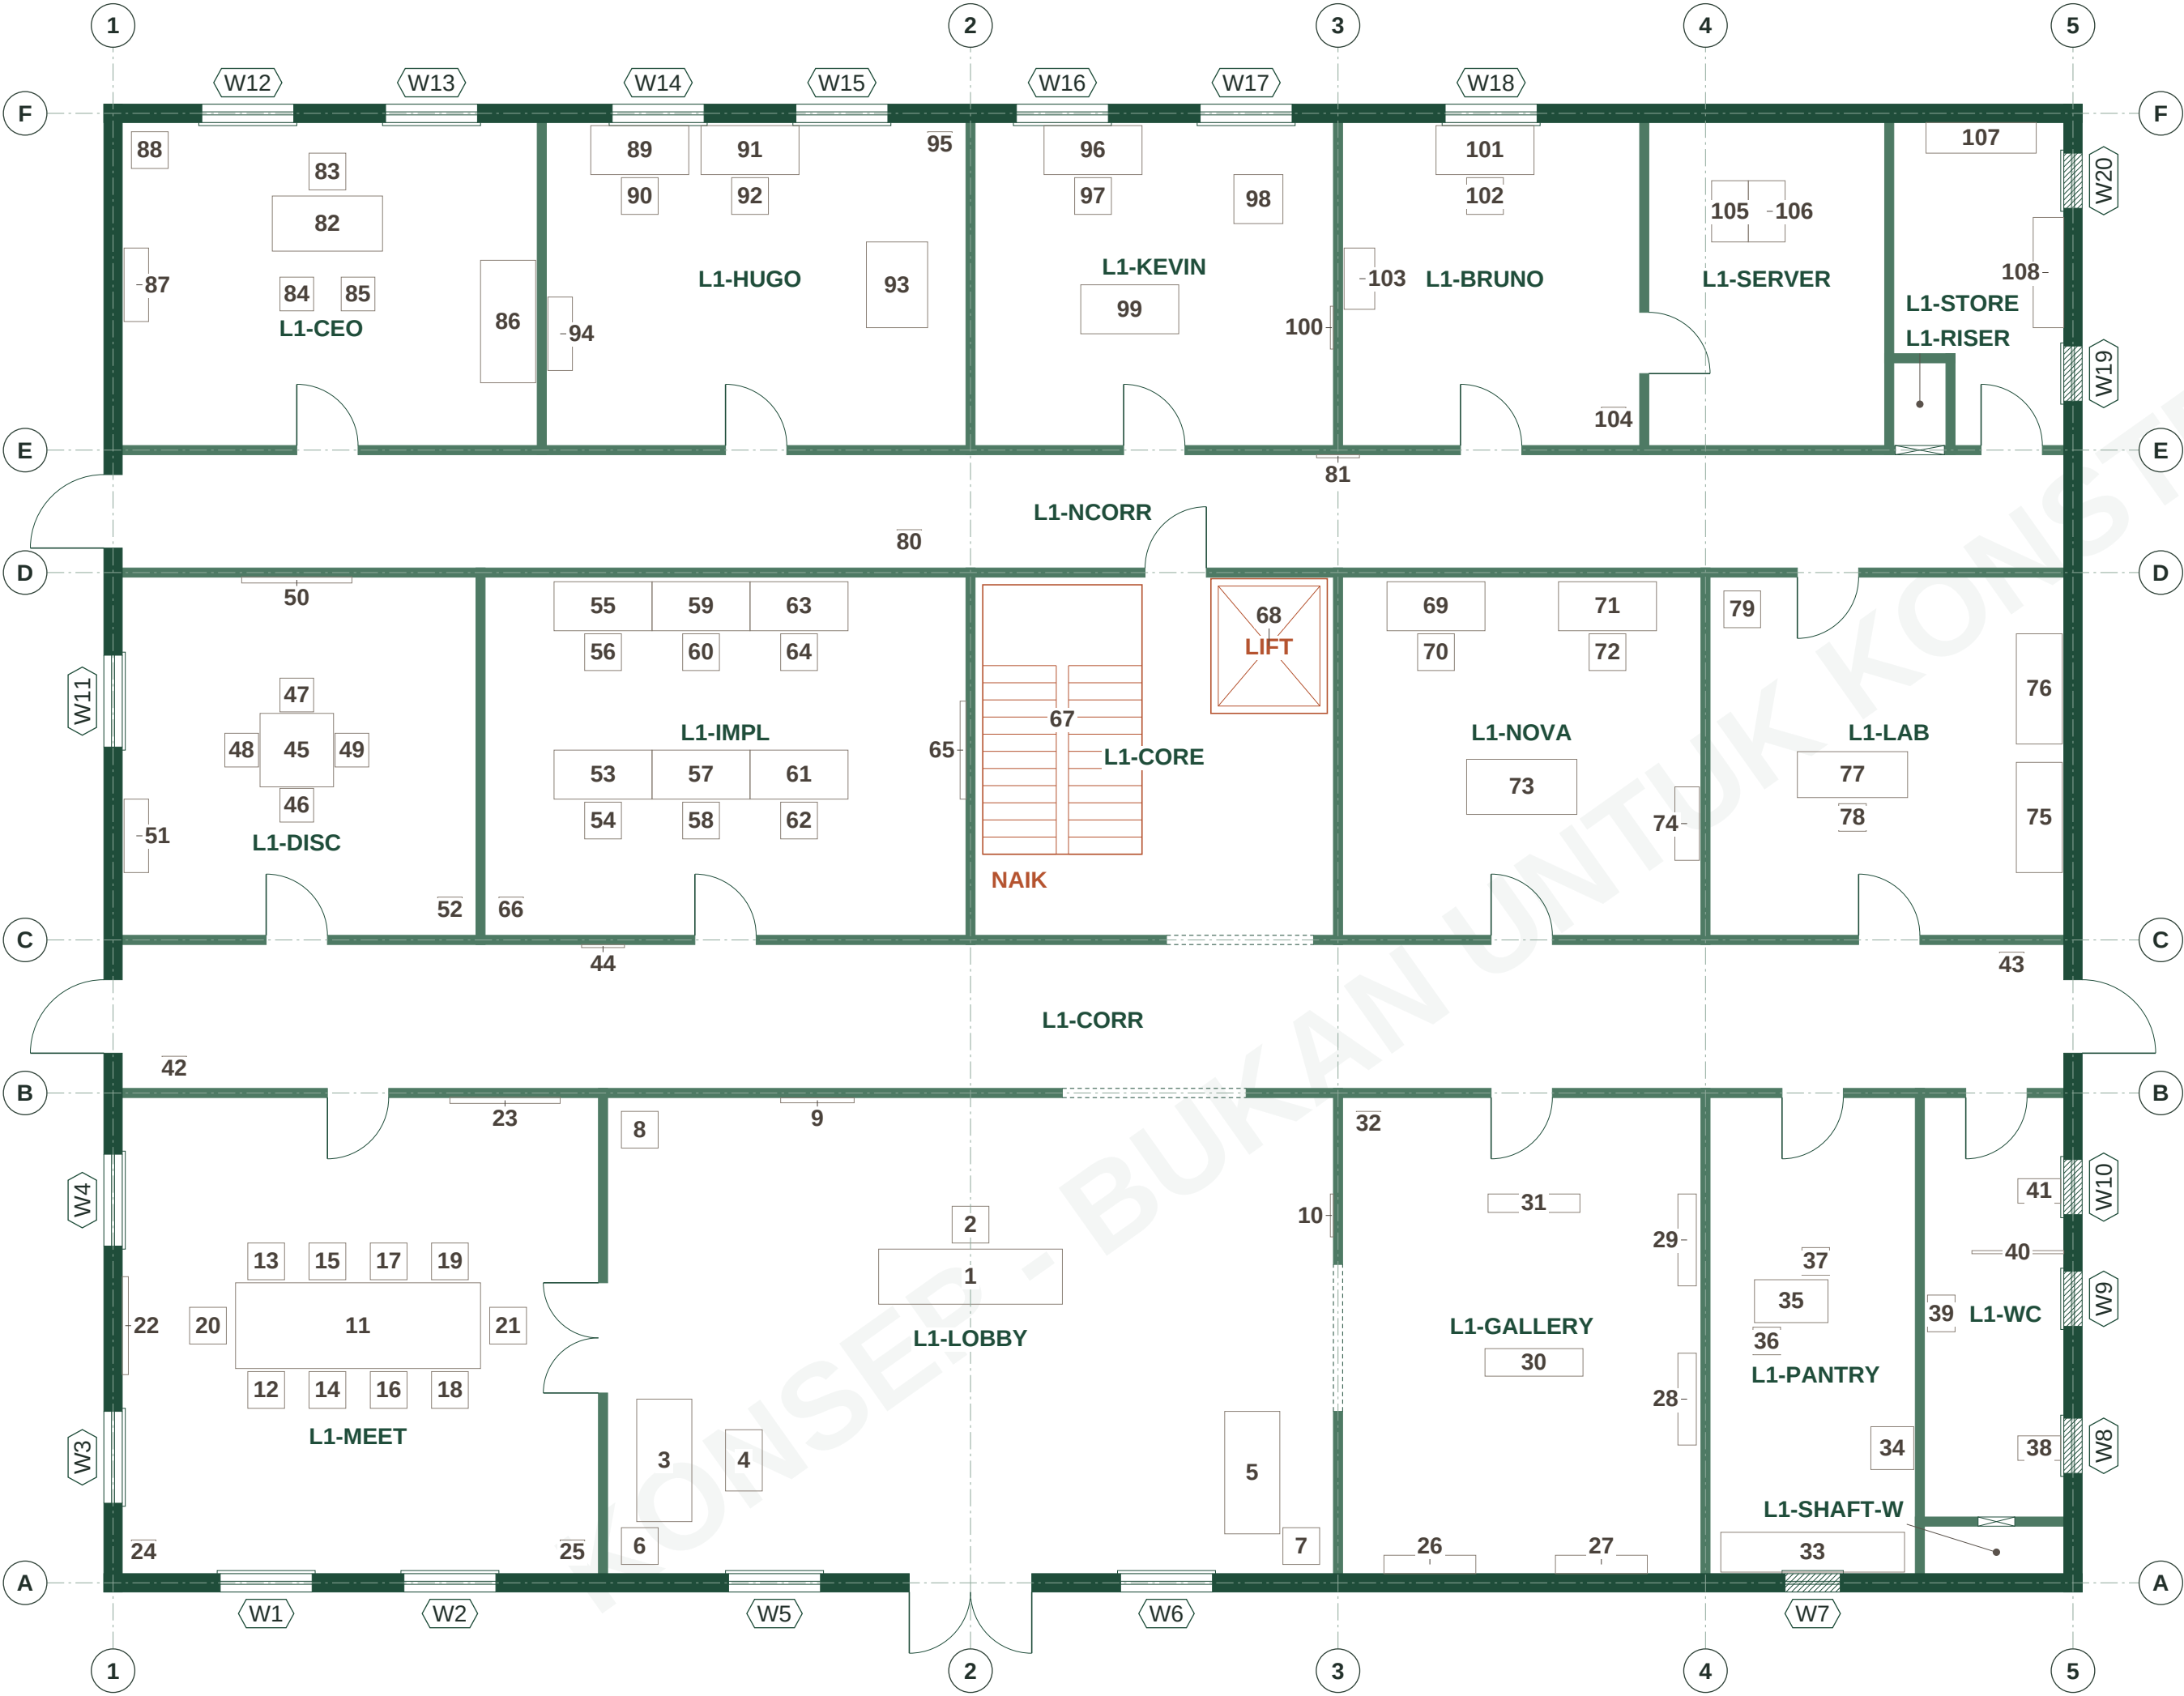

Utara = sumbu Y+ dunia
Lantai L1: Lantai 1 - Kerja & Kunjungan
Ukuran furniture = target catalog (AS-DIM-04).

JENIS FIXTURE (37 jenis, 108 unit)

Jenis (catalog)	Ukuran m	n
Kursi kerja	0,6x0,6	24
Meja kerja + monitor	1,6x0,8	12
Tanaman kecil	0,4x0,4	10
Kursi tamu	0,55x0,55	6
Panel galeri	1,5x0,3	5
Tanaman besar	0,6x0,6	4
Poster/pamflet	0,7x0,05	4
Rak buku	1,2x0,4	3
Meja lab ICT	1,8x0,75	3
Sofa	2x0,9	3
Bangku tinggi	0,45x0,45	3
Rack 42U (target)	0,6x1	2
Rak gudang	1,8x0,5	2
Layar dinding	1,6x0,1	2
Kloset	0,4x0,7	2
Papan tulis	1,8x0,1	2
Bangku	1,6x0,45	1
Meja kopi	1x0,6	1
Meja CEO	1,8x0,9	1
Papan direktori	1,2x0,08	1
Meja gambar	1,4x1	1
Easel	0,8x0,8	1
Kulkas	0,7x0,7	1
Meja tinggi	1,2x0,7	1
Rack lab terbuka 12U	0,6x0,6	1
Lift (konsep)	1,9x2,2	1
Meja rapat	4x1,4	1
Rak model	1,2x0,4	1
Counter pantry	3x0,65	1
Partisi bilik	1,5x0,05	1
Meja denah (blueprint)	1,8x0,9	1
Meja resepsi	3x0,9	1
Meja bundar	1,2x1,2	1
Wastafel	0,6x0,45	1
Tangga U (konsep)	2,6x4,4	1
Lemari alat	1x0,5	1
Meja kerja berdiri	1,6x0,8	1

Nomor kunci per fixture dan ruangnya: halaman 2.

STATUS KONSEP

Bukan untuk konstruksi

kantor-rpg Proyek kantor-rpg · gedung KRPG-01
Layout furniture Lantai 1

Skala 1:100 @ A2 lanskap
Revisi P03 · 2026-10-01
Render 2026-10-02 02:42:18 UTC
Halaman 1/2
Digambar Claude Code cloud (generator)
Diperiksa Max (supervisor) belum review
Sumber world.json sha256 488597bb0552fbde
Huruf: Helvetica fallback (Alegreya Sans tidak tersedia saat build).

Nomor lembar

A-201

Rev P03 · 1/2

No ID	Jenis	Ruang
1 FX-L1-001	Meja resepsi	LOBBY
2 FX-L1-002	Kursi kerja	LOBBY
3 FX-L1-003	Sofa	LOBBY
4 FX-L1-004	Meja kopi	LOBBY
5 FX-L1-005	Sofa	LOBBY
6 FX-L1-006	Tanaman besar	LOBBY
7 FX-L1-007	Tanaman besar	LOBBY
8 FX-L1-008	Tanaman besar	LOBBY
9 FX-L1-009	Papan direktori	LOBBY
10 FX-L1-010	Poster/pamflet	LOBBY
11 FX-L1-011	Meja rapat	MEET
12 FX-L1-012	Kursi kerja	MEET
13 FX-L1-013	Kursi kerja	MEET
14 FX-L1-014	Kursi kerja	MEET
15 FX-L1-015	Kursi kerja	MEET
16 FX-L1-016	Kursi kerja	MEET
17 FX-L1-017	Kursi kerja	MEET
18 FX-L1-018	Kursi kerja	MEET
19 FX-L1-019	Kursi kerja	MEET
20 FX-L1-020	Kursi kerja	MEET
21 FX-L1-021	Kursi kerja	MEET
22 FX-L1-022	Layar dinding	MEET
23 FX-L1-023	Papan tulis	MEET
24 FX-L1-024	Tanaman kecil	MEET
25 FX-L1-025	Tanaman kecil	MEET
26 FX-L1-026	Panel galeri	GALLERY
27 FX-L1-027	Panel galeri	GALLERY

No ID	Jenis	Ruang
28 FX-L1-028	Panel galeri	GALLERY
29 FX-L1-029	Panel galeri	GALLERY
30 FX-L1-030	Bangku	GALLERY
31 FX-L1-031	Panel galeri	GALLERY
32 FX-L1-032	Tanaman kecil	GALLERY
33 FX-L1-033	Counter pantry	PANTRY
34 FX-L1-034	Kulkas	PANTRY
35 FX-L1-035	Meja tinggi	PANTRY
36 FX-L1-036	Bangku tinggi	PANTRY
37 FX-L1-037	Bangku tinggi	PANTRY
38 FX-L1-038	Kloset	WC
39 FX-L1-039	Wastafel	WC
40 FX-L1-040	Partisi bilik	WC
41 FX-L1-041	Kloset	WC
42 FX-L1-042	Tanaman kecil	CORR
43 FX-L1-043	Tanaman kecil	CORR
44 FX-L1-044	Poster/pamflet	CORR
45 FX-L1-045	Meja bundar	DISC
46 FX-L1-046	Kursi tamu	DISC
47 FX-L1-047	Kursi tamu	DISC
48 FX-L1-048	Kursi tamu	DISC
49 FX-L1-049	Kursi tamu	DISC
50 FX-L1-050	Papan tulis	DISC
51 FX-L1-051	Rak buku	DISC
52 FX-L1-052	Tanaman kecil	DISC
53 FX-L1-053	Meja kerja + monitor	IMPL
54 FX-L1-054	Kursi kerja	IMPL

No ID	Jenis	Ruang
55 FX-L1-055	Meja kerja + monitor	IMPL
56 FX-L1-056	Kursi kerja	IMPL
57 FX-L1-057	Meja kerja + monitor	IMPL
58 FX-L1-058	Kursi kerja	IMPL
59 FX-L1-059	Meja kerja + monitor	IMPL
60 FX-L1-060	Kursi kerja	IMPL
61 FX-L1-061	Meja kerja + monitor	IMPL
62 FX-L1-062	Kursi kerja	IMPL
63 FX-L1-063	Meja kerja + monitor	IMPL
64 FX-L1-064	Kursi kerja	IMPL
65 FX-L1-065	Layar dinding	IMPL
66 FX-L1-066	Tanaman kecil	IMPL
67 FX-L1-067	Tangga U (konsep)	CORE
68 FX-L1-068	Lift (konsep)	CORE
69 FX-L1-069	Meja kerja + monitor	NOVA
70 FX-L1-070	Kursi kerja	NOVA
71 FX-L1-071	Meja kerja + monitor	NOVA
72 FX-L1-072	Kursi kerja	NOVA
73 FX-L1-073	Meja denah (blueprint)	NOVA
74 FX-L1-074	Rak buku	NOVA
75 FX-L1-075	Meja lab ICT	LAB
76 FX-L1-076	Meja lab ICT	LAB
77 FX-L1-077	Meja lab ICT	LAB
78 FX-L1-078	Bangku tinggi	LAB
79 FX-L1-079	Rack lab terbuka 12U	LAB
80 FX-L1-080	Tanaman kecil	NCORR
81 FX-L1-081	Poster/pamflet	NCORR

No ID	Jenis	Ruang
82 FX-L1-082	Meja CEO	CEO
83 FX-L1-083	Kursi kerja	CEO
84 FX-L1-084	Kursi tamu	CEO
85 FX-L1-085	Kursi tamu	CEO
86 FX-L1-086	Sofa	CEO
87 FX-L1-087	Rak buku	CEO
88 FX-L1-088	Tanaman besar	CEO
89 FX-L1-089	Meja kerja + monitor	HUGO
90 FX-L1-090	Kursi kerja	HUGO
91 FX-L1-091	Meja kerja + monitor	HUGO
92 FX-L1-092	Kursi kerja	HUGO
93 FX-L1-093	Meja gambar	HUGO
94 FX-L1-094	Rak model	HUGO
95 FX-L1-095	Tanaman kecil	HUGO
96 FX-L1-096	Meja kerja + monitor	KEVIN
97 FX-L1-097	Kursi kerja	KEVIN
98 FX-L1-098	Easel	KEVIN
99 FX-L1-099	Meja kerja berdiri	KEVIN
100 FX-L1-100	Poster/pamflet	KEVIN
101 FX-L1-101	Meja kerja + monitor	BRUNO
102 FX-L1-102	Kursi kerja	BRUNO
103 FX-L1-103	Lemari alat	BRUNO
104 FX-L1-104	Tanaman kecil	BRUNO
105 FX-L1-105	Rack 42U (target)	SERVER
106 FX-L1-106	Rack 42U (target)	SERVER
107 FX-L1-107	Rak gudang	STORE
108 FX-L1-108	Rak gudang	STORE

STATUS KONSEP

Bukan untuk konstruksi

kantor-rpg
Proyek kantor-rpg · gedung KRPG-01

Layout furniture Lantai 1

Skala1:100 @ A2 lanskap
RevisiP03 · 2026-10-01
Render2026-10-02 02:42:18 UTC
Halaman2/2
DigambarClaude Code cloud (generator)
DiperiksaMax (supervisor) belum review
Sumberworld.json sha256 488597bb0552fbde
Huruf: Helvetica fallback (Alegreya Sans tidak tersedia saat build).

Nomor lembar

A-201

Rev P03 · 2/2



Utara = sumbu Y+ dunia
Lantai L2: Lantai 2 - Rekreasi
Ukuran furniture = target catalog (AS-DIM-04).

JENIS FIXTURE (37 jenis, 91 unit)

Jenis (catalog)	Ukuran m	n
Kursi kerja	0,6x0,6	8
Beanbag	0,8x0,8	6
Planter	1,6x0,6	6
Bangku tinggi	0,45x0,45	6
Kursi santai	0,9x0,9	5
Bangku	1,6x0,45	5
Tanaman kecil	0,4x0,4	4
Rak buku	1,2x0,4	3
Meja kopi	1x0,6	3
Bilik shower	0,9x0,9	3
Sofa	2x0,9	3
Rak gudang	1,8x0,5	3
Layar dinding	1,6x0,1	3
Kabinet arcade	0,75x0,85	2
Meja makan	1,8x0,9	2
Matras	1,8x0,6	2
Konsol game + layar	2x0,5	2
Tanaman besar	0,6x0,6	2
Poster/pamflet	0,7x0,05	2
Wastafel	0,6x0,45	2
Treadmill	0,9x2	2
Kloset	0,4x0,7	2
Meja biliar 9 ft	2,84x1,57	1
Meja board game	1,2x1,2	1
Coffee bar	2,4x0,6	1
Rak stik	0,6x0,12	1
Rak dumbbell	1,2x0,5	1
Sepeda statis	0,6x1,2	1
Kulkas	0,7x0,7	1
Meja tinggi	1,2x0,7	1
Lift (konsep)	1,9x2,2	1
Loker	1,2x0,5	1
Counter pantry	3x0,65	1
Partisi bilik	1,5x0,05	1
Meja bundar	1,2x1,2	1
Tangga U (konsep)	2,6x4,4	1
Pohon dalam pot	1,2x1,2	1

Nomor kunci per fixture dan ruangnya: halaman 2.

STATUS KONSEP

Bukan untuk konstruksi

kantor-rpg Proyek kantor-rpg · gedung KRPG-01

Layout furniture Lantai 2

Skala 1:100 @ A2 lanskap
Revisi P03 · 2026-10-01
Render 2026-10-02 02:42:18 UTC
Halaman 1/2
Digambar Claude Code cloud (generator)
Diperiksa Max (supervisor) belum review
Sumber world.json sha256 488597bb0552fbde
Huruf: Helvetica fallback (Alegreya Sans tidak tersedia saat build).


Nomor lembar

A-202

Rev P03 · 1/2

LAYOUT FURNITURE LANTAI 2 Skala 1:100 @ A2

Angka pada furniture = nomor fixture (FX-L2-nnn tanpa nol depan); ID lengkap di halaman 2. Segi enam Wnn = jendela (schedule A-103).

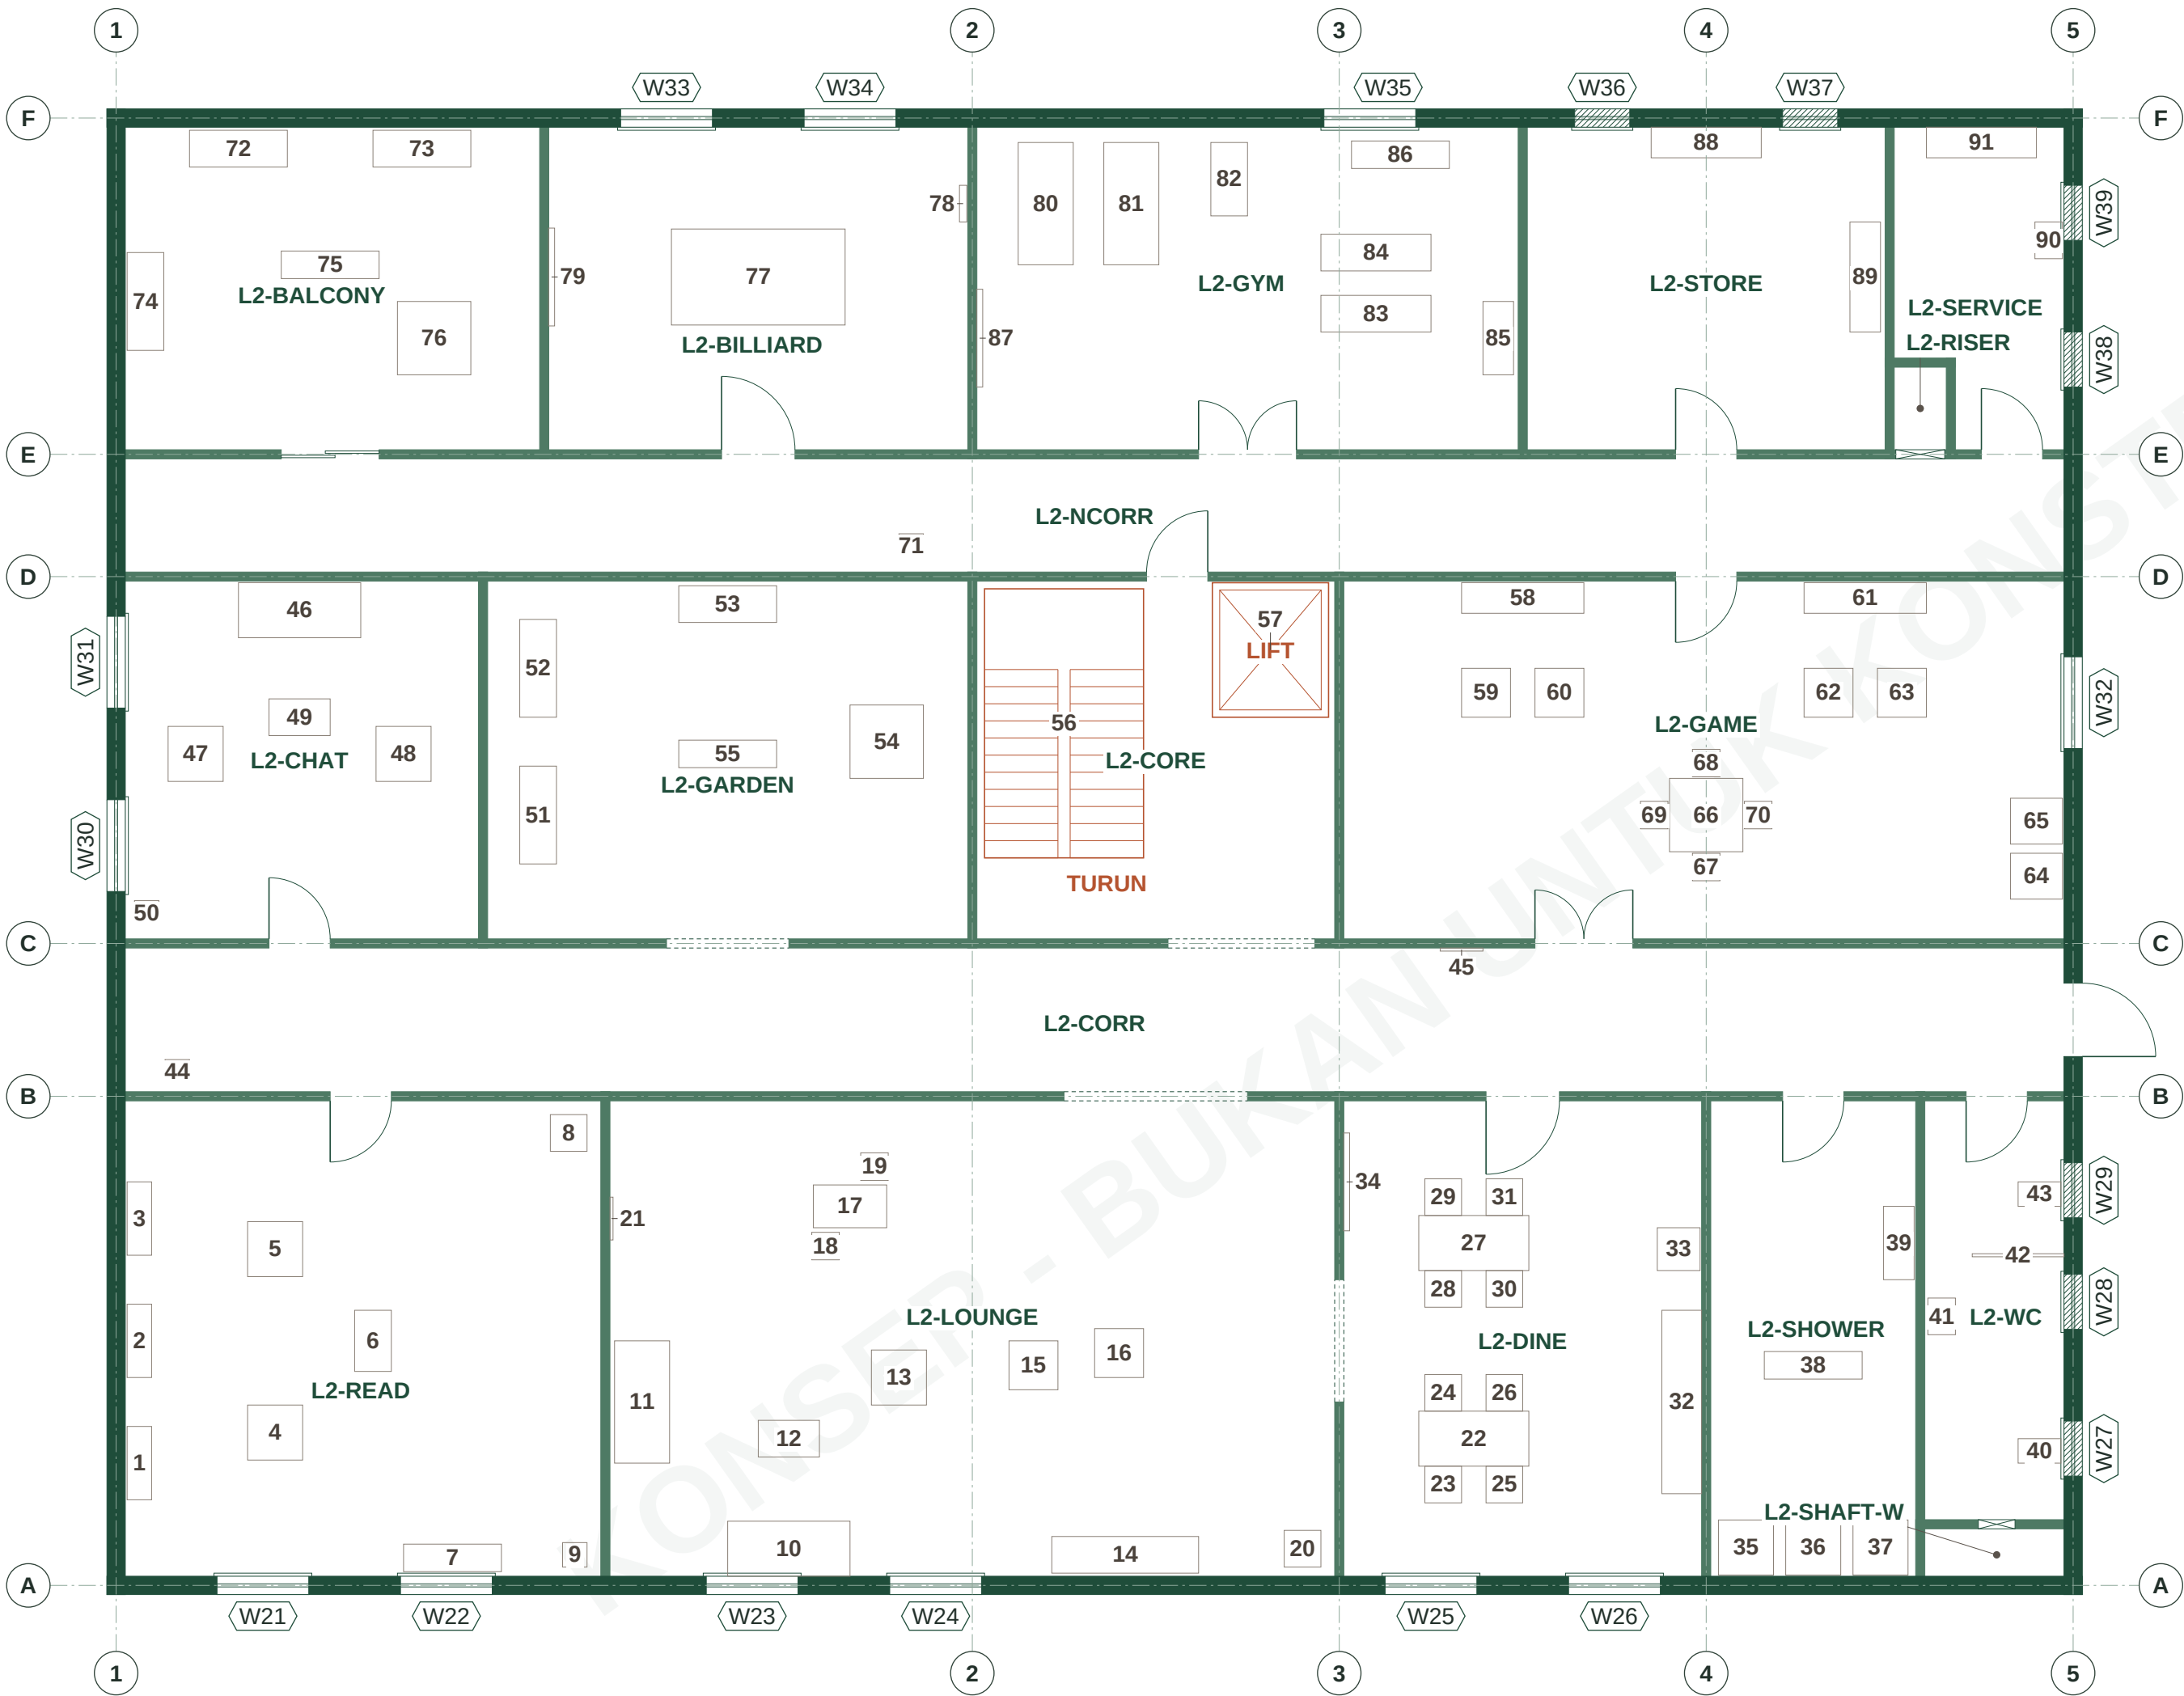

No ID	Jenis	Ruang
1 FX-L2-001	Rak buku	READ
2 FX-L2-002	Rak buku	READ
3 FX-L2-003	Rak buku	READ
4 FX-L2-004	Kursi santai	READ
5 FX-L2-005	Kursi santai	READ
6 FX-L2-006	Meja kopi	READ
7 FX-L2-007	Bangku	READ
8 FX-L2-008	Tanaman besar	READ
9 FX-L2-009	Tanaman kecil	READ
10 FX-L2-010	Sofa	LOUNGE
11 FX-L2-011	Sofa	LOUNGE
12 FX-L2-012	Meja kopi	LOUNGE
13 FX-L2-013	Kursi santai	LOUNGE
14 FX-L2-014	Coffee bar	LOUNGE
15 FX-L2-015	Beanbag	LOUNGE
16 FX-L2-016	Beanbag	LOUNGE
17 FX-L2-017	Meja tinggi	LOUNGE
18 FX-L2-018	Bangku tinggi	LOUNGE
19 FX-L2-019	Bangku tinggi	LOUNGE
20 FX-L2-020	Tanaman besar	LOUNGE
21 FX-L2-021	Poster/pamflet	LOUNGE
22 FX-L2-022	Meja makan	DINE
23 FX-L2-023	Kursi kerja	DINE

No ID	Jenis	Ruang
24 FX-L2-024	Kursi kerja	DINE
25 FX-L2-025	Kursi kerja	DINE
26 FX-L2-026	Kursi kerja	DINE
27 FX-L2-027	Meja makan	DINE
28 FX-L2-028	Kursi kerja	DINE
29 FX-L2-029	Kursi kerja	DINE
30 FX-L2-030	Kursi kerja	DINE
31 FX-L2-031	Kursi kerja	DINE
32 FX-L2-032	Counter pantry	DINE
33 FX-L2-033	Kulkas	DINE
34 FX-L2-034	Layar dinding	DINE
35 FX-L2-035	Bilik shower	SHOWER
36 FX-L2-036	Bilik shower	SHOWER
37 FX-L2-037	Bilik shower	SHOWER
38 FX-L2-038	Bangku	SHOWER
39 FX-L2-039	Loker	SHOWER
40 FX-L2-040	Kloset	WC
41 FX-L2-041	Wastafel	WC
42 FX-L2-042	Partisi bilik	WC
43 FX-L2-043	Kloset	WC
44 FX-L2-044	Tanaman kecil	CORR
45 FX-L2-045	Poster/pamflet	CORR
46 FX-L2-046	Sofa	CHAT

No ID	Jenis	Ruang
47 FX-L2-047	Kursi santai	CHAT
48 FX-L2-048	Kursi santai	CHAT
49 FX-L2-049	Meja kopi	CHAT
50 FX-L2-050	Tanaman kecil	CHAT
51 FX-L2-051	Planter	GARDEN
52 FX-L2-052	Planter	GARDEN
53 FX-L2-053	Planter	GARDEN
54 FX-L2-054	Pohon dalam pot	GARDEN
55 FX-L2-055	Bangku	GARDEN
56 FX-L2-056	Tangga U (konsep)	CORE
57 FX-L2-057	Lift (konsep)	CORE
58 FX-L2-058	Konsol game + layar	GAME
59 FX-L2-059	Beanbag	GAME
60 FX-L2-060	Beanbag	GAME
61 FX-L2-061	Konsol game + layar	GAME
62 FX-L2-062	Beanbag	GAME
63 FX-L2-063	Beanbag	GAME
64 FX-L2-064	Kabinet arcade	GAME
65 FX-L2-065	Kabinet arcade	GAME
66 FX-L2-066	Meja board game	GAME
67 FX-L2-067	Bangku tinggi	GAME
68 FX-L2-068	Bangku tinggi	GAME
69 FX-L2-069	Bangku tinggi	GAME

No ID	Jenis	Ruang
70 FX-L2-070	Bangku tinggi	GAME
71 FX-L2-071	Tanaman kecil	NCORR
72 FX-L2-072	Planter	BALCONY
73 FX-L2-073	Planter	BALCONY
74 FX-L2-074	Planter	BALCONY
75 FX-L2-075	Bangku	BALCONY
76 FX-L2-076	Meja bundar	BALCONY
77 FX-L2-077	Meja biliar 9 ft	BILLIARD
78 FX-L2-078	Rak stik	BILLIARD
79 FX-L2-079	Layar dinding	BILLIARD
80 FX-L2-080	Treadmill	GYM
81 FX-L2-081	Treadmill	GYM
82 FX-L2-082	Sepeda statis	GYM
83 FX-L2-083	Matras	GYM
84 FX-L2-084	Matras	GYM
85 FX-L2-085	Rak dumbbell	GYM
86 FX-L2-086	Bangku	GYM
87 FX-L2-087	Layar dinding	GYM
88 FX-L2-088	Rak gudang	STORE
89 FX-L2-089	Rak gudang	STORE
90 FX-L2-090	Wastafel	SERVICE
91 FX-L2-091	Rak gudang	SERVICE

STATUS KONSEP

Bukan untuk konstruksi

kantor-rpg
Proyek kantor-rpg · gedung KRPG-01

Layout furniture Lantai 2


Skala1:100 @ A2 lanskap
RevisiP03 · 2026-10-01
Render2026-10-02 02:42:18 UTC
Halaman2/2
DigambarClaude Code cloud (generator)
DiperiksaMax (supervisor) belum review
Sumberworld.json sha256 488597bb0552fbde
Huruf: Helvetica fallback (Alegreya Sans tidak tersedia saat build).

Nomor lembar

A-202


Rev P03 · 2/2

TAMPAK SELATAN 1:200

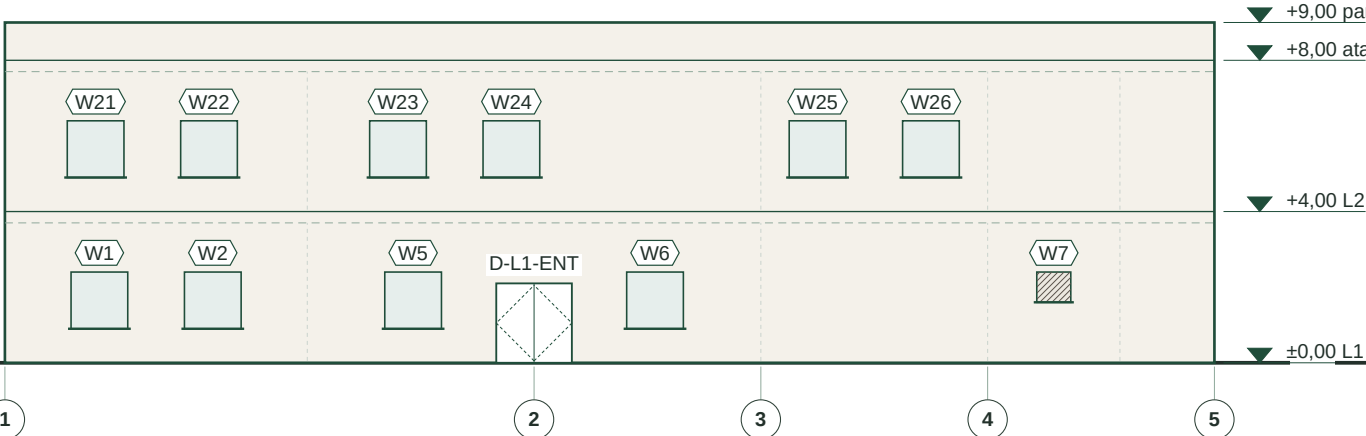


Panjang fasad 32 m, as ke as dinding luar.

TAMPAK UTARA 1:200

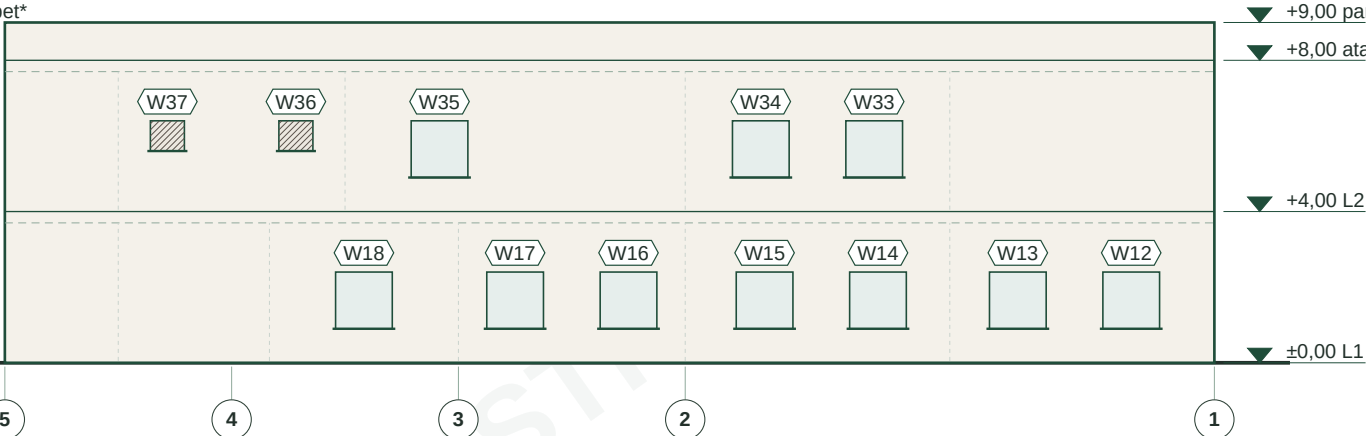


Panjang fasad 32 m, as ke as dinding luar.

TAMPAK TIMUR 1:200

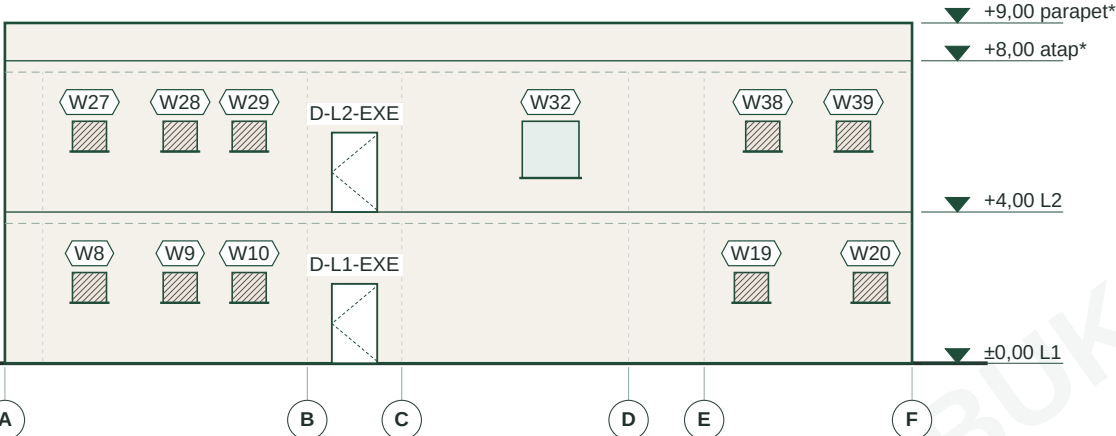

Panjang fasad 24 m, as ke as dinding luar.

TAMPAK BARAT 1:200

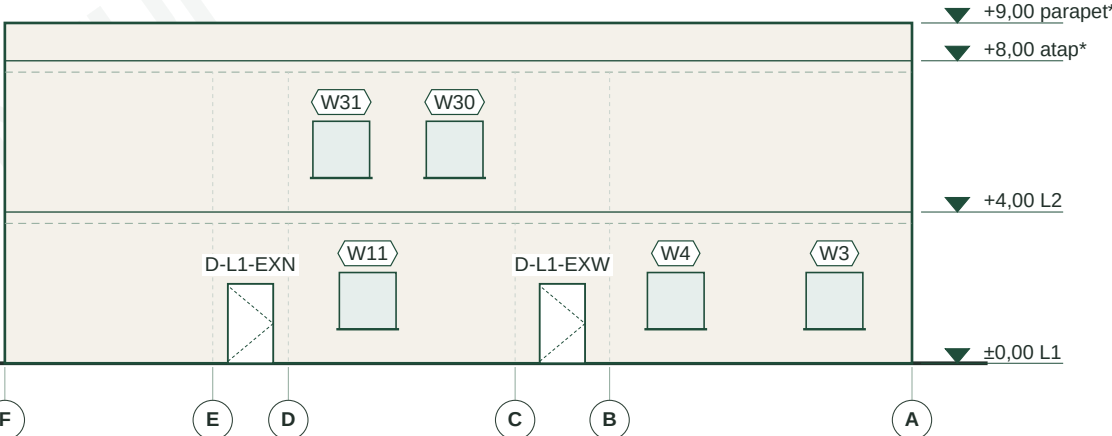

Panjang fasad 24 m, as ke as dinding luar.

CATATAN TAMPAK

- Tinggi antar lantai 4 m dan pelat 0,3 m dari world.json (AS-DIM-01, AS-DIM-03).
- * Atap dan parapet 1 m serta tinggi pintu 2,1 m adalah asumsi lembar ini (konsep); tidak ada di world.json.
- Jendela dari world.json windows (39 buah): posisi, lebar, ambang dan kepala per lantai; kaca buram diarsir. Kusen dan material fasad belum didesain.
- Tag segi enam Wnn = jendela nomor nn (W16 = W-L1-016); pasangan tag dan ID lengkap di schedule A-103 halaman 2.
- Segitiga putus pada pintu = sisi engsel (puncak segitiga) dari doors[].swing.hinge.
- Garis putus tipis = posisi dinding dalam yang bertemu fasad; garis putus abu = pelat tersembunyi.
- Pintu exit L2 timur menuju tangga darurat konsep VL-ESC-E di luar envelope (AS-EXIT-01), tidak digambar.



STATUS KONSEP

Bukan untuk konstruksi

kantor-rpg Proyek kantor-rpg · gedung KRPg-01

Tampak



Skala 1:200 @ A3 lanskap
Revisi P03 · 2026-10-01
Render 2026-10-02 02:42:18 UTC
Halaman 1/1
Digambar Claude Code cloud (generator)
Diperiksa Max (supervisor) belum review
Sumber world.json sha256 488597bb0552fbde

Huruf: Helvetica fallback (Alegreya Sans tidak tersedia saat build).


Nomor lembar

A-301

Rev P03 · 1/1

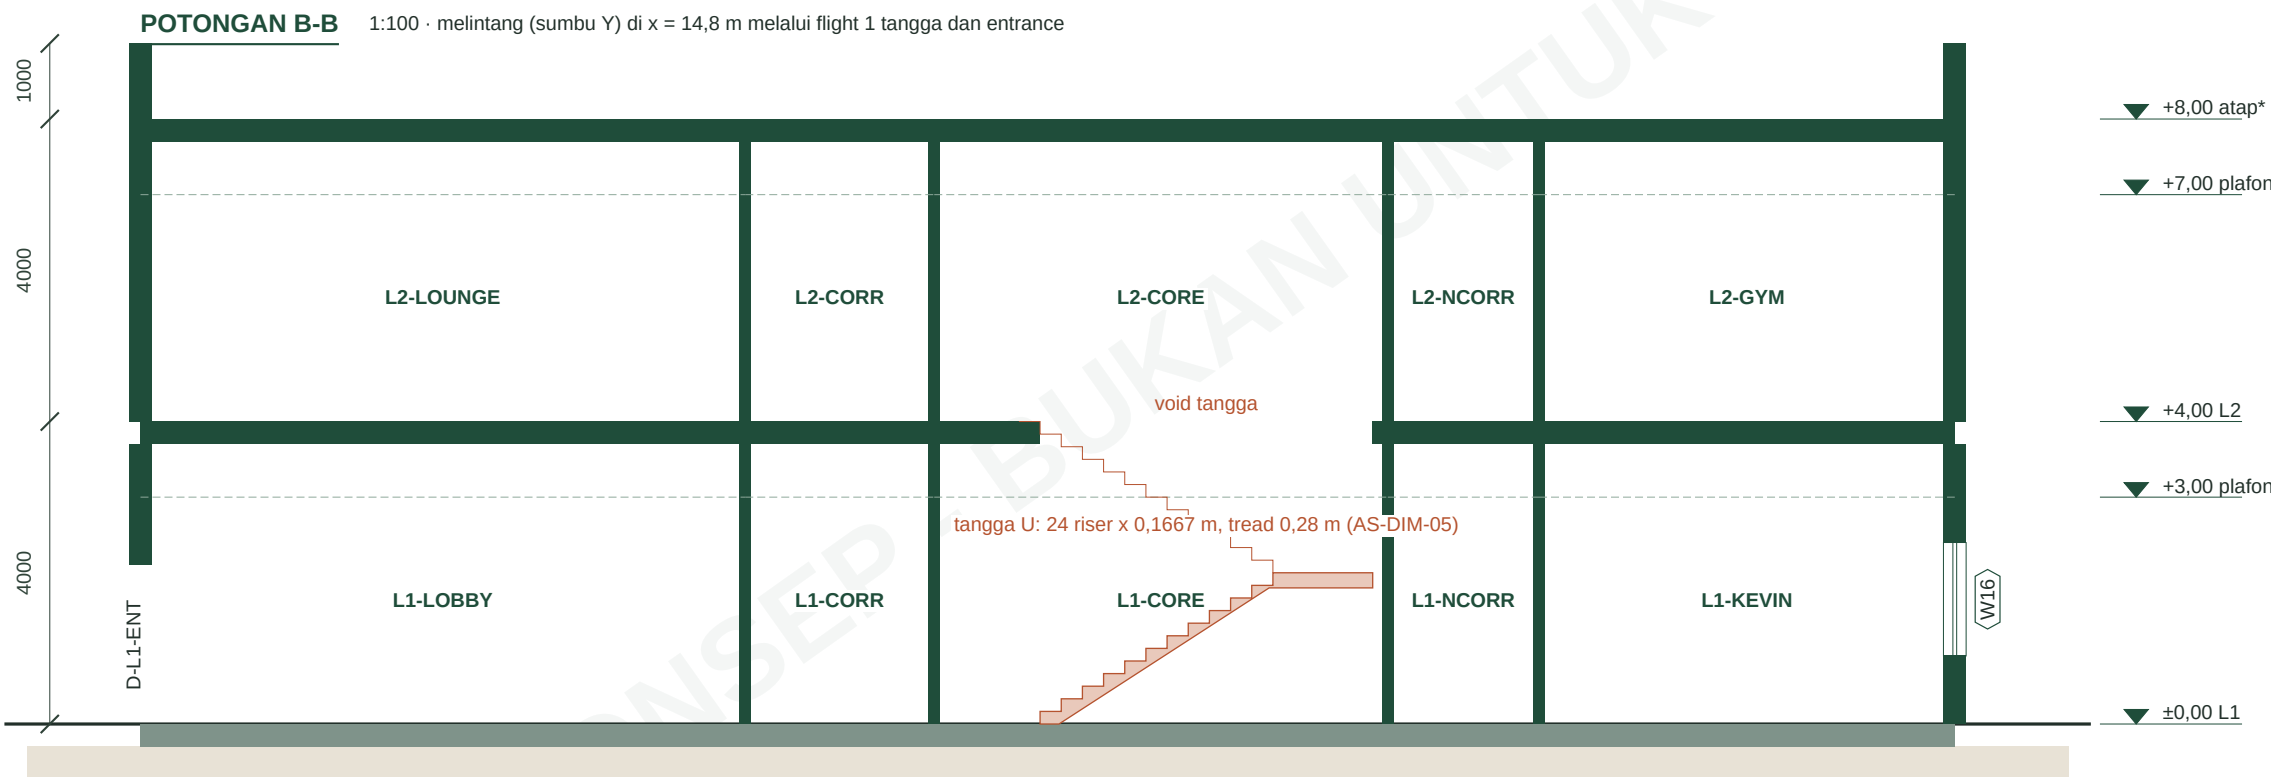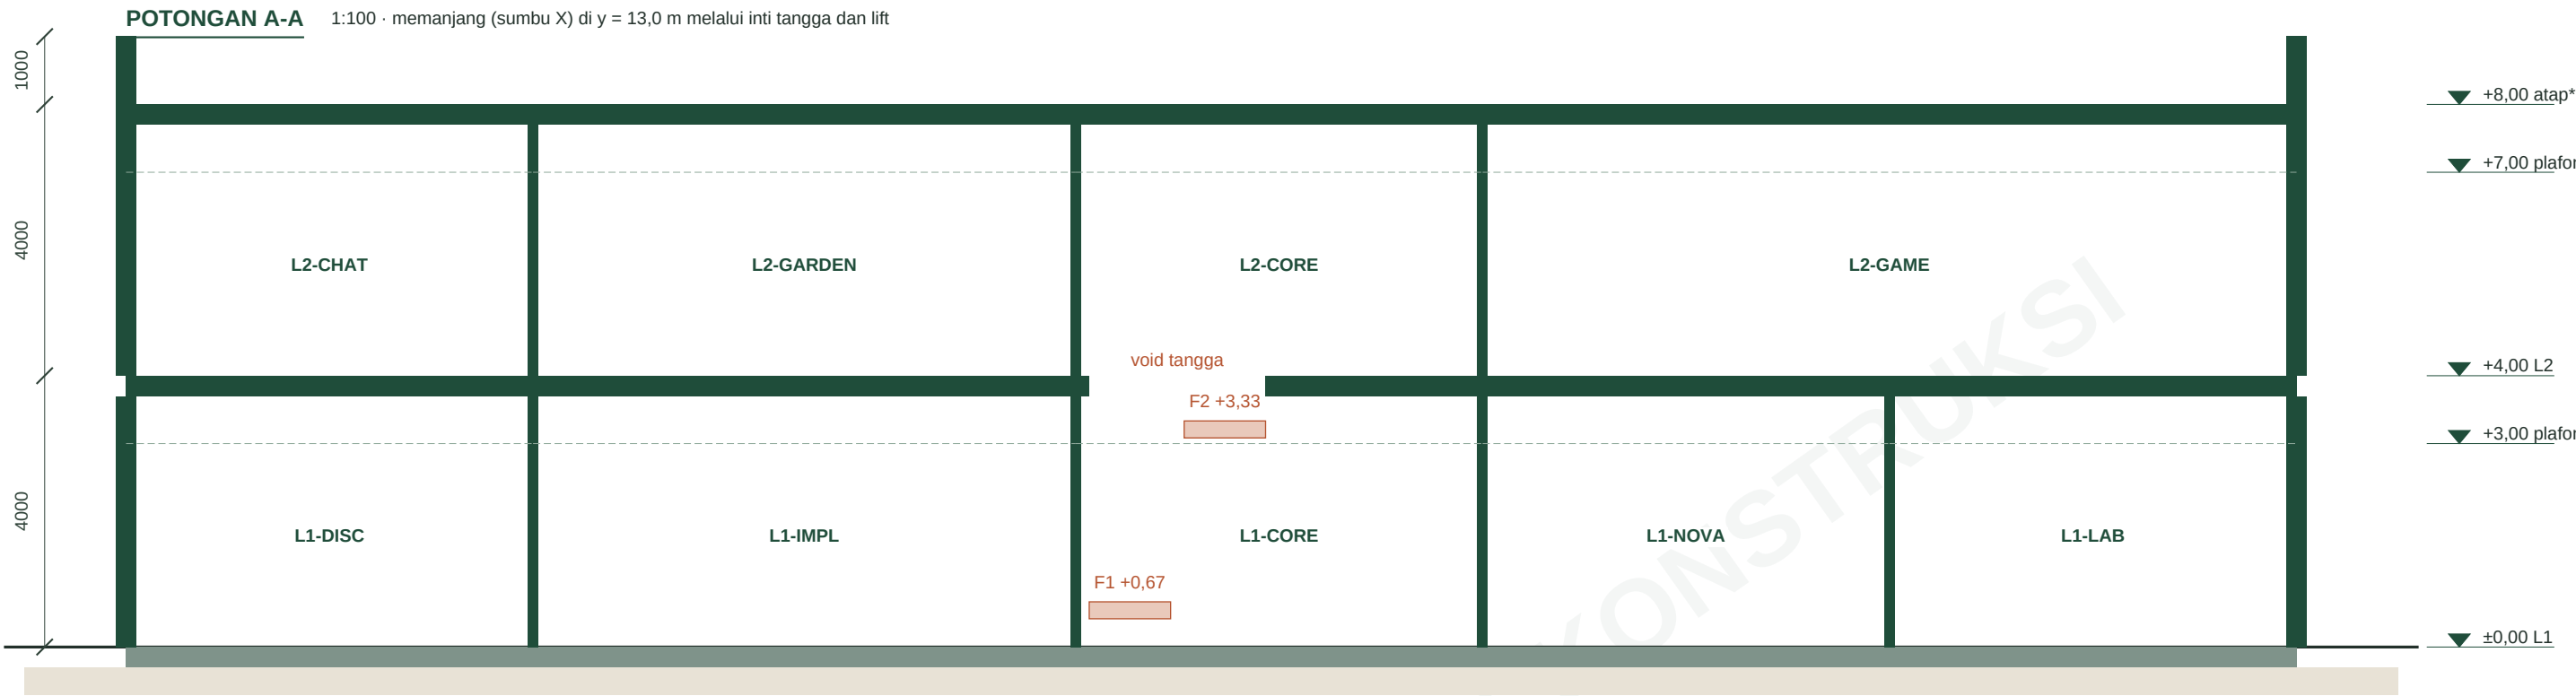

KUNCI POTONGAN L1 (1:500)

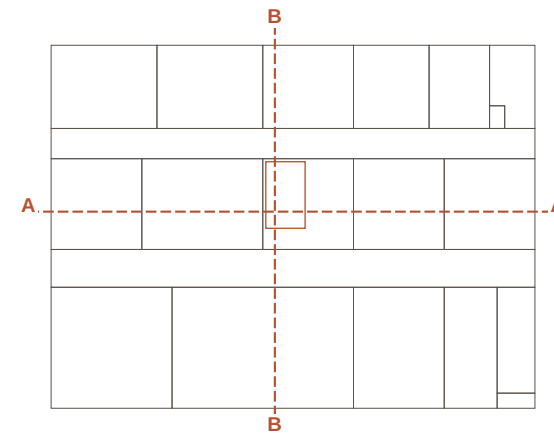

- Diturunkan dari world.json: tinggi antar lantai 4 m, plafon 3 m, pelat 0,3 m (AS-DIM-03); dinding dan bukaan dari derive_walls; tangga dari fixture stair_u (AS-DIM-05).
- Tinggi kepala pintu 2,1 m, parapet 1 m dan * atap konsep adalah asumsi lembar, bukan data world.json. Belum ada desain struktur atau fondasi.
- Hijau penuh = elemen terpotong (dinding, pelat). Garis putus = plafon. Terakota = tangga.
- Jendela yang terpotong garis potong digambar dengan ambang dan kepala dari world.json windows: W-L1-016 (tag W16).

STATUS KONSEP

Bukan untuk konstruksi

kantor-rpg Proyek kantor-rpg · gedung KRPg-01

Potongan


Skala 1:100 @ A3 lanskap
Revisi P03 · 2026-10-01
Render 2026-10-02 02:42:18 UTC
Halaman 1/1
Digambar Claude Code cloud (generator)
Diperiksa Max (supervisor) belum review
Sumber world.json sha256 488597bb0552fbde
Huruf: Helvetica fallback (Alegreya Sans tidak tersedia saat build).

Nomor lembar


A-401

Rev P03 · 1/1

FINISH LANTAI L11:200 · Lantai 1 - Kerja & Kunjungan

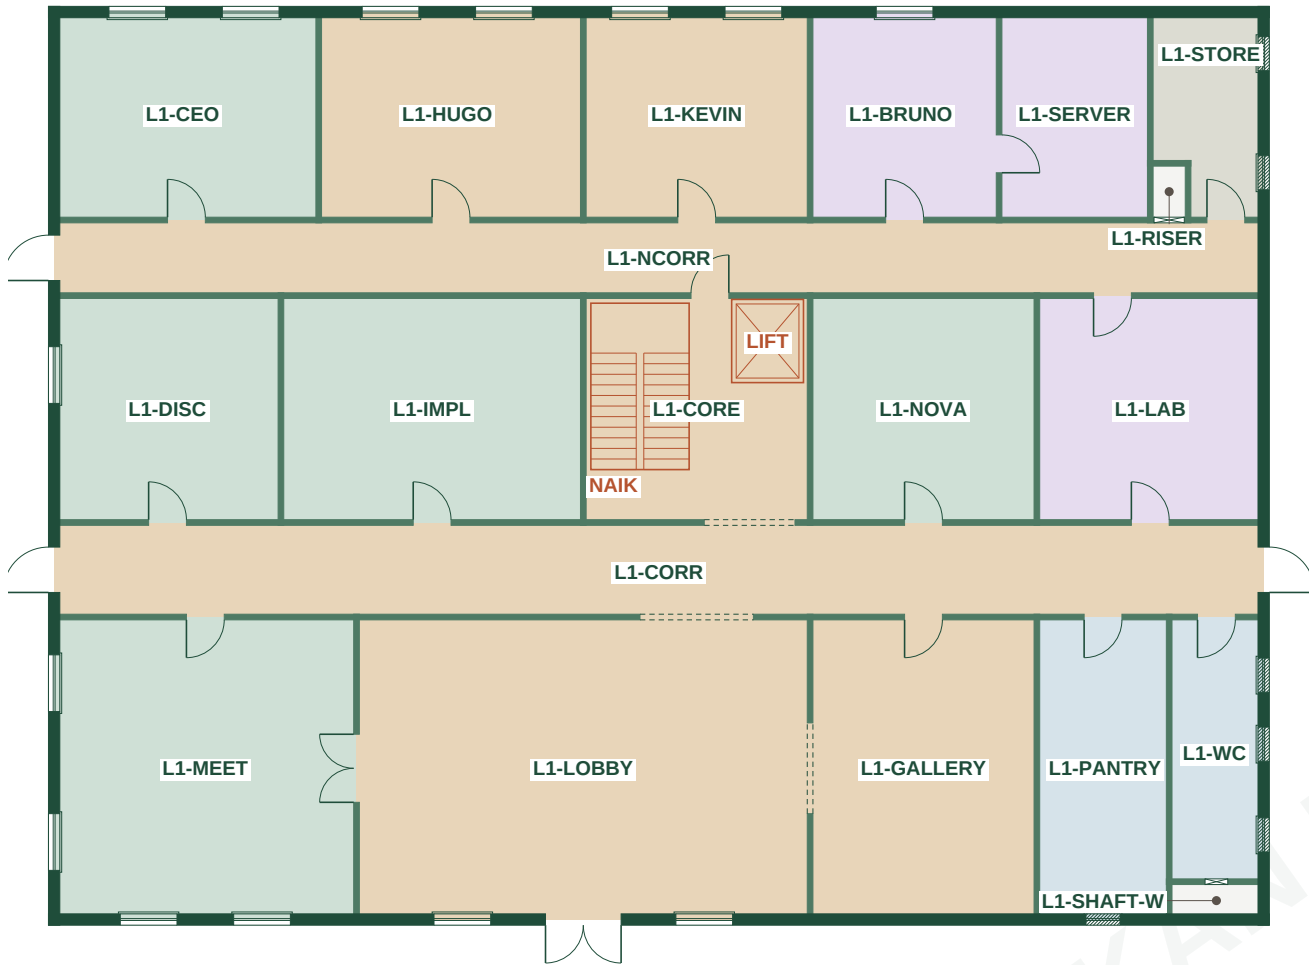

FINISH LANTAI L21:200 · Lantai 2 - Rekreasi

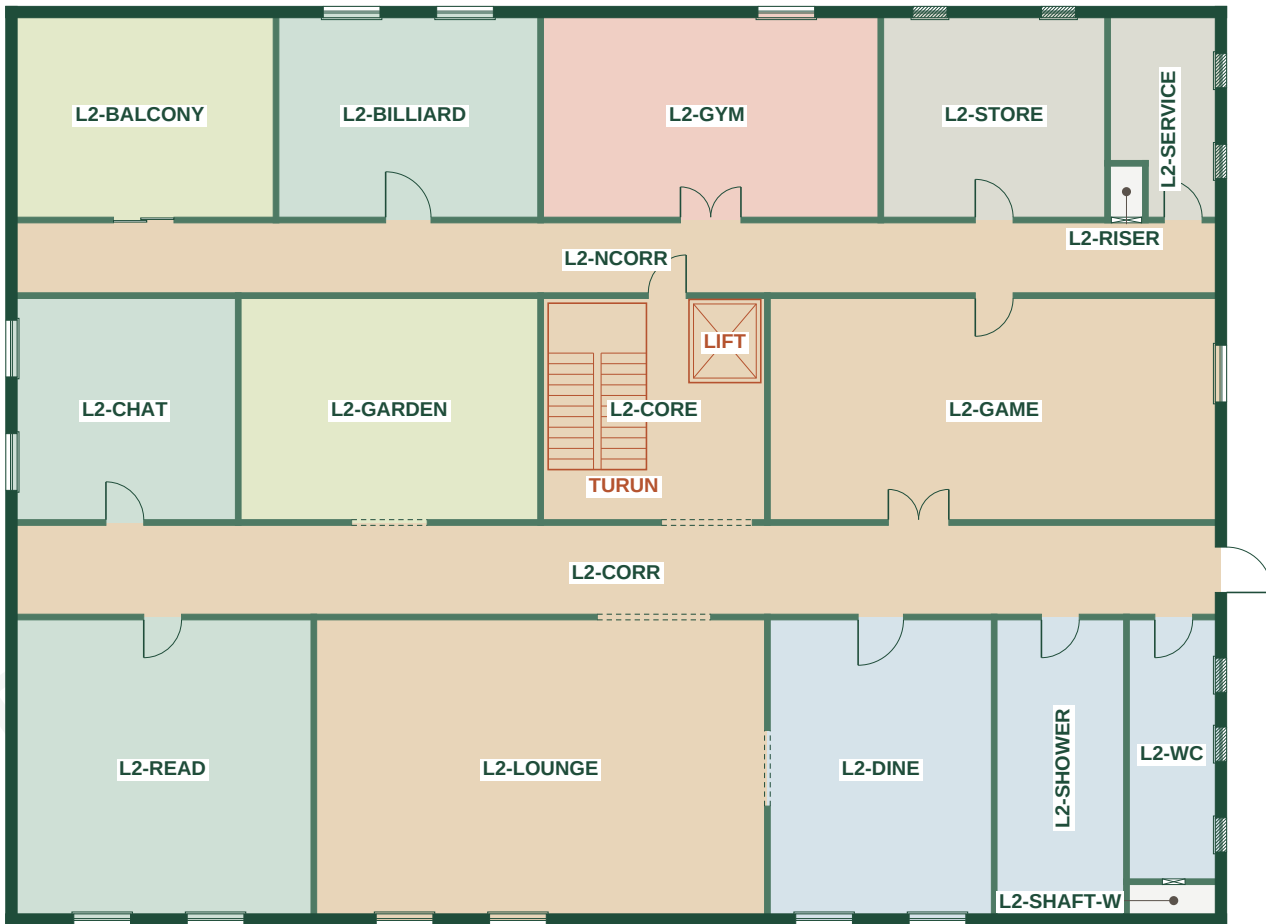

LEGENDA FINISH LANTAI (finish.floor di world.json)

Finish	Ruang	Luas m ²	Kontras teks
vinyl motif kayu	12	743,50	9,6:1
karpets tile matte	8	361,00	10,0:1
keramik anti-slip	5	139,00	10,5:1
- (tanpa finish: shaft/riser)	4	8,00	12,5:1
epoxy	3	63,00	10,0:1
vinyl anti-statik (target)	3	85,50	10,4:1
deck komposit	2	86,50	11,0:1
lantai karet olahraga	1	49,50	9,5:1

Total luas 1536,00 m² (dua lantai), 38 ruang.

CATATAN

- Warna = finish lantai per ruang dari world.json; finish dinding dan plafon tercantum di A-103.
- Finish adalah proposal konsep (status ruang 'proposal konsep'), bukan spesifikasi material.
- Luas as-drawn di as dinding (AS-DIM-02); ukuran gedung proposal (AS-DIM-01, AS-DIM-03).
- Kontras teks dihitung (WCAG) terhadap setiap warna isi; minimum 4,5:1.

STATUS KONSEP

Bukan untuk konstruksi

kantor-rpgProyek kantor-rpg · gedung KRPG-01

Finish interior dan material

Skala1:200 @ A3 lanskap
RevisiP03 · 2026-10-01
Render2026-10-02 02:42:18 UTC
Halaman1/1
DigambarClaude Code cloud (generator)
DiperiksaMax (supervisor) belum review
Sumberworld.json sha256 488597bb0552fbde
Huruf: Helvetica fallback (Alegreya Sans tidak tersedia saat build).

Nomor lembar


I-101

Rev P03 · 1/1



TOPOLOGI JARINGAN (VIRTUAL)

RANCANGAN VIRTUAL, BUKAN TOPOLOGI PRODUKSI

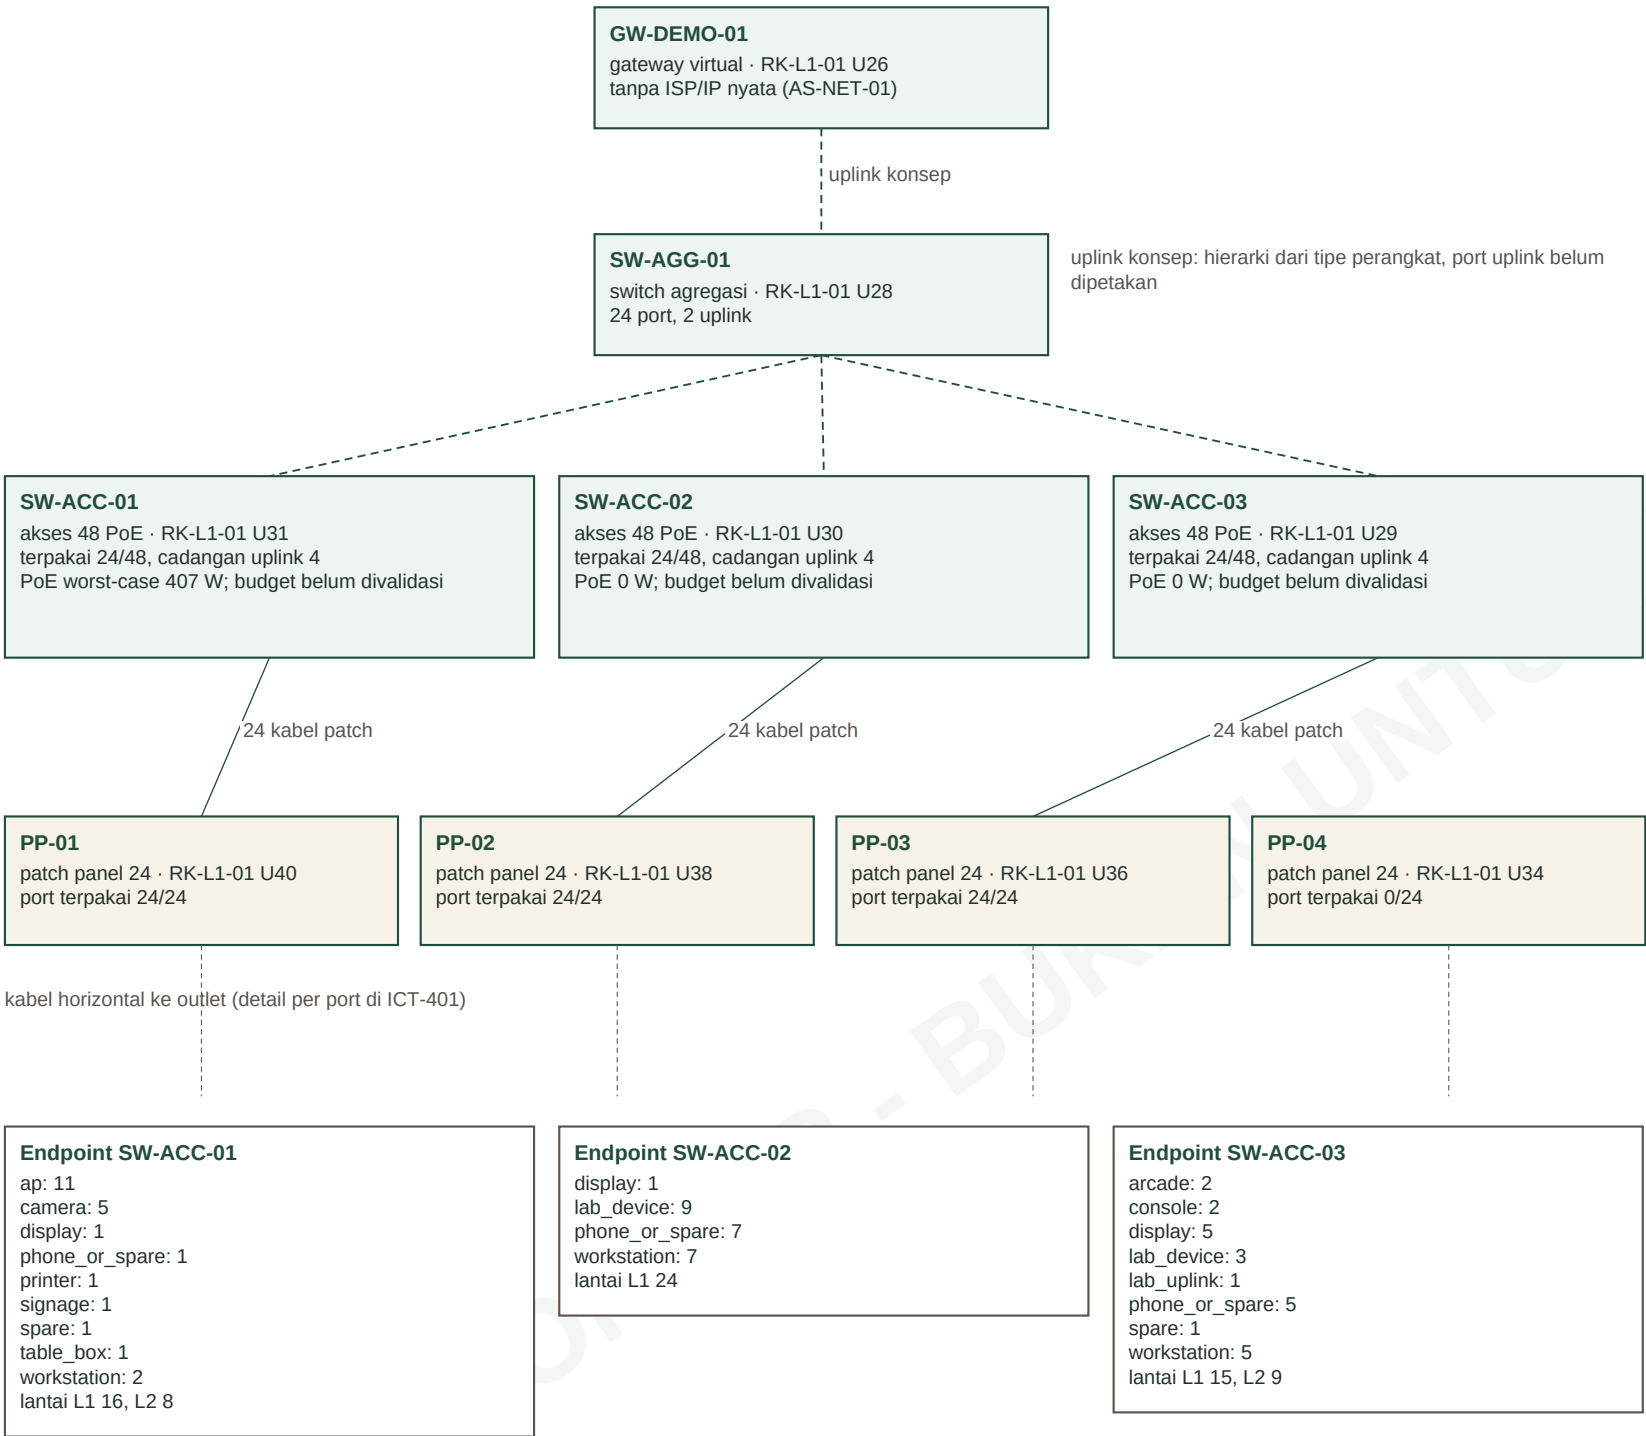

DOMAIN (ID abstrak, AS-NET-01)

Domain	Label	Port	Catatan
NET-OFFICE	office	48	abstrak
NET-DEMO	demo	10	abstrak
NET-GUEST	guest	0	abstrak, SSID tamu konsep
NET-LAB	lab	14	abstrak, terisolasi konsep
NET-SERVER	server	0	abstrak

JUMLAH DARI DATA

Outlet	45 outlet, 72 port
Patch panel	4 x 24 = 96 port, terpakai 72
Access point	11 placeholder (AS-ICT-01): L1 5, L2 6
Kamera	5 opsional konsep: L1 3, L2 2
Kabel	72 kabel, total 2074,8 m (AS-ICT-02)
PoE	worst-case 407 W dari kelas IEEE (AS-ICT-04); belum divalidasi

RACK

RK-L1-01	L1-SERVER, 42U: PP-01 U40, CM-01 U39, PP-02 U38, CM-02 U37, PP-03 U36, CM-03 U35, PP-04 U34, CM-04 U33, SW-ACC-01 U31, SW-ACC-02 U30, SW-ACC-03 U29, SW-AGG-01 U28, GW-DEMO-01 U26
RK-L1-02	L1-SERVER, 42U: SRV-DEMO-01 U20, NAS-DEMO-01 U17, PDU-01 U10, UPS-01 U1

SRV-DEMO-01 dan NAS-DEMO-01 belum punya port map; koneksinya tidak digambar.

STATUS KONSEP

Bukan untuk konstruksi

kantor-rpg Proyek kantor-rpg · gedung KRPG-01

Topologi jaringan (virtual)

Skala	NTS @ A3 lanskap
Revisi	P03 · 2026-10-01
Render	2026-10-02 02:42:18 UTC
Halaman	1/1
Digambar	Claude Code cloud (generator)
Diperiksa	Max (supervisor) belum review
Sumber	world.json sha256 488597bb0552fbde

Huruf: Helvetica fallback (Alegreya Sans tidak tersedia saat build).

Nomor lembar

ICT-001

Rev P03 · 1/1



Rancangan virtual, bukan topologi produksi

Lantai L1: Lantai 1 - Kerja & Kunjungan. Sumber: world.json ict + design/derived/ict-portmap.json

LEGENDA

- △ Outlet data, tag Tnn
- AP placeholder, tag APn
- Kamera opsional + arah konsep
- Tray kabel +3,2 m
- Riser ke lantai lain
- Rack 42U (target)

OUTLET L1 (30 outlet, 55 port)

Tag	ID	Ruang	Port	Tag	ID	Ruang	Port
T1	TO-L1-001	LOBBY	2	T16	TO-L1-016	LAB	4
T2	TO-L1-002	LOBBY	1	T17	TO-L1-017	LAB	2
T3	TO-L1-003	MEET	2	T18	TO-L1-018	CEO	2
T4	TO-L1-004	MEET	1	T19	TO-L1-019	HUGO	2
T5	TO-L1-005	IMPL	2	T20	TO-L1-020	HUGO	2
T6	TO-L1-006	IMPL	2	T21	TO-L1-021	KEVIN	2
T7	TO-L1-007	IMPL	2	T22	TO-L1-022	BRUNO	2
T8	TO-L1-008	IMPL	2	T23	TO-L1-023	LOBBY	1
T9	TO-L1-009	IMPL	2	T24	TO-L1-024	IMPL	1
T10	TO-L1-010	IMPL	2	T25	TO-L1-025	CORR	1
T11	TO-L1-011	IMPL	1	T26	TO-L1-026	NCORR	1
T12	TO-L1-012	NOVA	2	T27	TO-L1-027	NCORR	1
T13	TO-L1-013	NOVA	2	T28	TO-L1-028	LOBBY	1
T14	TO-L1-014	LAB	4	T29	TO-L1-029	CORR	1
T15	TO-L1-015	LAB	4	T30	TO-L1-030	BRUNO	1

Domain dan endpoint per port: ICT-401.

PERANGKAT L1 (AP 5, kamera 3)

Tag	ID	Ruang	Outlet	z m	PoE
AP1	AP-L1-01	LOBBY	T23	3,0	4
AP2	AP-L1-02	IMPL	T24	3,0	4
AP3	AP-L1-03	CORR	T25	3,0	4
AP4	AP-L1-04	NCORR	T26	3,0	4
AP5	AP-L1-05	NCORR	T27	3,0	4
CAM1	CAM-L1-01	LOBBY	T28	2,8	3
CAM2	CAM-L1-02	CORR	T29	2,8	3
CAM3	CAM-L1-03	BRUNO	T30	2,8	3

Semua AP placeholder (AS-ICT-01); kamera opsional konsep, arah bukan FOV terukur. Lihat juga AS-ICT-02, AS-ICT-03, AS-NET-01 di A-001.

STATUS KONSEP

Bukan untuk konstruksi

kantor-rpg Proyek kantor-rpg · gedung KRPG-01


Outlet, AP dan kamera Lantai 1

Skala 1:100 @ A2 lanskap
Revisi P03 · 2026-10-01
Render 2026-10-02 02:42:18 UTC
Halaman 1/1
Digambar Claude Code cloud (generator)
Diperiksa Max (supervisor) belum review
Sumber world.json sha256 488597bb0552fbde
Huruf: Helvetica fallback (Alegreya Sans tidak tersedia saat build).

Nomor lembar

ICT-101

Rev P03 · 1/1

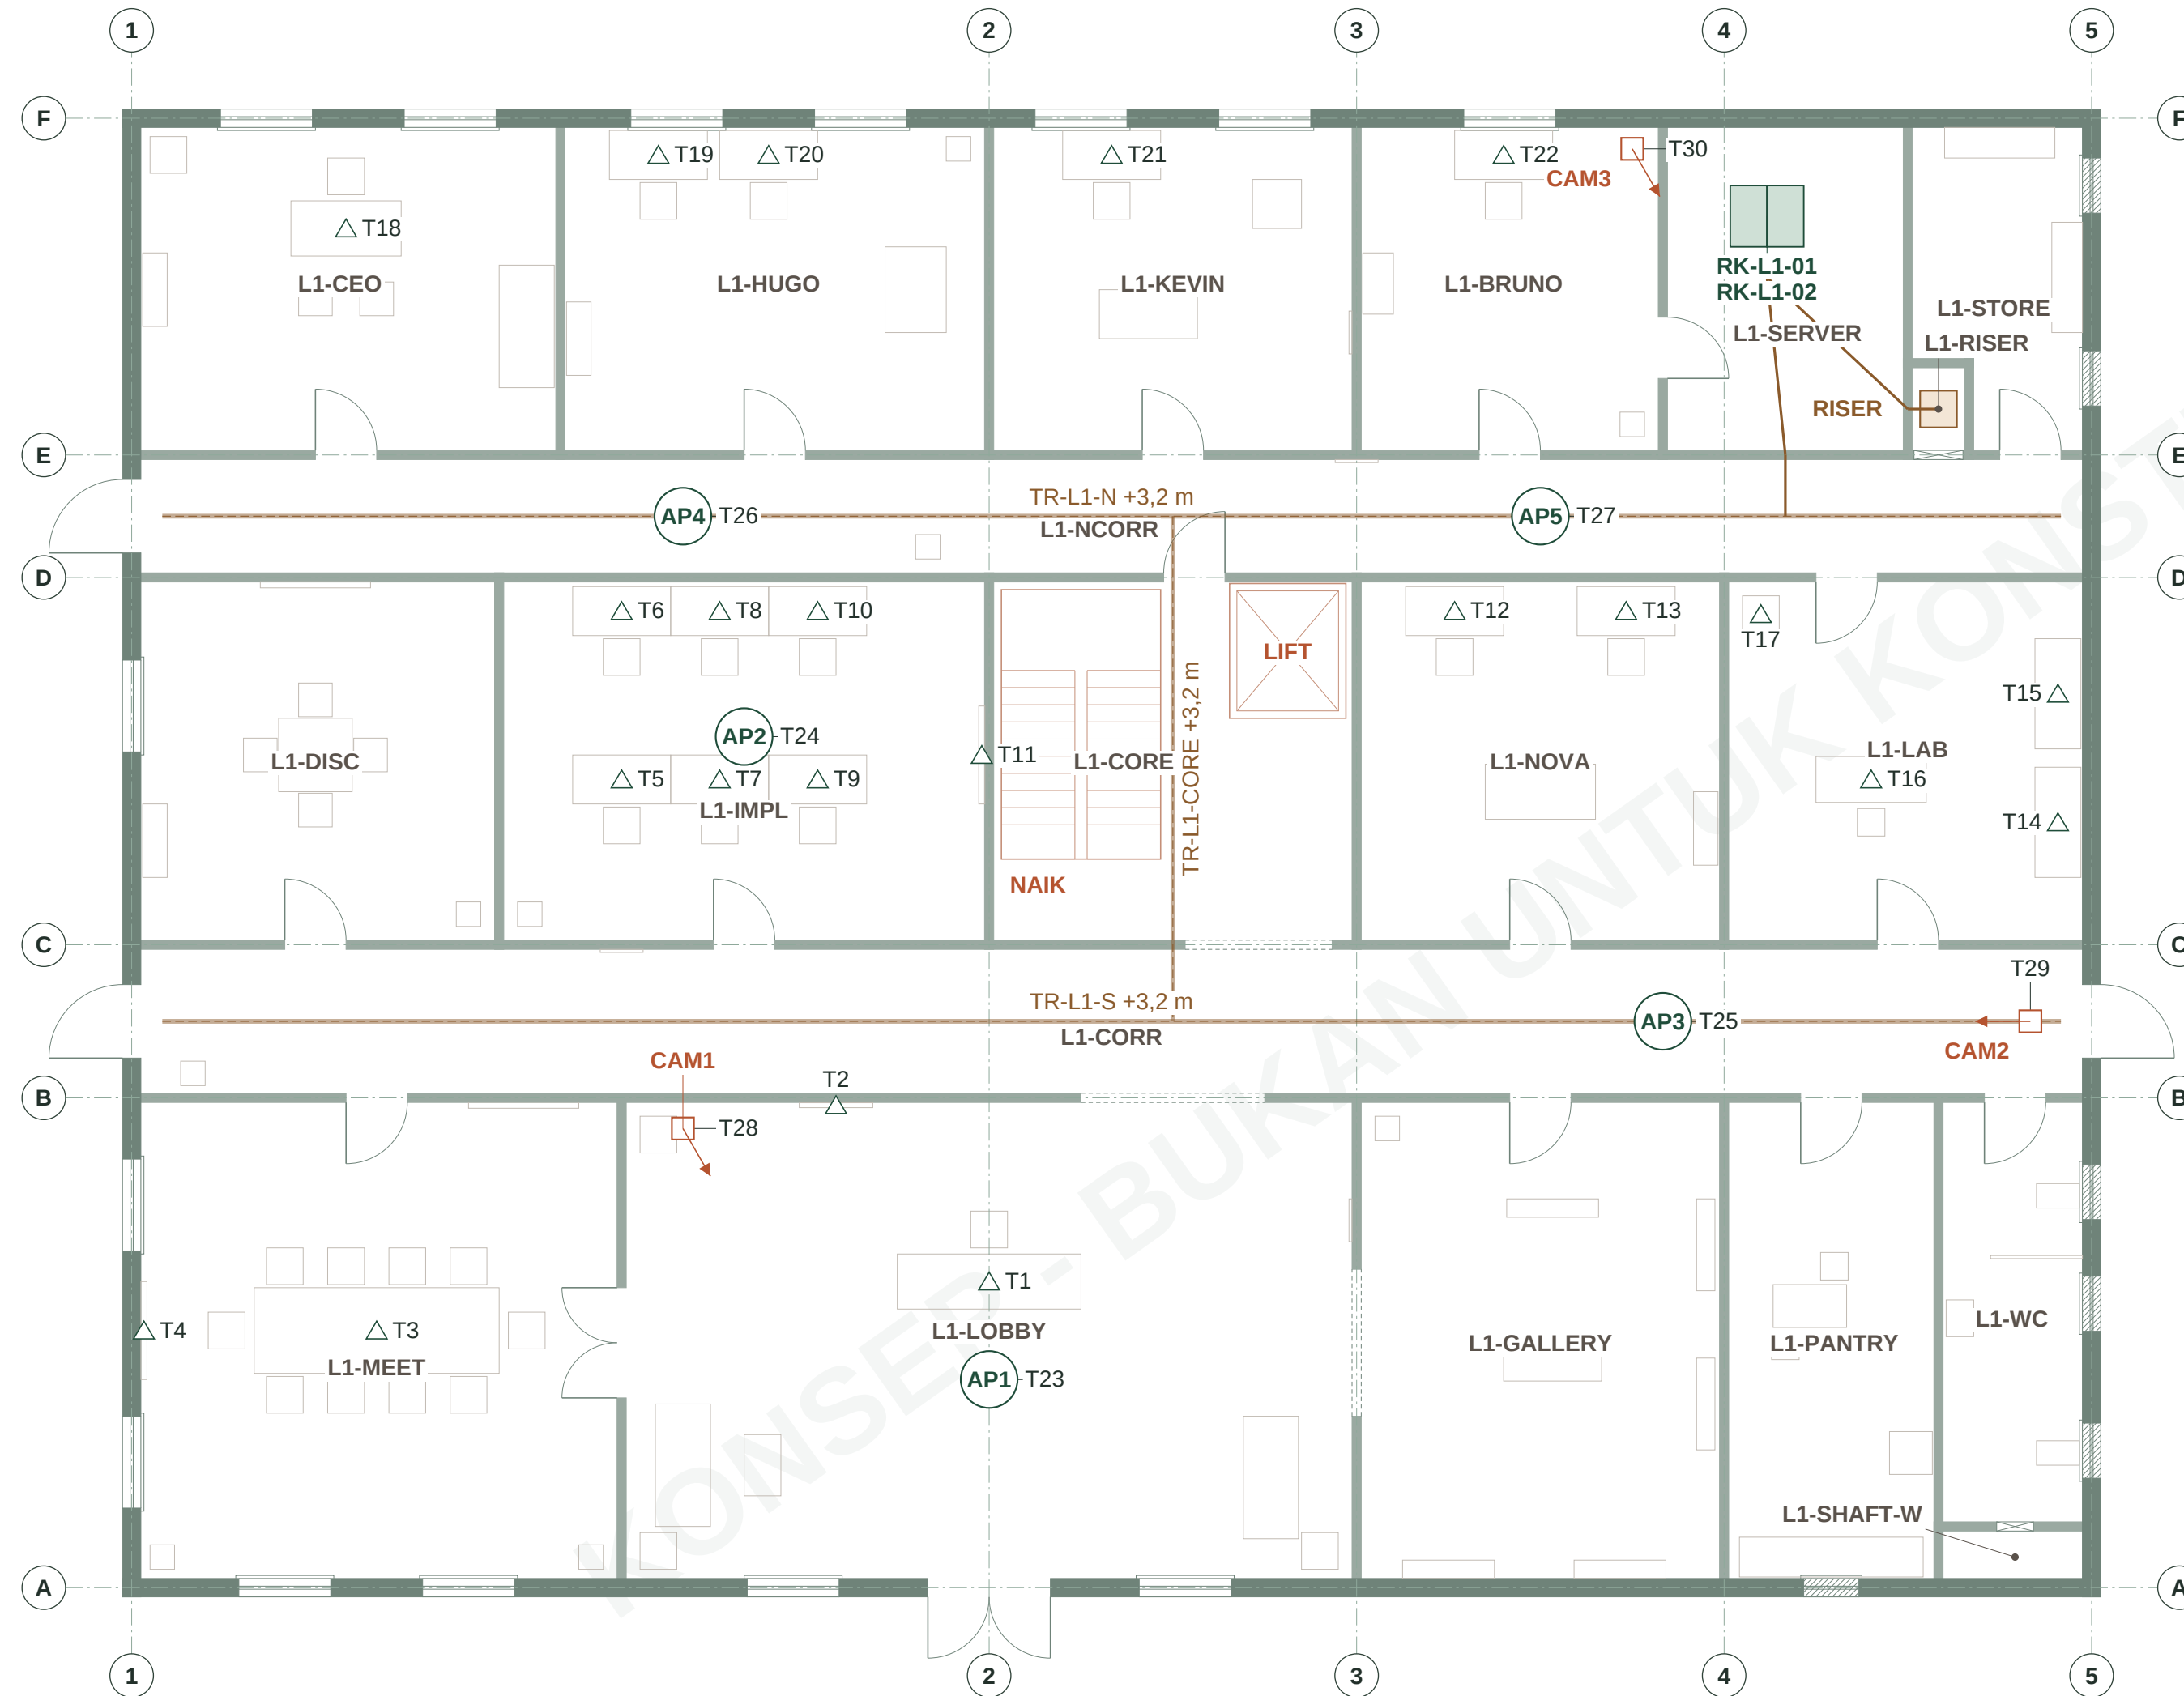

OUTLET, AP DAN KAMERA LANTAI 1

Skala 1:100 @ A2

Tag Tnn = outlet TO-L1-0nn, APn/CAMn = perangkat; ID lengkap di tabel panel. Tray di +3,2 m (AS-ICT-02). AP placeholder tanpa klaim radius Wi-Fi (AS-ICT-01).



OUTLET, AP DAN KAMERA LANTAI 2 Skala 1:100 @ A2

Tag Tnn = outlet TO-L2-0nn, APn/CAMn = perangkat; ID lengkap di tabel panel. Tray di +3,2 m (AS-ICT-02). AP placeholder tanpa klaim radius Wi-Fi (AS-ICT-01).



Rancangan virtual, bukan topologi produksi

Lantai L2: Lantai 2 - Rekreasi. Sumber: world.json ict + design/derived/ict-portmap.json

LEGENDA

- △ Outlet data, tag Tnn
□ Kamera opsional + arah konsep
■ Riser ke lantai lain
○ AP placeholder, tag APn
— Tray kabel +3,2 m
■ Rack 42U (target)

OUTLET L2 (15 outlet, 17 port)

Tag	ID	Ruang	Port	Tag	ID	Ruang	Port
T1	TO-L2-001	DINE	1	T9	TO-L2-009	DINE	1
T2	TO-L2-002	GAME	2	T10	TO-L2-010	GAME	1
T3	TO-L2-003	GAME	2	T11	TO-L2-011	CORR	1
T4	TO-L2-004	GAME	1	T12	TO-L2-012	NCORR	1
T5	TO-L2-005	GAME	1	T13	TO-L2-013	GYM	1
T6	TO-L2-006	BILLIARD	1	T14	TO-L2-014	CORR	1
T7	TO-L2-007	GYM	1	T15	TO-L2-015	NCORR	1
T8	TO-L2-008	LOUNGE	1				

Domain dan endpoint per port: ICT-401.

PERANGKAT L2 (AP 6, kamera 2)

Tag	ID	Ruang	Outlet	z m	PoE
AP1	AP-L2-01	LOUNGE	T8	3,0	4
AP2	AP-L2-02	DINE	T9	3,0	4
AP3	AP-L2-03	GAME	T10	3,0	4
AP4	AP-L2-04	CORR	T11	3,0	4
AP5	AP-L2-05	NCORR	T12	3,0	4
AP6	AP-L2-06	GYM	T13	3,0	4
CAM1	CAM-L2-01	CORR	T14	2,8	3
CAM2	CAM-L2-02	NCORR	T15	2,8	3

Semua AP placeholder (AS-ICT-01); kamera opsional konsep, arah bukan FOV terukur. Lihat juga AS-ICT-02, AS-ICT-03, AS-NET-01 di A-001.

STATUS KONSEP

Bukan untuk konstruksi

kantor-rpg Proyek kantor-rpg · gedung KRPG-01

Outlet, AP dan kamera Lantai 2


Skala 1:100 @ A2 lanskap
Revisi P03 · 2026-10-01
Render 2026-10-02 02:42:18 UTC
Halaman 1/1
Digambar Claude Code cloud (generator)
Diperiksa Max (supervisor) belum review
Sumber world.json sha256 488597bb0552fbde
Huruf: Helvetica fallback (Alegreya Sans tidak tersedia saat build).

Nomor lembar


ICT-102

Rev P03 · 1/1


RK-L1-01 TAMPAK DEPAN 1:10 · L1-SERVER · 42U

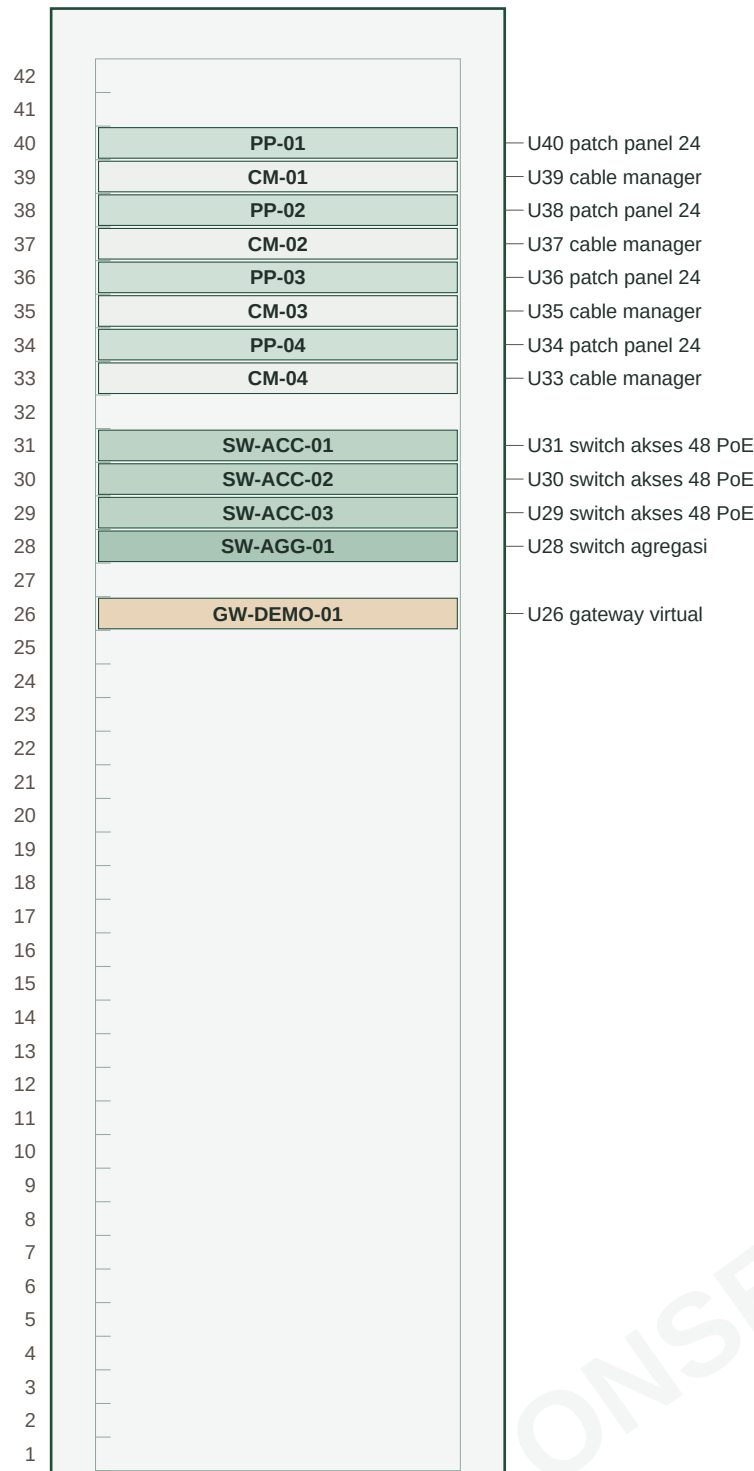

RK-L1-02 TAMPAK DEPAN 1:10 · L1-SERVER · 42U

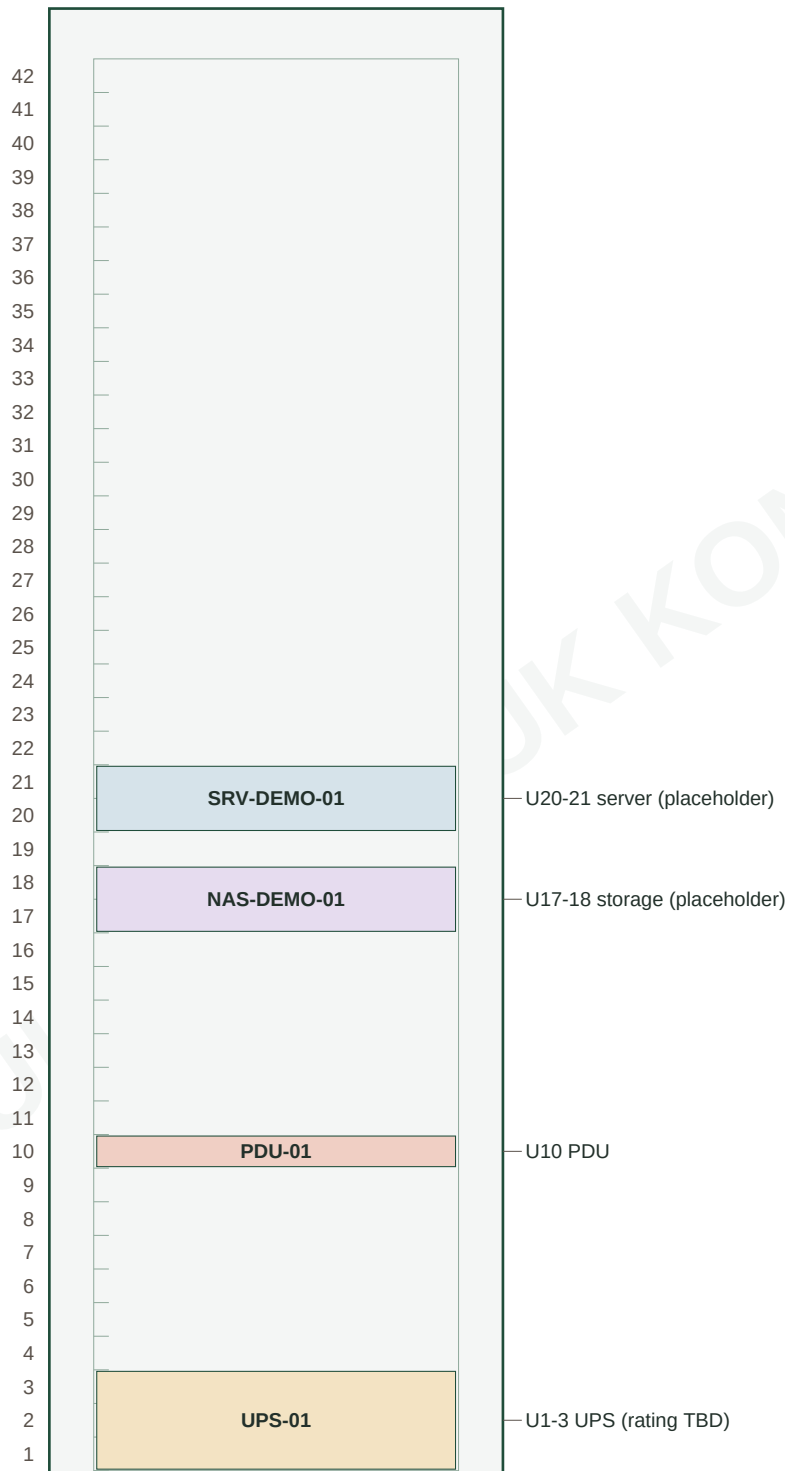

CLEARANCE RACK 1:100 (AS-ICT-06)

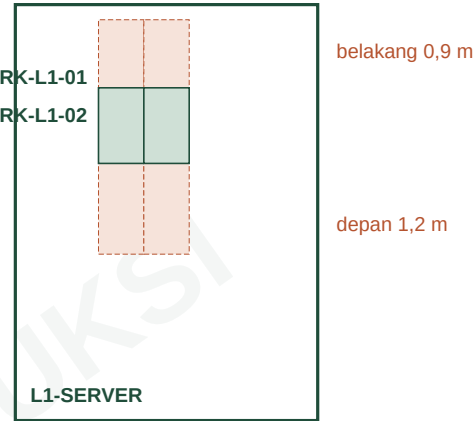

ISI RACK (world.json racks[].contents)

Rack	U	Tg	Perangkat	Tipe	Port
RK-L1-01	U40	1	PP-01	patch panel 24	24
RK-L1-01	U39	1	CM-01	cable manager	-
RK-L1-01	U38	1	PP-02	patch panel 24	24
RK-L1-01	U37	1	CM-02	cable manager	-
RK-L1-01	U36	1	PP-03	patch panel 24	24
RK-L1-01	U35	1	CM-03	cable manager	-
RK-L1-01	U34	1	PP-04	patch panel 24	24
RK-L1-01	U33	1	CM-04	cable manager	-
RK-L1-01	U31	1	SW-ACC-01	switch akses 48 PoE	48
RK-L1-01	U30	1	SW-ACC-02	switch akses 48 PoE	48
RK-L1-01	U29	1	SW-ACC-03	switch akses 48 PoE	48
RK-L1-01	U28	1	SW-AGG-01	switch agregasi	24
RK-L1-01	U26	1	GW-DEMO-01	gateway virtual	8
RK-L1-02	U20	2	SRV-DEMO-01	server (placeholder)	2
RK-L1-02	U17	2	NAS-DEMO-01	storage (placeholder)	2
RK-L1-02	U10	1	PDU-01	PDU	-
RK-L1-02	U1	3	UPS-01	UPS (rating TBD)	-

- Skala tampak rack 1:10; 1U = 44,45 mm, nomor U dihitung dari bawah. Tg = tinggi dalam U.
- Model switch, PDU dan UPS belum dipilih (AS-ICT-04, AS-ICT-05); tidak ada harga.
- Clearance depan 1,2 m / belakang 0,9 m adalah target konsep dari catalog (AS-ICT-06), wajib diverifikasi ke standar yang dipilih.

STATUS KONSEP

Bukan untuk konstruksi

kantor-rpg Proyek kantor-rpg · gedung KRPg-01

Elevasi rack

Skala 1:10 @ A3 lanskap
Revisi P03 · 2026-10-01
Render 2026-10-02 02:42:18 UTC
Halaman 1/1
Digambar Claude Code cloud (generator)
Diperiksa Max (supervisor) belum review
Sumber world.json sha256 488597bb0552fbde


Huruf: Helvetica fallback (Alegreya Sans tidak tersedia saat build).

Nomor lembar


ICT-201

Rev P03 · 1/1

JALUR KABEL L1 1:200 · tray +3,2 m

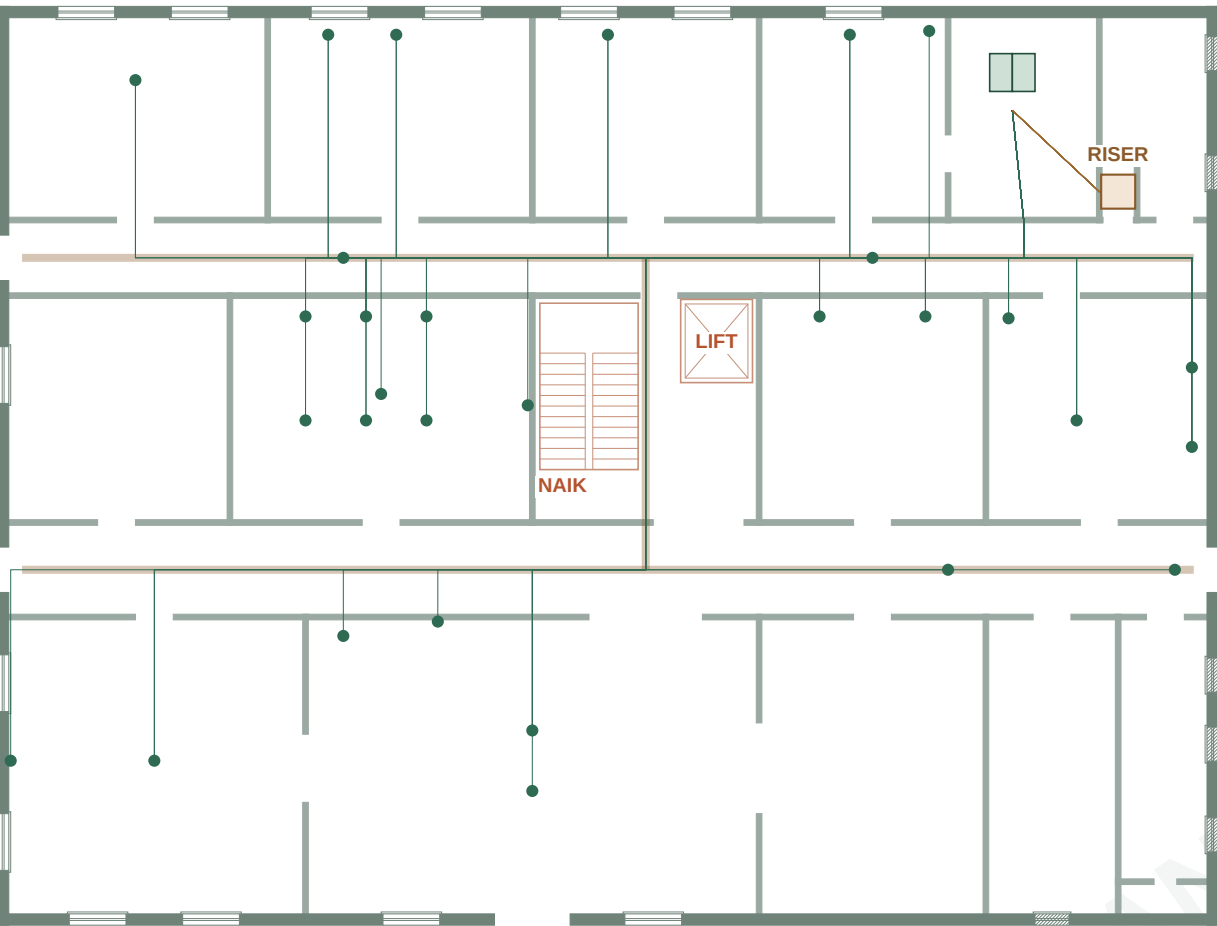

JALUR KABEL L2 1:200 · tray +3,2 m

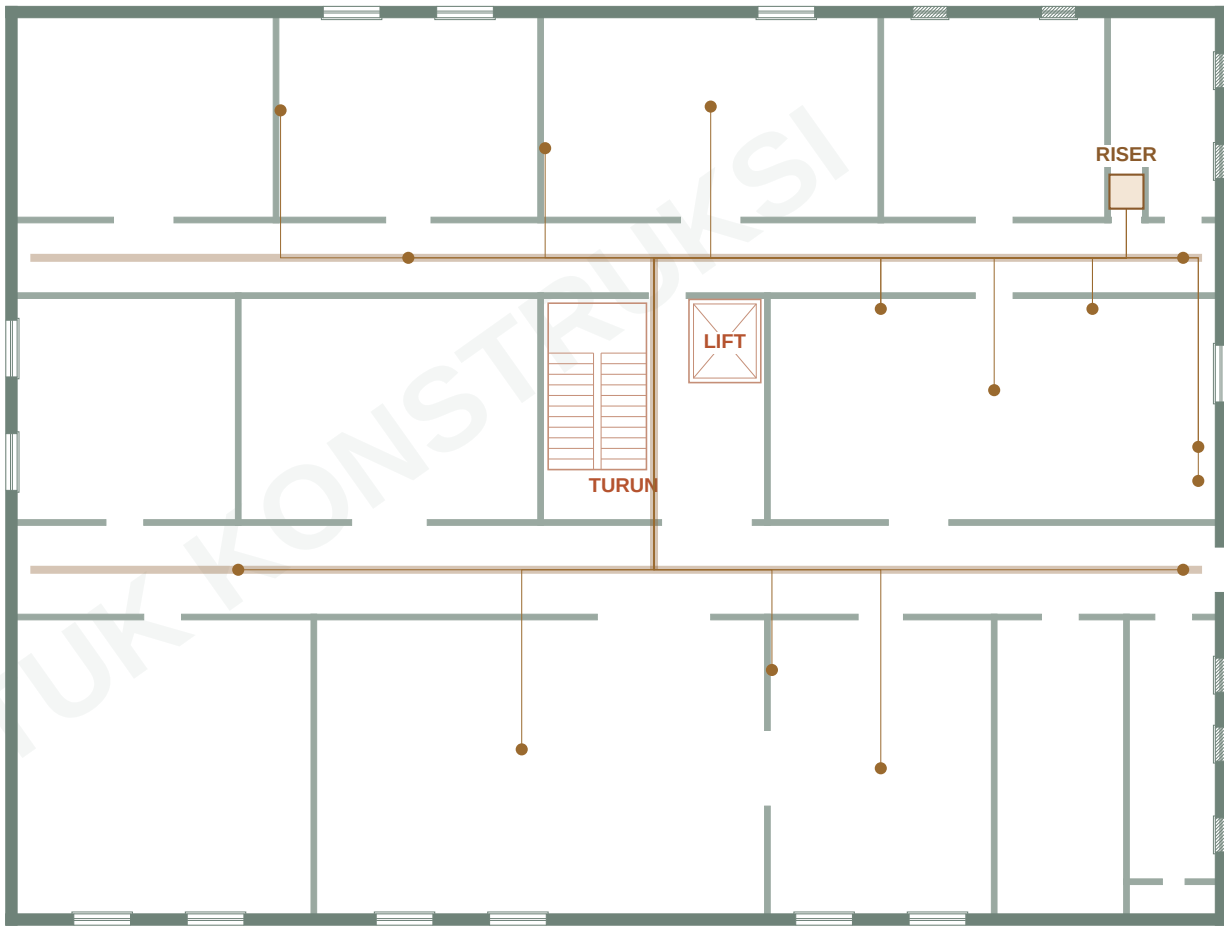


RINGKASAN PANJANG KABEL (ict-portmap.json)

Lantai	Kabel	Total m	Min m	Maks m	Rata m
L1	55	1537,1	12,7	50,6	27,9
L2	17	537,7	15,6	48,9	31,6
Total	72	2074,8	12,7	50,6	28,8

Cek: jumlah baris 2074,8 m vs total port map 2074,8 m: COCOK. Semua kabel di bawah target 90 m (AS-ICT-03).

SKEMA RISER

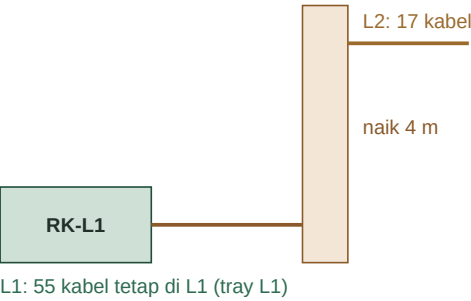

- Garis hijau = kabel endpoint L1, coklat = kabel endpoint L2 (bagian di L1 ikut warna lantai tujuan).
- Panjang = route tray + naik rack 1,2 m + riser 4,0 m (L2) + drop + slack 3,3 m (AS-ICT-02).



STATUS KONSEP

Bukan untuk konstruksi

kantor-rpg Proyek kantor-rpg · gedung KRPG-01
Pathway dan riser

Skala 1:200 @ A3 lanskap
Revisi P03 · 2026-10-01
Render 2026-10-02 02:42:18 UTC
Halaman 1/1
Digambar Claude Code cloud (generator)
Diperiksa Max (supervisor) belum review
Sumber world.json sha256 488597bb0552fbde
Huruf: Helvetica fallback (Alegreya Sans tidak tersedia saat build).

Nomor lembar

ICT-301

Rev P03 · 1/1

PORT SCHEDULE

rancangan virtual, bukan topologi produksi · sumber design/derived/ict-portmap.json (world P03)

Kabel	Port outlet	Ruang	PP/port	Switch/port	Domain	PoE	m	Label sisi rack	Label sisi outlet	Endpoint
C-TO-L1-023-A	TO-L1-023-A	L1-LOBBY	PP-01/01	SW-ACC-01/01	NET-OFFICE	4	35,8	PP-01-01 > TO-L1-023-A	TO-L1-023-A > PP-01-01	ap AP-L1-01
C-TO-L1-024-A	TO-L1-024-A	L1-IMPL	PP-01/02	SW-ACC-01/02	NET-OFFICE	4	29,3	PP-01-02 > TO-L1-024-A	TO-L1-024-A > PP-01-02	ap AP-L1-02
C-TO-L1-025-A	TO-L1-025-A	L1-CORR	PP-01/03	SW-ACC-01/03	NET-OFFICE	4	34,9	PP-01-03 > TO-L1-025-A	TO-L1-025-A > PP-01-03	ap AP-L1-03
C-TO-L1-026-A	TO-L1-026-A	L1-NCORR	PP-01/04	SW-ACC-01/04	NET-OFFICE	4	26,7	PP-01-04 > TO-L1-026-A	TO-L1-026-A > PP-01-04	ap AP-L1-04
C-TO-L1-027-A	TO-L1-027-A	L1-NCORR	PP-01/05	SW-ACC-01/05	NET-OFFICE	4	12,7	PP-01-05 > TO-L1-027-A	TO-L1-027-A > PP-01-05	ap AP-L1-05
C-TO-L1-028-A	TO-L1-028-A	L1-LOBBY	PP-01/06	SW-ACC-01/06	NET-OFFICE	3	36,7	PP-01-06 > TO-L1-028-A	TO-L1-028-A > PP-01-06	camera CAM-L1-01
C-TO-L1-029-A	TO-L1-029-A	L1-CORR	PP-01/07	SW-ACC-01/07	NET-OFFICE	3	40,9	PP-01-07 > TO-L1-029-A	TO-L1-029-A > PP-01-07	camera CAM-L1-02
C-TO-L1-030-A	TO-L1-030-A	L1-BRUNO	PP-01/08	SW-ACC-01/08	NET-OFFICE	3	17,2	PP-01-08 > TO-L1-030-A	TO-L1-030-A > PP-01-08	camera CAM-L1-03
C-TO-L2-008-A	TO-L2-008-A	L2-LOUNGE	PP-01/09	SW-ACC-01/09	NET-OFFICE	4	43,1	PP-01-09 > TO-L2-008-A	TO-L2-008-A > PP-01-09	ap AP-L2-01
C-TO-L2-009-A	TO-L2-009-A	L2-DINE	PP-01/10	SW-ACC-01/10	NET-OFFICE	4	46,1	PP-01-10 > TO-L2-009-A	TO-L2-009-A > PP-01-10	ap AP-L2-02
C-TO-L2-010-A	TO-L2-010-A	L2-GAME	PP-01/11	SW-ACC-01/11	NET-OFFICE	4	21,1	PP-01-11 > TO-L2-010-A	TO-L2-010-A > PP-01-11	ap AP-L2-03
C-TO-L2-011-A	TO-L2-011-A	L2-CORR	PP-01/12	SW-ACC-01/12	NET-OFFICE	4	45,9	PP-01-12 > TO-L2-011-A	TO-L2-011-A > PP-01-12	ap AP-L2-04
C-TO-L2-012-A	TO-L2-012-A	L2-NCORR	PP-01/13	SW-ACC-01/13	NET-OFFICE	4	33,1	PP-01-13 > TO-L2-012-A	TO-L2-012-A > PP-01-13	ap AP-L2-05
C-TO-L2-013-A	TO-L2-013-A	L2-GYM	PP-01/14	SW-ACC-01/14	NET-OFFICE	4	29,1	PP-01-14 > TO-L2-013-A	TO-L2-013-A > PP-01-14	ap AP-L2-06
C-TO-L2-014-A	TO-L2-014-A	L2-CORR	PP-01/15	SW-ACC-01/15	NET-OFFICE	3	48,9	PP-01-15 > TO-L2-014-A	TO-L2-014-A > PP-01-15	camera CAM-L2-01
C-TO-L2-015-A	TO-L2-015-A	L2-NCORR	PP-01/16	SW-ACC-01/16	NET-OFFICE	3	15,6	PP-01-16 > TO-L2-015-A	TO-L2-015-A > PP-01-16	camera CAM-L2-02
C-TO-L1-001-A	TO-L1-001-A	L1-LOBBY	PP-01/17	SW-ACC-01/17	NET-OFFICE	-	36,9	PP-01-17 > TO-L1-001-A	TO-L1-001-A > PP-01-17	workstation FX-L1-001
C-TO-L1-001-B	TO-L1-001-B	L1-LOBBY	PP-01/18	SW-ACC-01/18	NET-OFFICE	-	36,9	PP-01-18 > TO-L1-001-B	TO-L1-001-B > PP-01-18	printer FX-L1-001
C-TO-L1-002-A	TO-L1-002-A	L1-LOBBY	PP-01/19	SW-ACC-01/19	NET-DEMO	-	35,6	PP-01-19 > TO-L1-002-A	TO-L1-002-A > PP-01-19	signage FX-L1-009
C-TO-L1-003-A	TO-L1-003-A	L1-MEET	PP-01/20	SW-ACC-01/20	NET-OFFICE	-	47,7	PP-01-20 > TO-L1-003-A	TO-L1-003-A > PP-01-20	table_box FX-L1-011
C-TO-L1-003-B	TO-L1-003-B	L1-MEET	PP-01/21	SW-ACC-01/21	NET-OFFICE	-	47,7	PP-01-21 > TO-L1-003-B	TO-L1-003-B > PP-01-21	spare FX-L1-011
C-TO-L1-004-A	TO-L1-004-A	L1-MEET	PP-01/22	SW-ACC-01/22	NET-OFFICE	-	50,6	PP-01-22 > TO-L1-004-A	TO-L1-004-A > PP-01-22	display FX-L1-022
C-TO-L1-005-A	TO-L1-005-A	L1-IMPL	PP-01/23	SW-ACC-01/23	NET-OFFICE	-	34,7	PP-01-23 > TO-L1-005-A	TO-L1-005-A > PP-01-23	workstation FX-L1-053
C-TO-L1-005-B	TO-L1-005-B	L1-IMPL	PP-01/24	SW-ACC-01/24	NET-OFFICE	-	34,7	PP-01-24 > TO-L1-005-B	TO-L1-005-B > PP-01-24	phone_or_spare FX-L1-053
C-TO-L1-006-A	TO-L1-006-A	L1-IMPL	PP-02/01	SW-ACC-02/01	NET-OFFICE	-	31,9	PP-02-01 > TO-L1-006-A	TO-L1-006-A > PP-02-01	workstation FX-L1-055
C-TO-L1-006-B	TO-L1-006-B	L1-IMPL	PP-02/02	SW-ACC-02/02	NET-OFFICE	-	31,9	PP-02-02 > TO-L1-006-B	TO-L1-006-B > PP-02-02	phone_or_spare FX-L1-055
C-TO-L1-007-A	TO-L1-007-A	L1-IMPL	PP-02/03	SW-ACC-02/03	NET-OFFICE	-	33,1	PP-02-03 > TO-L1-007-A	TO-L1-007-A > PP-02-03	workstation FX-L1-057
C-TO-L1-007-B	TO-L1-007-B	L1-IMPL	PP-02/04	SW-ACC-02/04	NET-OFFICE	-	33,1	PP-02-04 > TO-L1-007-B	TO-L1-007-B > PP-02-04	phone_or_spare FX-L1-057
C-TO-L1-008-A	TO-L1-008-A	L1-IMPL	PP-02/05	SW-ACC-02/05	NET-OFFICE	-	30,3	PP-02-05 > TO-L1-008-A	TO-L1-008-A > PP-02-05	workstation FX-L1-059
C-TO-L1-008-B	TO-L1-008-B	L1-IMPL	PP-02/06	SW-ACC-02/06	NET-OFFICE	-	30,3	PP-02-06 > TO-L1-008-B	TO-L1-008-B > PP-02-06	phone_or_spare FX-L1-059
C-TO-L1-009-A	TO-L1-009-A	L1-IMPL	PP-02/07	SW-ACC-02/07	NET-OFFICE	-	31,5	PP-02-07 > TO-L1-009-A	TO-L1-009-A > PP-02-07	workstation FX-L1-061
C-TO-L1-009-B	TO-L1-009-B	L1-IMPL	PP-02/08	SW-ACC-02/08	NET-OFFICE	-	31,5	PP-02-08 > TO-L1-009-B	TO-L1-009-B > PP-02-08	phone_or_spare FX-L1-061
C-TO-L1-010-A	TO-L1-010-A	L1-IMPL	PP-02/09	SW-ACC-02/09	NET-OFFICE	-	28,7	PP-02-09 > TO-L1-010-A	TO-L1-010-A > PP-02-09	workstation FX-L1-063
C-TO-L1-010-B	TO-L1-010-B	L1-IMPL	PP-02/10	SW-ACC-02/10	NET-OFFICE	-	28,7	PP-02-10 > TO-L1-010-B	TO-L1-010-B > PP-02-10	phone_or_spare FX-L1-063
C-TO-L1-011-A	TO-L1-011-A	L1-IMPL	PP-02/11	SW-ACC-02/11	NET-OFFICE	-	27,5	PP-02-11 > TO-L1-011-A	TO-L1-011-A > PP-02-11	display FX-L1-065
C-TO-L1-012-A	TO-L1-012-A	L1-NOVA	PP-02/12	SW-ACC-02/12	NET-OFFICE	-	18,3	PP-02-12 > TO-L1-012-A	TO-L1-012-A > PP-02-12	workstation FX-L1-069
C-TO-L1-012-B	TO-L1-012-B	L1-NOVA	PP-02/13	SW-ACC-02/13	NET-OFFICE	-	18,3	PP-02-13 > TO-L1-012-B	TO-L1-012-B > PP-02-13	phone_or_spare FX-L1-069
C-TO-L1-013-A	TO-L1-013-A	L1-NOVA	PP-02/14	SW-ACC-02/14	NET-OFFICE	-	15,5	PP-02-14 > TO-L1-013-A	TO-L1-013-A > PP-02-14	workstation FX-L1-071
C-TO-L1-013-B	TO-L1-013-B	L1-NOVA	PP-02/15	SW-ACC-02/15	NET-OFFICE	-	15,5	PP-02-15 > TO-L1-013-B	TO-L1-013-B > PP-02-15	phone_or_spare FX-L1-071
C-TO-L1-014-A	TO-L1-014-A	L1-LAB	PP-02/16	SW-ACC-02/16	NET-LAB	-	20,8	PP-02-16 > TO-L1-014-A	TO-L1-014-A > PP-02-16	lab_device FX-L1-075
C-TO-L1-014-B	TO-L1-014-B	L1-LAB	PP-02/17	SW-ACC-02/17	NET-LAB	-	20,8	PP-02-17 > TO-L1-014-B	TO-L1-014-B > PP-02-17	lab_device FX-L1-075
C-TO-L1-014-C	TO-L1-014-C	L1-LAB	PP-02/18	SW-ACC-02/18	NET-LAB	-	20,8	PP-02-18 > TO-L1-014-C	TO-L1-014-C > PP-02-18	lab_device FX-L1-075
C-TO-L1-014-D	TO-L1-014-D	L1-LAB	PP-02/19	SW-ACC-02/19	NET-LAB	-	20,8	PP-02-19 > TO-L1-014-D	TO-L1-014-D > PP-02-19	lab_device FX-L1-075
C-TO-L1-015-A	TO-L1-015-A	L1-LAB	PP-02/20	SW-ACC-02/20	NET-LAB	-	18,7	PP-02-20 > TO-L1-015-A	TO-L1-015-A > PP-02-20	lab_device FX-L1-076

Label dua ujung: sisi rack 'PP-nn-pp > port outlet', sisi outlet sebaliknya. Panjang mengikuti AS-ICT-02; batas 90 m AS-ICT-03.

STATUS KONSEP

Bukan untuk konstruksi

kantor-rpg Proyek kantor-rpg · gedung KRPg-01

Port dan device schedule

Skala NTS @ A3 lanskap
Revisi P03 · 2026-10-01
Render 2026-10-02 02:42:18 UTC
Halaman 1/3
Digambar Claude Code cloud (generator)
Diperiksa Max (supervisor) belum review
Sumber world.json sha256 488597bb0552fbde

Huruf: Helvetica fallback (Alegreya Sans tidak tersedia saat build).

Nomor lembar

ICT-401

Rev P03 · 1/3

PORT SCHEDULE

rancangan virtual, bukan topologi produksi · sumber design/derived/ict-portmap.json (world P03)

Kabel	Port outlet	Ruang	PP/port	Switch/port	Domain	PoE	m	Label sisi rack	Label sisi outlet	Endpoint
C-TO-L1-015-B	TO-L1-015-B	L1-LAB	PP-02/21	SW-ACC-02/21	NET-LAB	-	18,7	PP-02-21 > TO-L1-015-B	TO-L1-015-B > PP-02-21	lab_device FX-L1-076
C-TO-L1-015-C	TO-L1-015-C	L1-LAB	PP-02/22	SW-ACC-02/22	NET-LAB	-	18,7	PP-02-22 > TO-L1-015-C	TO-L1-015-C > PP-02-22	lab_device FX-L1-076
C-TO-L1-015-D	TO-L1-015-D	L1-LAB	PP-02/23	SW-ACC-02/23	NET-LAB	-	18,7	PP-02-23 > TO-L1-015-D	TO-L1-015-D > PP-02-23	lab_device FX-L1-076
C-TO-L1-016-A	TO-L1-016-A	L1-LAB	PP-02/24	SW-ACC-02/24	NET-LAB	-	17,1	PP-02-24 > TO-L1-016-A	TO-L1-016-A > PP-02-24	lab_device FX-L1-077
C-TO-L1-016-B	TO-L1-016-B	L1-LAB	PP-03/01	SW-ACC-03/01	NET-LAB	-	17,1	PP-03-01 > TO-L1-016-B	TO-L1-016-B > PP-03-01	lab_device FX-L1-077
C-TO-L1-016-C	TO-L1-016-C	L1-LAB	PP-03/02	SW-ACC-03/02	NET-LAB	-	17,1	PP-03-02 > TO-L1-016-C	TO-L1-016-C > PP-03-02	lab_device FX-L1-077
C-TO-L1-016-D	TO-L1-016-D	L1-LAB	PP-03/03	SW-ACC-03/03	NET-LAB	-	17,1	PP-03-03 > TO-L1-016-D	TO-L1-016-D > PP-03-03	lab_device FX-L1-077
C-TO-L1-017-A	TO-L1-017-A	L1-LAB	PP-03/04	SW-ACC-03/04	NET-LAB	-	13,4	PP-03-04 > TO-L1-017-A	TO-L1-017-A > PP-03-04	lab_uplink FX-L1-079
C-TO-L1-017-B	TO-L1-017-B	L1-LAB	PP-03/05	SW-ACC-03/05	NET-LAB	-	13,4	PP-03-05 > TO-L1-017-B	TO-L1-017-B > PP-03-05	spare FX-L1-079
C-TO-L1-018-A	TO-L1-018-A	L1-CEO	PP-03/06	SW-ACC-03/06	NET-OFFICE	-	39,6	PP-03-06 > TO-L1-018-A	TO-L1-018-A > PP-03-06	workstation FX-L1-082
C-TO-L1-018-B	TO-L1-018-B	L1-CEO	PP-03/07	SW-ACC-03/07	NET-OFFICE	-	39,6	PP-03-07 > TO-L1-018-B	TO-L1-018-B > PP-03-07	phone_or_spare FX-L1-082
C-TO-L1-019-A	TO-L1-019-A	L1-HUGO	PP-03/08	SW-ACC-03/08	NET-OFFICE	-	35,7	PP-03-08 > TO-L1-019-A	TO-L1-019-A > PP-03-08	workstation FX-L1-089
C-TO-L1-019-B	TO-L1-019-B	L1-HUGO	PP-03/09	SW-ACC-03/09	NET-OFFICE	-	35,7	PP-03-09 > TO-L1-019-B	TO-L1-019-B > PP-03-09	phone_or_spare FX-L1-089
C-TO-L1-020-A	TO-L1-020-A	L1-HUGO	PP-03/10	SW-ACC-03/10	NET-OFFICE	-	33,9	PP-03-10 > TO-L1-020-A	TO-L1-020-A > PP-03-10	workstation FX-L1-091
C-TO-L1-020-B	TO-L1-020-B	L1-HUGO	PP-03/11	SW-ACC-03/11	NET-OFFICE	-	33,9	PP-03-11 > TO-L1-020-B	TO-L1-020-B > PP-03-11	phone_or_spare FX-L1-091
C-TO-L1-021-A	TO-L1-021-A	L1-KEVIN	PP-03/12	SW-ACC-03/12	NET-OFFICE	-	28,3	PP-03-12 > TO-L1-021-A	TO-L1-021-A > PP-03-12	workstation FX-L1-096
C-TO-L1-021-B	TO-L1-021-B	L1-KEVIN	PP-03/13	SW-ACC-03/13	NET-OFFICE	-	28,3	PP-03-13 > TO-L1-021-B	TO-L1-021-B > PP-03-13	phone_or_spare FX-L1-096
C-TO-L1-022-A	TO-L1-022-A	L1-BRUNO	PP-03/14	SW-ACC-03/14	NET-OFFICE	-	21,9	PP-03-14 > TO-L1-022-A	TO-L1-022-A > PP-03-14	workstation FX-L1-101
C-TO-L1-022-B	TO-L1-022-B	L1-BRUNO	PP-03/15	SW-ACC-03/15	NET-OFFICE	-	21,9	PP-03-15 > TO-L1-022-B	TO-L1-022-B > PP-03-15	phone_or_spare FX-L1-101
C-TO-L2-001-A	TO-L2-001-A	L2-DINE	PP-03/16	SW-ACC-03/16	NET-DEMO	-	42,5	PP-03-16 > TO-L2-001-A	TO-L2-001-A > PP-03-16	display FX-L2-034
C-TO-L2-002-A	TO-L2-002-A	L2-GAME	PP-03/17	SW-ACC-03/17	NET-DEMO	-	24,7	PP-03-17 > TO-L2-002-A	TO-L2-002-A > PP-03-17	console FX-L2-058
C-TO-L2-002-B	TO-L2-002-B	L2-GAME	PP-03/18	SW-ACC-03/18	NET-DEMO	-	24,7	PP-03-18 > TO-L2-002-B	TO-L2-002-B > PP-03-18	display FX-L2-058
C-TO-L2-003-A	TO-L2-003-A	L2-GAME	PP-03/19	SW-ACC-03/19	NET-DEMO	-	19,1	PP-03-19 > TO-L2-003-A	TO-L2-003-A > PP-03-19	console FX-L2-061
C-TO-L2-003-B	TO-L2-003-B	L2-GAME	PP-03/20	SW-ACC-03/20	NET-DEMO	-	19,1	PP-03-20 > TO-L2-003-B	TO-L2-003-B > PP-03-20	display FX-L2-061
C-TO-L2-004-A	TO-L2-004-A	L2-GAME	PP-03/21	SW-ACC-03/21	NET-DEMO	-	24,6	PP-03-21 > TO-L2-004-A	TO-L2-004-A > PP-03-21	arcade FX-L2-064
C-TO-L2-005-A	TO-L2-005-A	L2-GAME	PP-03/22	SW-ACC-03/22	NET-DEMO	-	23,7	PP-03-22 > TO-L2-005-A	TO-L2-005-A > PP-03-22	arcade FX-L2-065
C-TO-L2-006-A	TO-L2-006-A	L2-BILLIARD	PP-03/23	SW-ACC-03/23	NET-DEMO	-	42,2	PP-03-23 > TO-L2-006-A	TO-L2-006-A > PP-03-23	display FX-L2-079
C-TO-L2-007-A	TO-L2-007-A	L2-GYM	PP-03/24	SW-ACC-03/24	NET-DEMO	-	34,2	PP-03-24 > TO-L2-007-A	TO-L2-007-A > PP-03-24	display FX-L2-087
Total	72 kabel						2074,8	port map: 2074,8 m	COCOK	

Label dua ujung: sisi rack 'PP-nn-pp > port outlet', sisi outlet sebaliknya. Panjang mengikuti AS-ICT-02; batas 90 m AS-ICT-03.

STATUS KONSEP

Bukan untuk konstruksi

kantor-rpg Proyek kantor-rpg · gedung KRPg-01

Port dan device schedule

Skala NTS @ A3 lanskap
Revisi P03 · 2026-10-01
Render 2026-10-02 02:42:18 UTC
Halaman 2/3
Digambar Claude Code cloud (generator)
Diperiksa Max (supervisor) belum review
Sumber world.json sha256 488597bb0552fbde

Huruf: Helvetica fallback (Alegreya Sans tidak tersedia saat build).

Nomor lembar

ICT-401

Rev P03 · 2/3

BOM RINGKAS DAN POE

BOM (tanpa harga): jumlah turunan dari port map; tanpa harga (AS-ICT-05)

Item	Satuan	Jumlah
Kabel tembaga horizontal (kategori TBD)	m	2074,8
Box kabel 305 m (pembulatan, belum termasuk waste)	box	7
Keystone jack sisi outlet	pcs	72
Faceplate 1 port	pcs	24
Faceplate 2 port	pcs	18
Faceplate 4 port	pcs	3
Patch panel 24 port	pcs	4
Patch cord sisi rack (1 per port terpakai, asumsi)	pcs	72
Patch cord sisi perangkat (1 per port terpakai, asumsi)	pcs	72
Access switch 48 port PoE (kelas, model TBD)	pcs	3
Access point (placeholder AS-ICT-01)	pcs	11
Kamera konsep (opsional)	pcs	5
Rack 42U (target)	pcs	2
UPS (rating TBD)	pcs	1

Harga: tidak ada (tidak ada quote bertanggal; tidak diestimasi; AS-ICT-05).

POE PER SWITCH (BELUM DIVALIDASI)

Switch	Port	Spare	Worst W	Budget W	Status
SW-ACC-01	24/48	20	407	belum ada	belum divalidasi: datasheet switch belum dipilih
SW-ACC-02	24/48	20	0	belum ada	belum divalidasi: datasheet switch belum dipilih
SW-ACC-03	24/48	20	0	belum ada	belum divalidasi: datasheet switch belum dipilih

Total PoE worst-case 407 W dari nilai PSE kelas IEEE (AS-ICT-04): belum divalidasi karena datasheet switch belum dipilih.

TOTAL

Outlet / port	45 / 72
Panjang kabel	2074,8 m (baris) vs 2074,8 m (port map): COCOK
Terpanjang / terpendek	50,6 / 12,7 m
Revisi data	port map P03 / world P03: sama

STATUS KONSEP

Bukan untuk konstruksi

kantor-rpg Proyek kantor-rpg · gedung KRPg-01

Port dan device schedule

Skala	NTS @ A3 lanskap
Revisi	P03 · 2026-10-01
Render	2026-10-02 02:42:18 UTC
Halaman	3/3
Digambar	Claude Code cloud (generator)
Diperiksa	Max (supervisor) belum review
Sumber	world.json sha256 488597bb0552fbde
Huruf: Helvetica fallback (Alegreya Sans tidak tersedia saat build).	

Nomor lembar

ICT-401

Rev P03 · 3/3