



JALUR KABEL L1 1:200 · tray +3,2 m

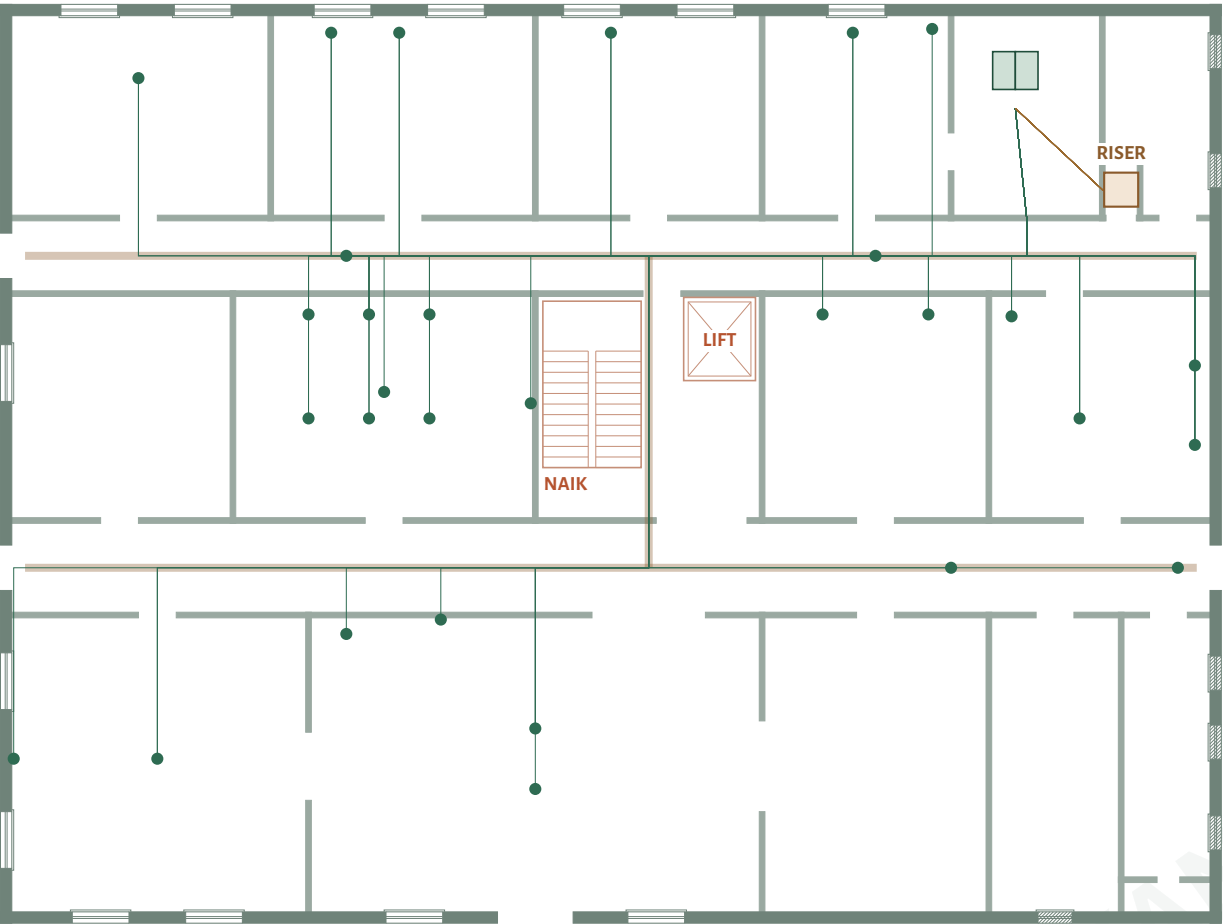

JALUR KABEL L2 1:200 · tray +3,2 m

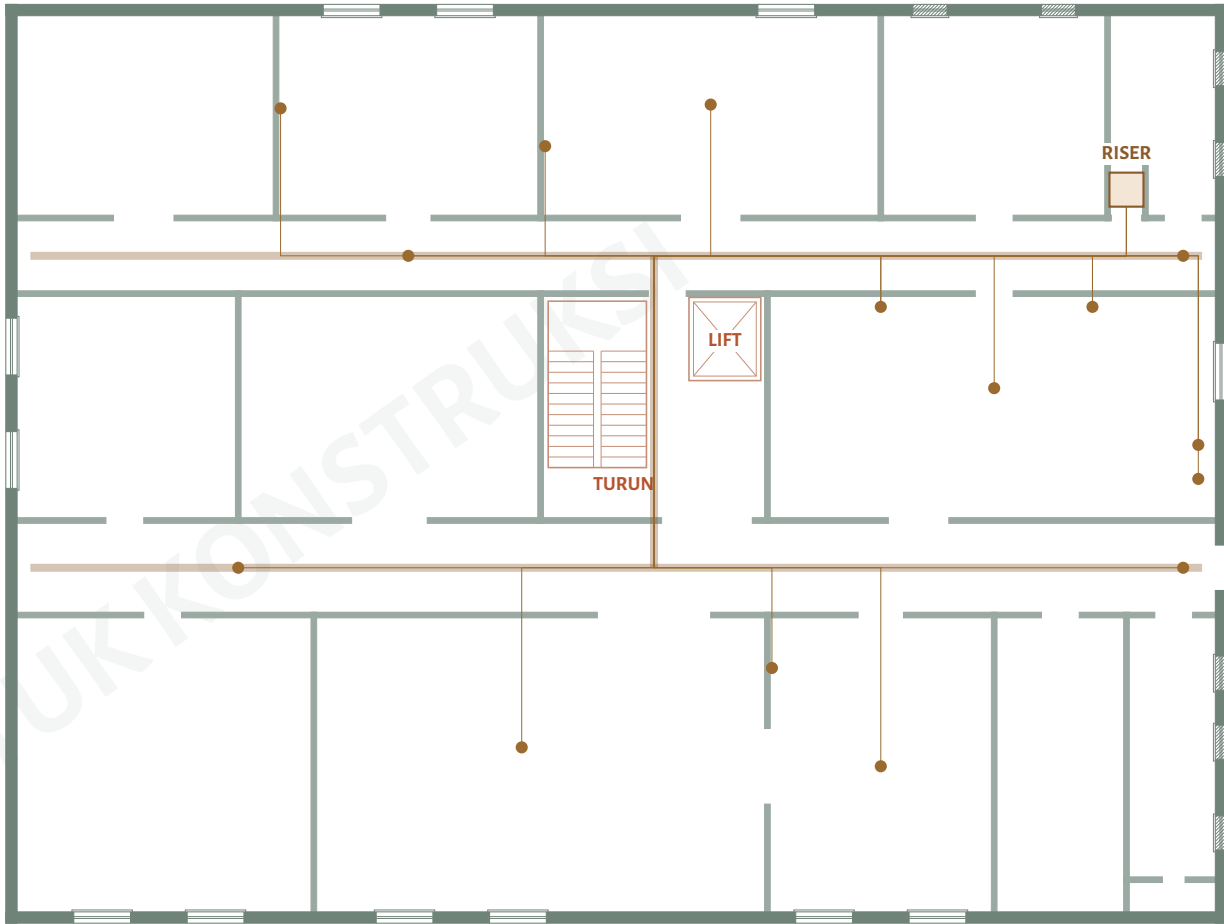


RINGKASAN PANJANG KABEL (ict-portmap.json)

Lantai	Kabel	Total m	Min m	Maks m	Rata m
L1	55	1537,1	12,7	50,6	27,9
L2	17	537,7	15,6	48,9	31,6
Total	72	2074,8	12,7	50,6	28,8

Cek: jumlah baris 2074,8 m vs total port map 2074,8 m: COCOK. Semua kabel di bawah target 90 m (AS-ICT-03).

SKEMA RISER

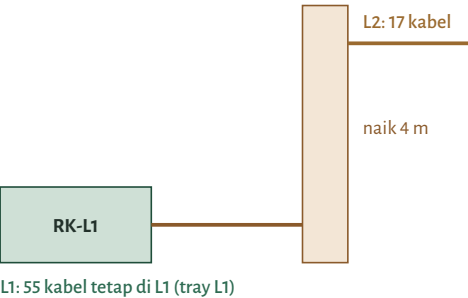

- Garis hijau = kabel endpoint L1, coklat = kabel endpoint L2 (bagian di L1 ikut warna lantai tujuan).
- Panjang = route tray + naik rack 1,2 m + riser 4,0 m (L2) + drop + slack 3,3 m (AS-ICT-02).



STATUS KONSEP

Bukan untuk konstruksi

kantor-rpg Proyek kantor-rpg · gedung KRPG-01
Pathway dan riser

Skala 1:200 @ A3 lanskap
Revisi P03 · 2026-10-01
Render 2026-10-02 00:29:26 UTC
Halaman 1/1
Digambar Claude Code cloud (generator)
Diperiksa Max (supervisor) belum review
Sumber world.json sha256 488597bb0552fbde

Huruf: KantorRPC Sans, turunan Alegreya Sans karya Juan Pablo del Peral (SILOFL1.1, paket Debian fonts-alegreya-sans), subset tertanam.

Nomor lembar

ICT-301

Rev P03 · 1/1